

Truss point-load schedules

Candidate 9 • Preliminary independent-analysis inputs

Load basis retained from the agreed study:

- Loft: 40 psf live; 75 psf in north/east storage bands; 12 psf floor dead load.
- Roof: 9.5 psf sloped assembly, 6.6 psf cap; roof live load 20 psf in plan.
- Metal walls: 4 psf. Actual modeled steel weight plus 10% connection allowance.
- Hoist: 1,000 lb lifted + 25% impact + 100 lb equipment = 1,350 lb point action.
Quarter, half and three-quarter span positions on B2 and T1; one hoist at a time.

Each truss receives only its own nodal loads and transferred connection actions.

There are separate basic-load cases, service combinations and strength combinations.

Diagnostic lateral/uplift and 125 psf storage cases are retained separately, not approved loads.

Use the interior loads with the exported interface movements for baseline replay.

At those restrained interfaces, listed actions are comparison reactions, NOT extra loads.

For optimization, model the surrounding stiffness or refresh the global model each iteration.

The following pages show the completed storage case and roof-first service case.


Every signed 3D force and moment, load case and exact point location is in the CSV/JSON.

Floor/roof load stations are not shifted to panel joints: doing that could hide chord bending.

These schedules are a starting load set, not final building-code or construction approval.

Roof framing distribution, joints, bracing, site wind/seismic, occupancy and foundations remain design inputs to verify. Existing garage walls provide no assumed capacity.


TE | Completed loft | service_patches

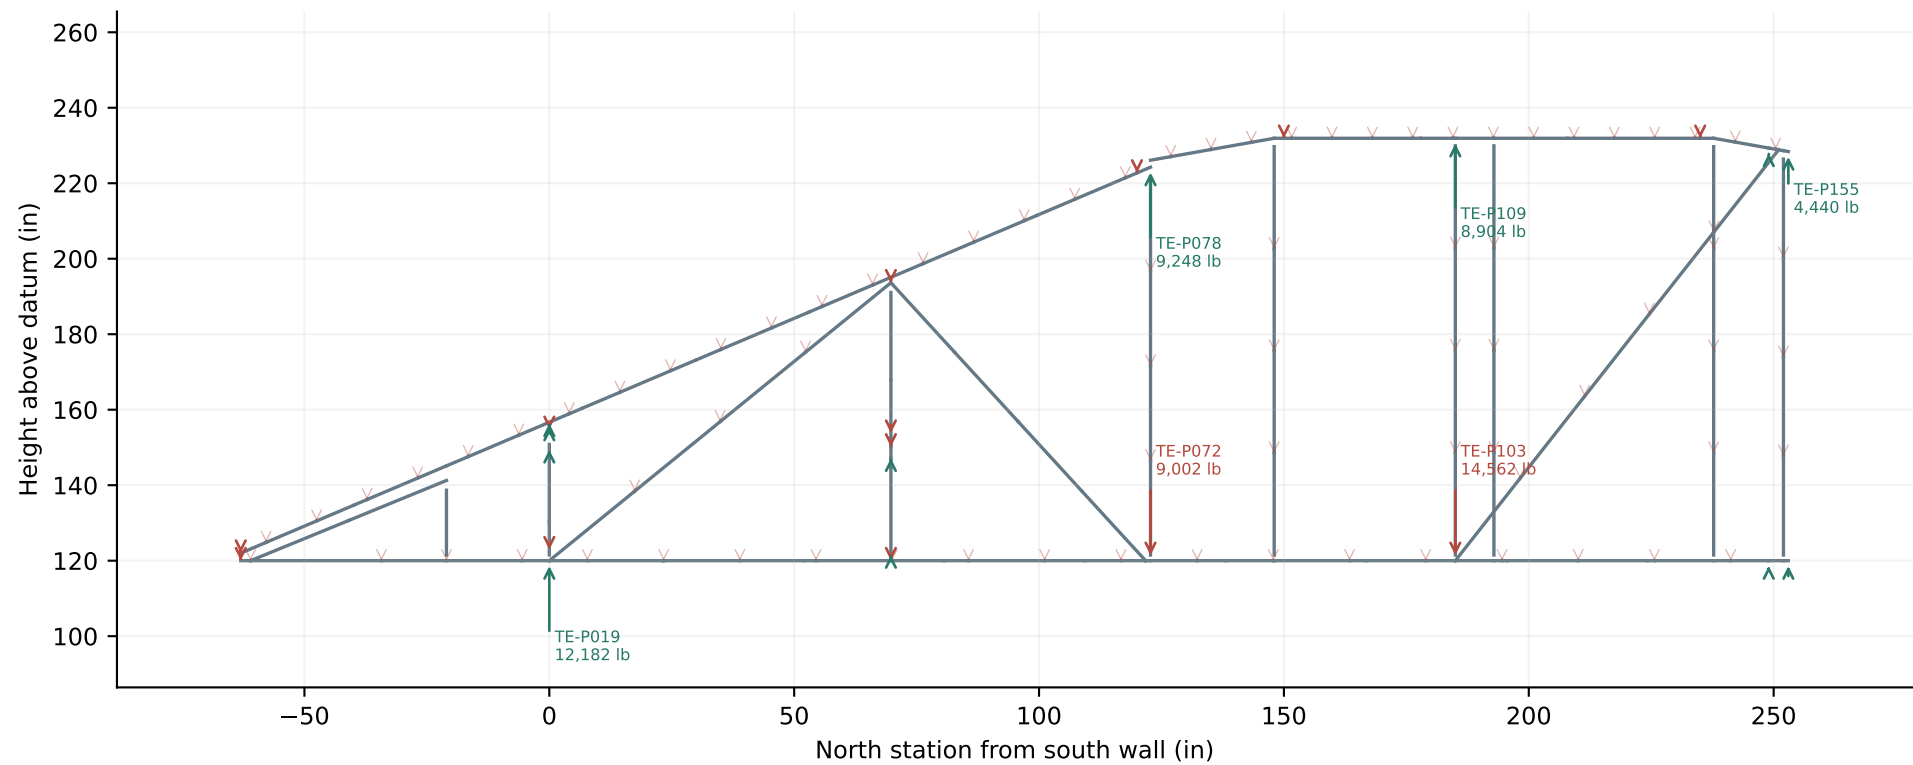

Interface actions: +FY upward, -FY downward. FX east; FZ north. Vertical arrows only; six largest interface forces labeled. Moments and exact vectors are in the CSV/JSON. Interior loads are also included there. Rounded labels are for reading only.

Point	Station in	Height in	Connected to	FY lb	FX lb	FZ lb
TE-P001	-63.00	120.00	S2, T-SO	-643	1	143
TE-P002	-63.00	122.00	S2	-35	-0	-1,071
TE-P019	0.00	120.00	S3	12,182	-237	1,043
TE-P020	-0.00	121.50	S3	-1,996	109	-500
TE-P021	0.00	130.31	S3	-9	-0	0
TE-P022	-0.00	150.80	S3	1,962	-109	500
TE-P023	0.00	153.37	BR-R-main-2, S3, T-S top / segment 1	-1,532	180	-364
TE-P024	0.00	156.37	S3	32	0	1
TE-P025	-0.00	156.68	S3	1,965	29	333
TE-P045	69.75	120.00	T1 future floor beam, T1 future...	-1,235	-681	-23
TE-P046	69.75	121.50	T1 future hanger 5	215	80	-4
TE-P047	69.75	144.69	T1 future hanger 5	-9	0	-0
TE-P048	69.75	147.14	T1 future hanger 5, T1 upper lower...	661	500	-22
TE-P049	69.75	150.14	T1 future hanger 5, T1 upper lower...	-33	2	-0
TE-P050	69.75	152.37	T1 upper lower chord	-2,273	87	18
TE-P053	69.75	193.64	T1 top / segment 1	-824	-97	8
TE-P070	120.00	222.73	BR-R-main-1	-33	199	116
TE-P072	122.76	120.00	BR-E-upper-1	-9,002	2	-5,013
TE-P078	122.76	224.25	BR-E-upper-2	9,248	-113	-5,610
TE-P093	150.00	231.91	BR-R-cap-2	-118	245	-77
TE-P103	185.00	120.00	B2 future floor beam, BR-E-upper-2	-14,562	-322	5,624
TE-P109	185.00	231.91	BR-E-upper-1	8,904	-2	5,013
TE-P132	235.00	231.91	BR-R-cap-1	-86	371	113
TE-P143	249.00	120.00	T-N, T-N vertical 4	1,728	-1,122	-531
TE-P144	249.00	229.32	N2, T-N diagonal 9, T-N top /...	1,333	463	-2,823
TE-P154	253.00	120.00	N2	2,475	880	400
TE-P155	253.00	228.40	N2	4,440	-466	2,728


TE | Roof-first stage | roof_first_service

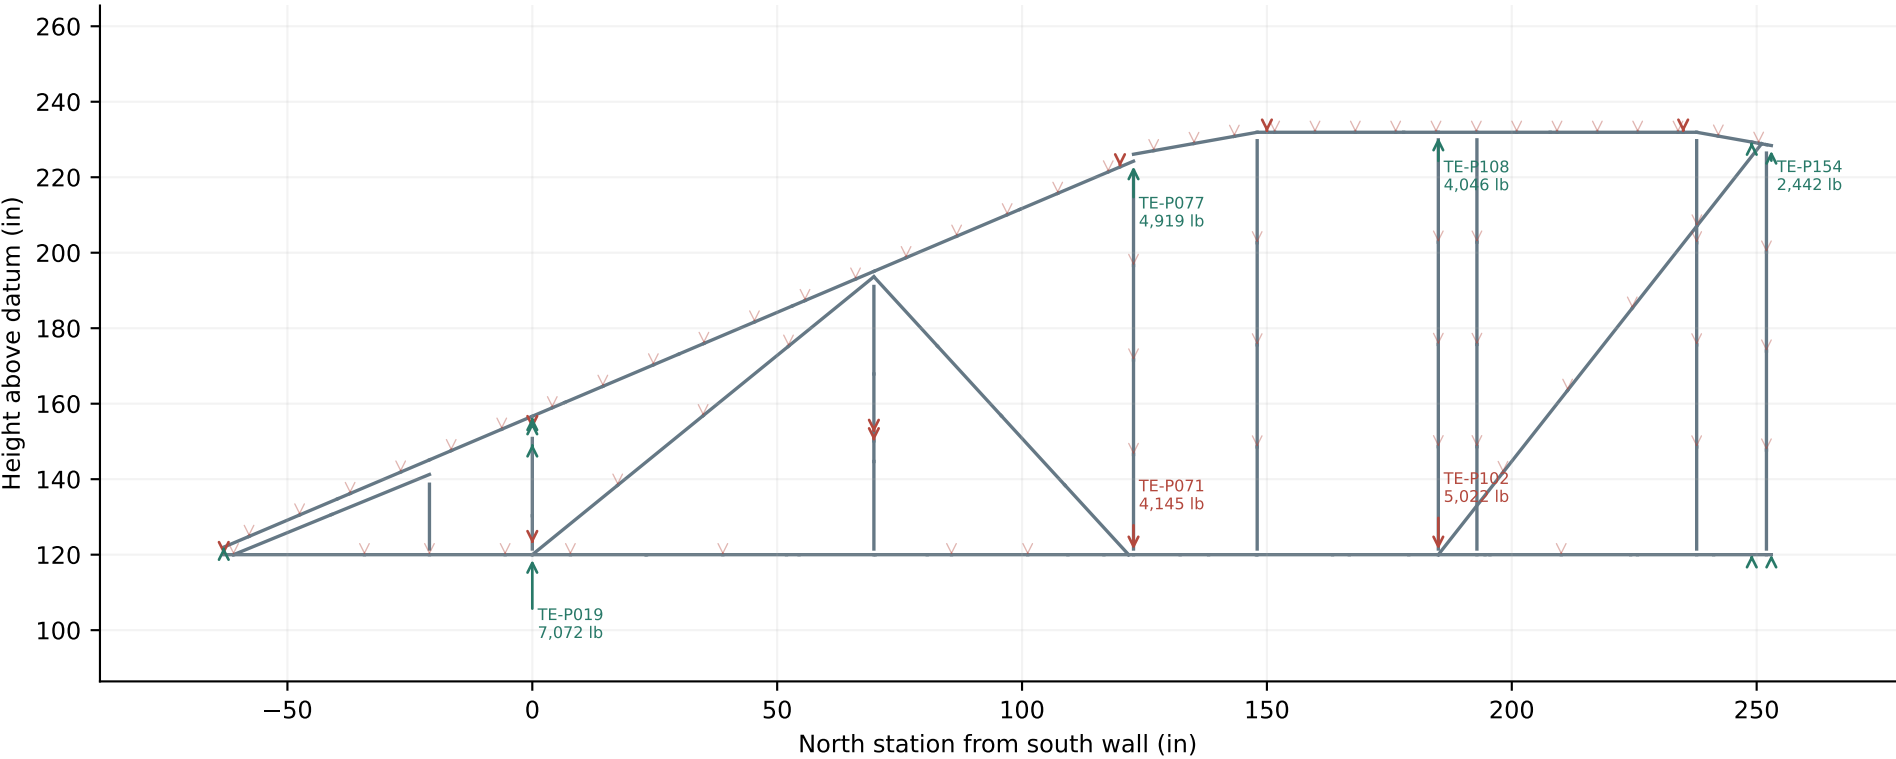

Interface actions: +FY upward, −FY downward. FX east; FZ north. Vertical arrows only; six largest interface forces labeled. Moments and exact vectors are in the CSV/JSON. Interior loads are also included there. Rounded labels are for reading only.

Point	Station in	Height in	Connected to	FY lb	FX lb	FZ lb
TE-P001	-63.00	120.00	S2, T-SO	-330	1	-571
TE-P002	-63.00	122.00	S2	671	19	5
TE-P019	0.00	120.00	S3	7,072	-139	659
TE-P020	-0.00	121.50	S3	-1,577	73	-240
TE-P021	0.00	130.31	S3	-9	-0	0
TE-P022	-0.00	150.80	S3	1,543	-73	240
TE-P023	0.00	153.37	BR-R-main-2, S3, T-S top / segment 1	-1,194	115	-171
TE-P024	0.00	156.37	S3	25	0	1
TE-P025	-0.00	156.68	S3	1,555	13	164
TE-P048	69.75	150.14	T1 upper lower chord	-201	-1	-6
TE-P049	69.75	152.37	T1 upper lower chord	-55	-25	4
TE-P052	69.75	193.64	T1 top / segment 1	-14	-10	3
TE-P069	120.00	222.73	BR-R-main-1	-81	21	31
TE-P071	122.76	120.00	BR-E-upper-1	-4,145	3	-2,296
TE-P077	122.76	224.25	BR-E-upper-2	4,919	-5	-2,996
TE-P092	150.00	231.91	BR-R-cap-2	-127	20	-7
TE-P102	185.00	120.00	BR-E-upper-2	-5,022	5	2,996
TE-P108	185.00	231.91	BR-E-upper-1	4,046	-3	2,296
TE-P131	235.00	231.91	BR-R-cap-1	-114	20	7
TE-P142	249.00	120.00	T-N, T-N vertical 4	1,105	-68	-295
TE-P143	249.00	229.32	N2, T-N diagonal 9, T-N top /...	370	-78	-1,349
TE-P153	253.00	120.00	N2	1,260	20	225
TE-P154	253.00	228.40	N2	2,442	90	1,300


TW | Completed loft | service_patches

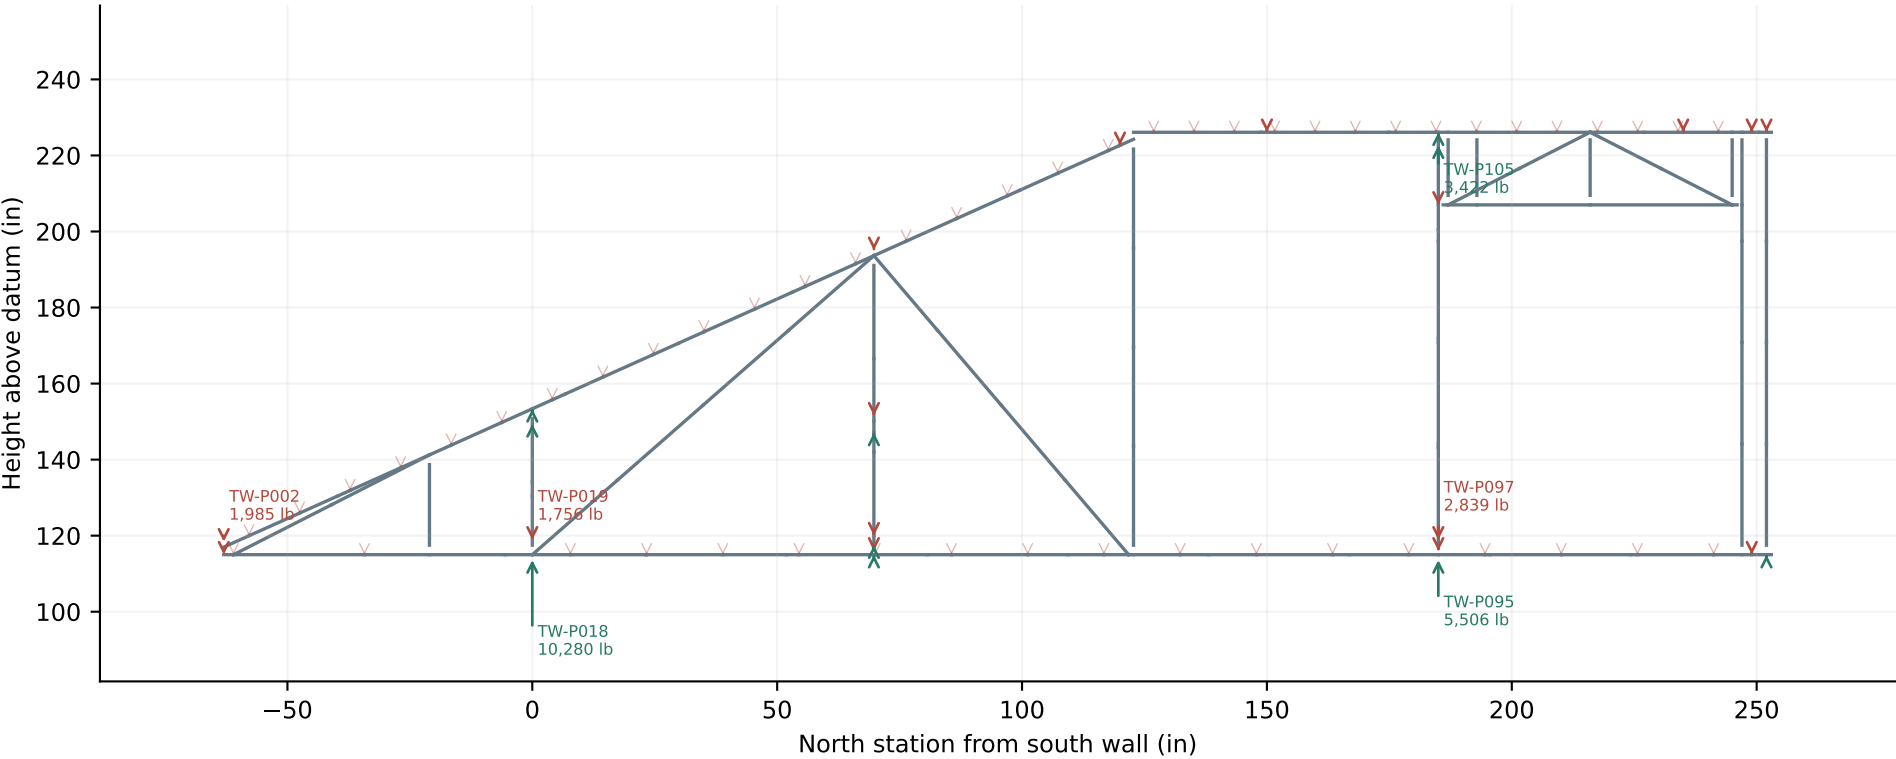

Interface actions: +FY upward, −FY downward. FX east; FZ north. Vertical arrows only; six largest interface forces labeled. Moments and exact vectors are in the CSV/JSON. Interior loads are also included there. Rounded labels are for reading only.

Point	Station in	Height in	Connected to	FY lb	FX lb	FZ lb
TW-P001	-63.00	115.00	SW0, T-SO	-1,239	11	4,498
TW-P002	-63.00	117.00	SW0	-1,985	-9	-4,433
TW-P018	0.00	115.00	T-S, W1	10,280	49	51
TW-P019	-0.00	117.50	W1	-1,756	-131	-365
TW-P020	0.00	130.31	W1	-4	0	0
TW-P021	-0.00	134.15	W1	-1	0	0
TW-P022	-0.00	150.80	W1	1,731	131	365
TW-P023	0.00	153.37	BR-R-main-1, T-S top / segment 1, W1	373	-150	-82
TW-P043	69.75	115.00	T1 future floor beam	247	50	-16
TW-P044	69.75	116.00	T1 future floor beam, T1 future...	-146	238	14
TW-P045	69.75	117.50	T1 future floor beam, T1 future...	395	-187	-30
TW-P046	69.75	120.00	T1 future floor beam, T1 future...	-398	187	30
TW-P047	69.75	142.02	T1 future hanger 1	-2	-0	0
TW-P048	69.75	147.14	T1 future hanger 1, T1 upper lower...	401	-187	-30
TW-P049	69.75	150.14	T1 future hanger 1, T1 upper lower...	-1,532	-10	29
TW-P052	69.75	193.64	T1 top / segment 1	-1,410	19	26
TW-P068	120.00	222.66	BR-R-main-2	-49	-87	47
TW-P085	150.00	226.09	BR-R-cap-1	-153	-358	-88
TW-P095	185.00	115.00	B2 future floor beam, BR-W-2, W3	5,506	442	-922
TW-P096	185.00	116.00	B2 future floor beam, W3	-128	509	-36
TW-P097	185.00	117.50	W3	-2,839	-553	55
TW-P098	185.00	143.18	W3	-6	0	-0
TW-P099	185.00	144.15	W3	-1	0	-0
TW-P100	185.00	170.80	W3	-1	0	-0
TW-P101	185.00	171.82	W3	-6	-0	-0
TW-P102	185.00	197.44	W3	-1	-0	-0
TW-P103	185.00	200.46	W3	-6	-0	0
TW-P104	185.00	207.00	W3	-708	170	1,580
TW-P105	185.00	224.09	W3	3,422	384	-1,622
TW-P106	185.00	226.09	W3	126	3	-13
TW-P135	235.00	226.09	BR-R-cap-2	-124	-258	52
TW-P151	249.00	115.00	BR-N-upper-1, T-N, W4	-36	-291	776
TW-P152	249.00	226.09	BR-N-upper-2, T-N top / segment 1,...	-180	29	84
TW-P153	250.41	226.09	T-N top / segment 1, W4	-2	0	-0
TW-P154	252.00	115.00	T-N, W4	168	2	3
TW-P160	252.00	226.09	T-N top / segment 1, W4	-138	-2	-3
TW-P161	253.00	115.00	BR-N-ground-2, BR-W-1, T-N, W4	9	0	29
TW-P162	253.00	226.09	T-N top / segment 1, W4	2	0	3


TW | Roof-first stage | roof_first_service

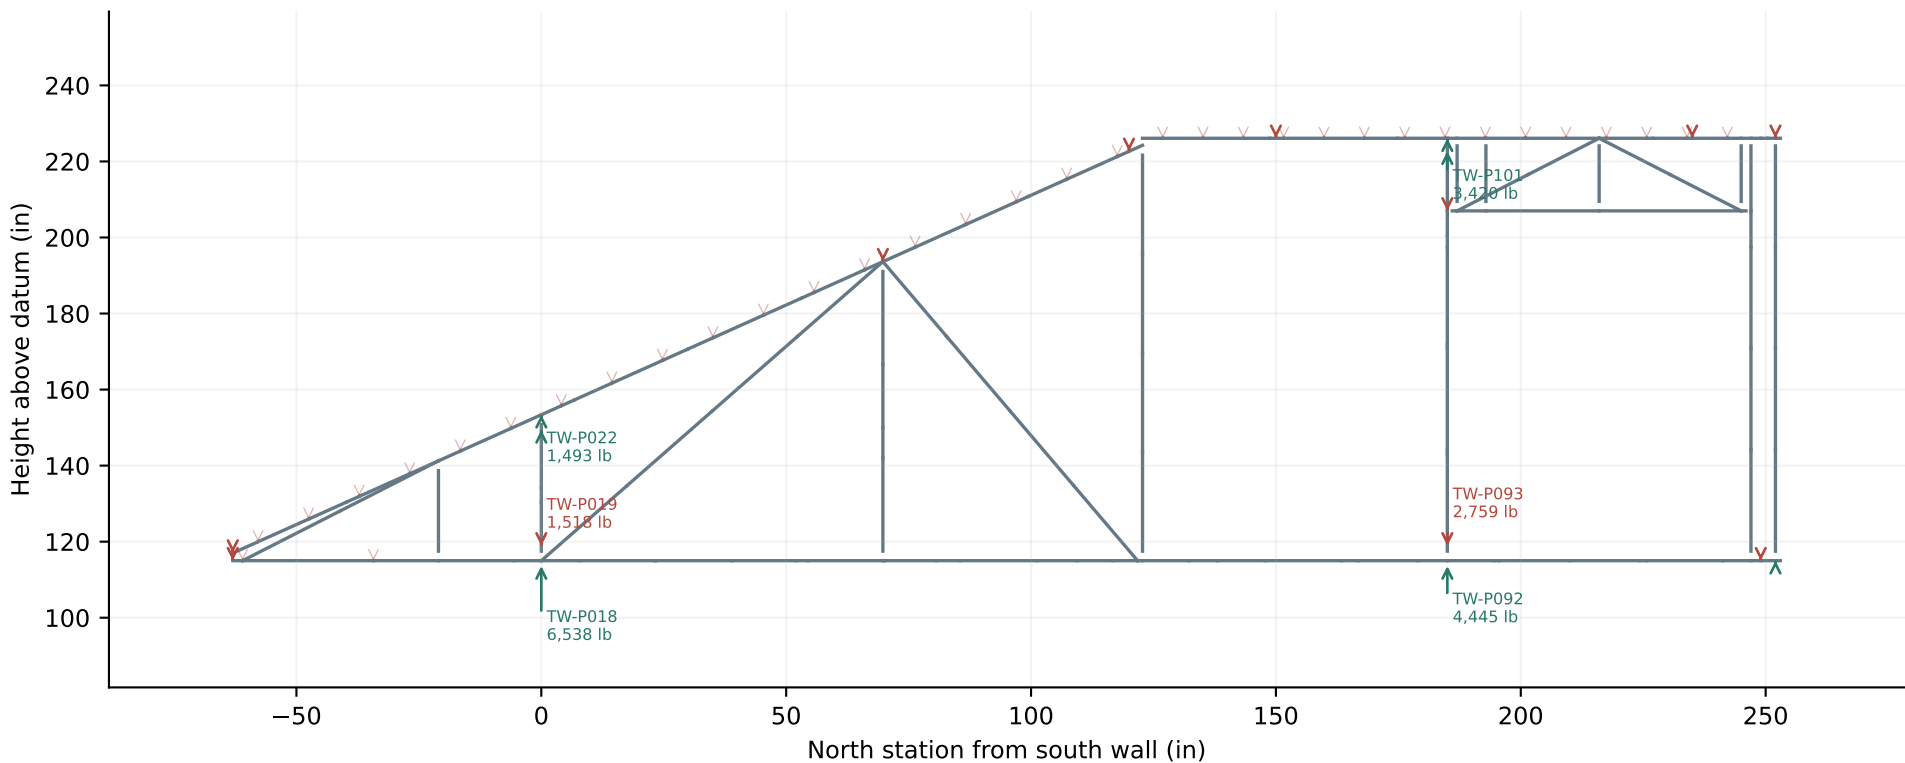

Interface actions: +FY upward, −FY downward. FX east; FZ north. Vertical arrows only; six largest interface forces labeled. Moments and exact vectors are in the CSV/JSON. Interior loads are also included there. Rounded labels are for reading only.

Point	Station in	Height in	Connected to	FY lb	FX lb	FZ lb
TW-P001	-63.00	115.00	SW0, T-SO	-739	-10	2,484
TW-P002	-63.00	117.00	SW0	-793	-5	-2,442
TW-P018	0.00	115.00	T-S, W1	6,538	112	23
TW-P019	-0.00	117.50	W1	-1,518	-99	-203
TW-P020	0.00	130.31	W1	-4	0	-0
TW-P021	-0.00	134.15	W1	-1	-0	0
TW-P022	-0.00	150.80	W1	1,493	99	203
TW-P023	0.00	153.37	BR-R-main-1, T-S top / segment 1, W1	376	-118	-16
TW-P046	69.75	150.14	T1 upper lower chord	-16	46	-8
TW-P049	69.75	193.64	T1 top / segment 1	-229	-10	8
TW-P065	120.00	222.66	BR-R-main-2	-71	-7	16
TW-P082	150.00	226.09	BR-R-cap-1	-116	-20	-3
TW-P092	185.00	115.00	BR-W-2, W3	4,445	2	-522
TW-P093	185.00	117.50	W3	-2,759	-36	47
TW-P094	185.00	143.18	W3	-6	-0	-0
TW-P095	185.00	144.15	W3	-1	0	-0
TW-P096	185.00	170.80	W3	-1	-0	-0
TW-P097	185.00	171.82	W3	-6	0	-0
TW-P098	185.00	197.44	W3	-1	0	-0
TW-P099	185.00	200.46	W3	-6	-0	-0
TW-P100	185.00	207.00	W3	-791	-0	1,550
TW-P101	185.00	224.09	W3	3,420	36	-1,584
TW-P102	185.00	226.09	W3	126	0	-13
TW-P131	235.00	226.09	BR-R-cap-2	-123	-21	4
TW-P147	249.00	115.00	BR-N-upper-1, T-N, W4	-47	32	398
TW-P148	249.00	226.09	BR-N-upper-2, T-N top / segment 1,...	-7	-2	44
TW-P149	250.41	226.09	T-N top / segment 1, W4	-2	-0	-0
TW-P150	252.00	115.00	T-N, W4	109	2	2
TW-P156	252.00	226.09	T-N top / segment 1, W4	-80	-2	-2
TW-P157	253.00	115.00	BR-N-ground-2, BR-W-1, T-N, W4	4	-0	14
TW-P158	253.00	226.09	T-N top / segment 1, W4	-0	0	1


TN | Completed loft | service_patches

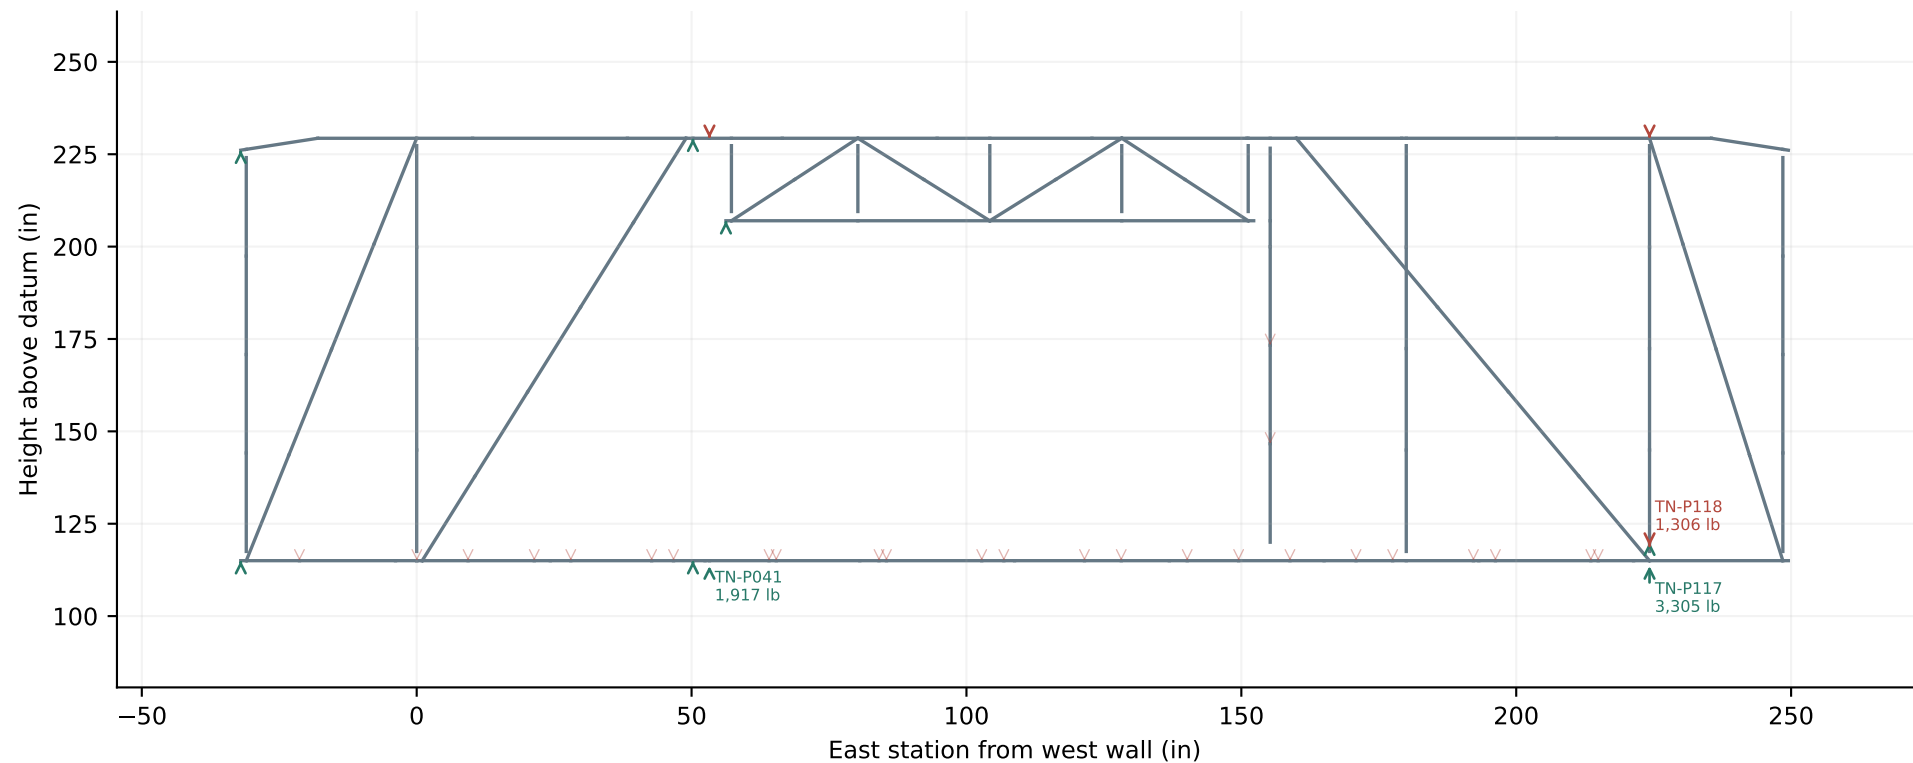

Interface actions: +FY upward, −FY downward. FX east; FZ north. Vertical arrows only; six largest interface forces labeled. Moments and exact vectors are in the CSV/JSON. Interior loads are also included there. Rounded labels are for reading only.

Point	Station in	Height in	Connected to	FY lb	FX lb	FZ lb
TN-P001	-32.00	115.00	BR-N-upper-1, T-W / B-WO, W4	312	-192	65
TN-P002	-32.00	226.09	BR-N-upper-2, T-W top / segment 2,...	72	192	-14
TN-P038	50.25	115.00	BR-N-upper-2	221	-192	-1
TN-P039	50.25	229.32	BR-N-upper-1	606	482	10
TN-P041	53.25	115.00	N1 / U-W	1,917	-773	-50
TN-P042	53.25	229.32	N1 / U-W	-469	-554	13
TN-P043	56.25	207.00	N1 / U-W	375	873	-10
TN-P117	224.25	115.00	N2, T-E	3,305	-327	-281
TN-P118	224.25	117.50	T-E	-1,306	562	267
TN-P119	224.25	120.00	T-E	892	-3	-4
TN-P124	224.25	229.32	N2, T-E top / segment 4	-401	-67	5


TN | Roof-first stage | roof_first_service

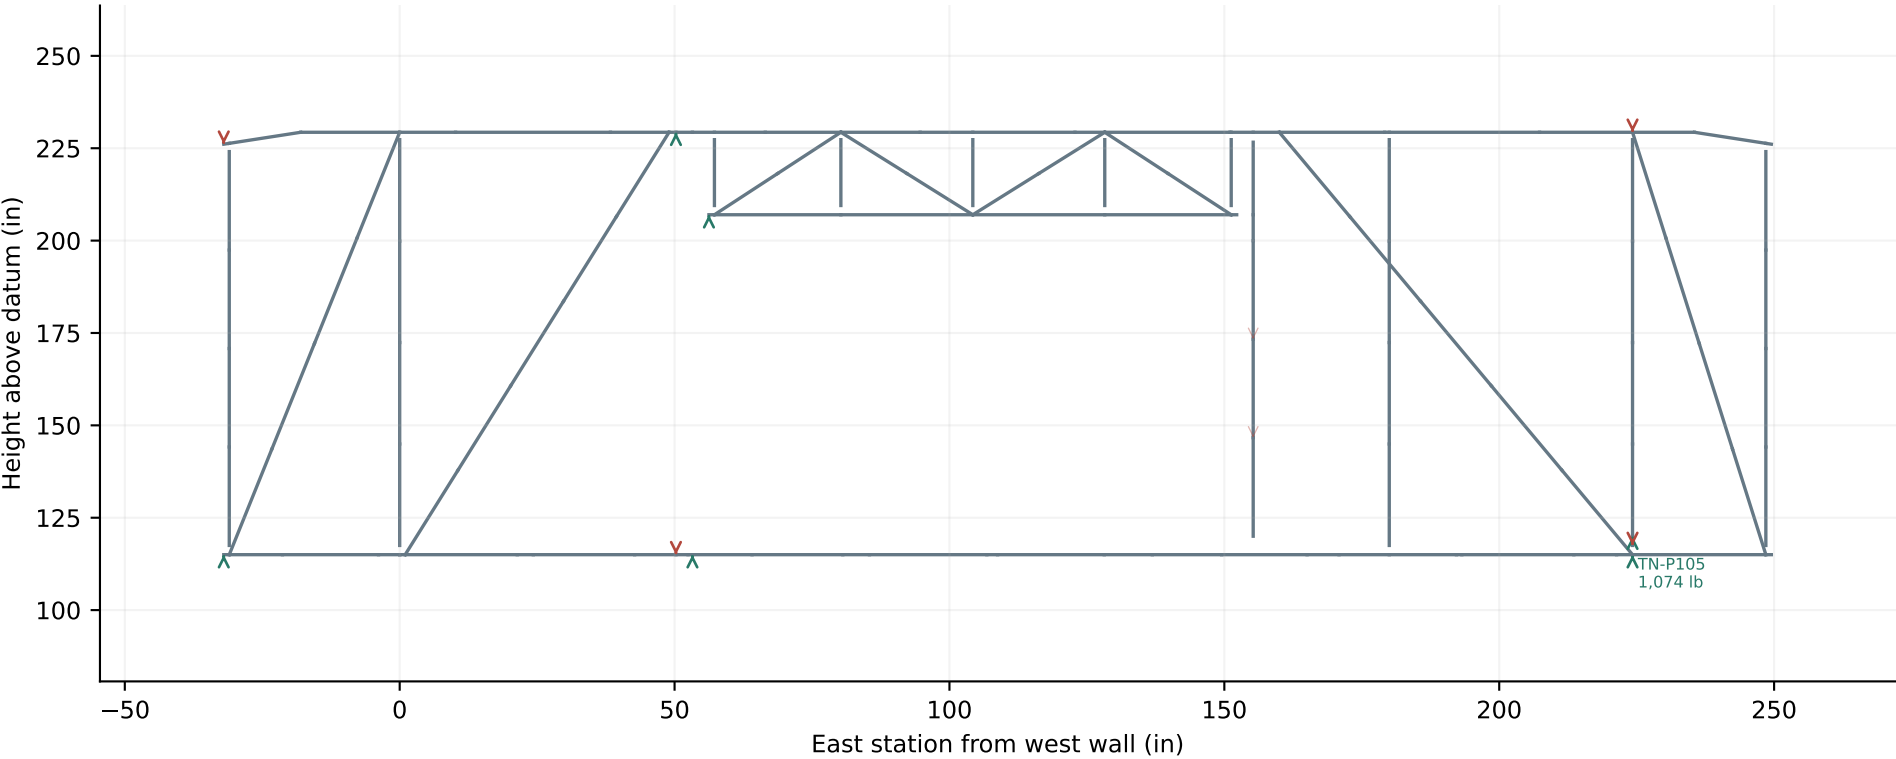

Interface actions: +FY upward, −FY downward. FX east; FZ north. Vertical arrows only; six largest interface forces labeled. Moments and exact vectors are in the CSV/JSON. Interior loads are also included there. Rounded labels are for reading only.

Point	Station in	Height in	Connected to	FY lb	FX lb	FZ lb
TN-P001	-32.00	115.00	BR-N-upper-1, T-W / B-WO, W4	322	-148	5
TN-P002	-32.00	226.09	BR-N-upper-2, T-W top / segment 2,...	-191	41	-5
TN-P035	50.25	115.00	BR-N-upper-2	-48	-4	-2
TN-P036	50.25	229.32	BR-N-upper-1	42	63	1
TN-P038	53.25	115.00	N1 / U-W	109	-33	-1
TN-P039	53.25	229.32	N1 / U-W	-15	-127	4
TN-P040	56.25	207.00	N1 / U-W	148	164	-4
TN-P105	224.25	115.00	N2, T-E	1,074	45	-150
TN-P106	224.25	117.50	T-E	-791	35	148
TN-P107	224.25	120.00	T-E	476	-1	-2
TN-P112	224.25	229.32	N2, T-E top / segment 4	-392	-35	5


TS | Completed loft | service_patches

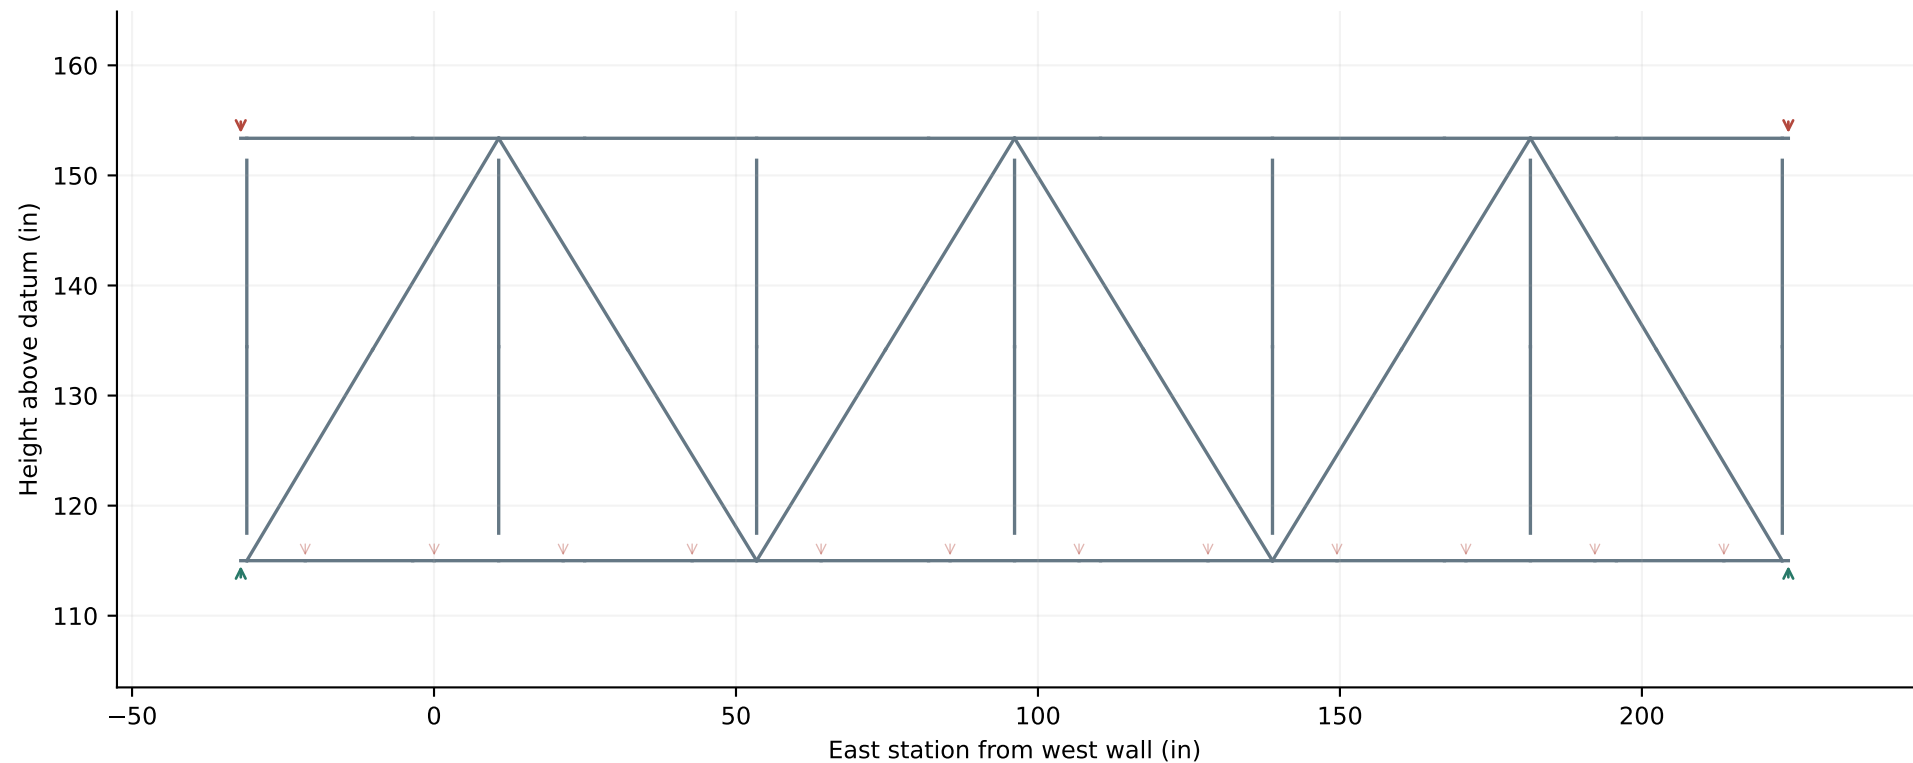

Interface actions: +FY upward, −FY downward. FX east; FZ north. Vertical arrows only; six largest interface forces labeled. Moments and exact vectors are in the CSV/JSON. Interior loads are also included there. Rounded labels are for reading only.

Point	Station in	Height in	Connected to	FY lb	FX lb	FZ lb
TS-P001	-32.00	115.00	T-W / B-WO, T-W diagonal 9, T-W...	886	-50	11
TS-P002	-32.00	153.37	BR-R-main-1, T-W top / segment 1,...	-489	-128	-17
TS-P068	224.25	115.00	BR-E-ground-1, S3, T-E	850	221	31
TS-P069	224.25	153.37	BR-R-main-2, S3, T-E top / segment...	-504	-42	-25


TS | Roof-first stage | roof_first_service

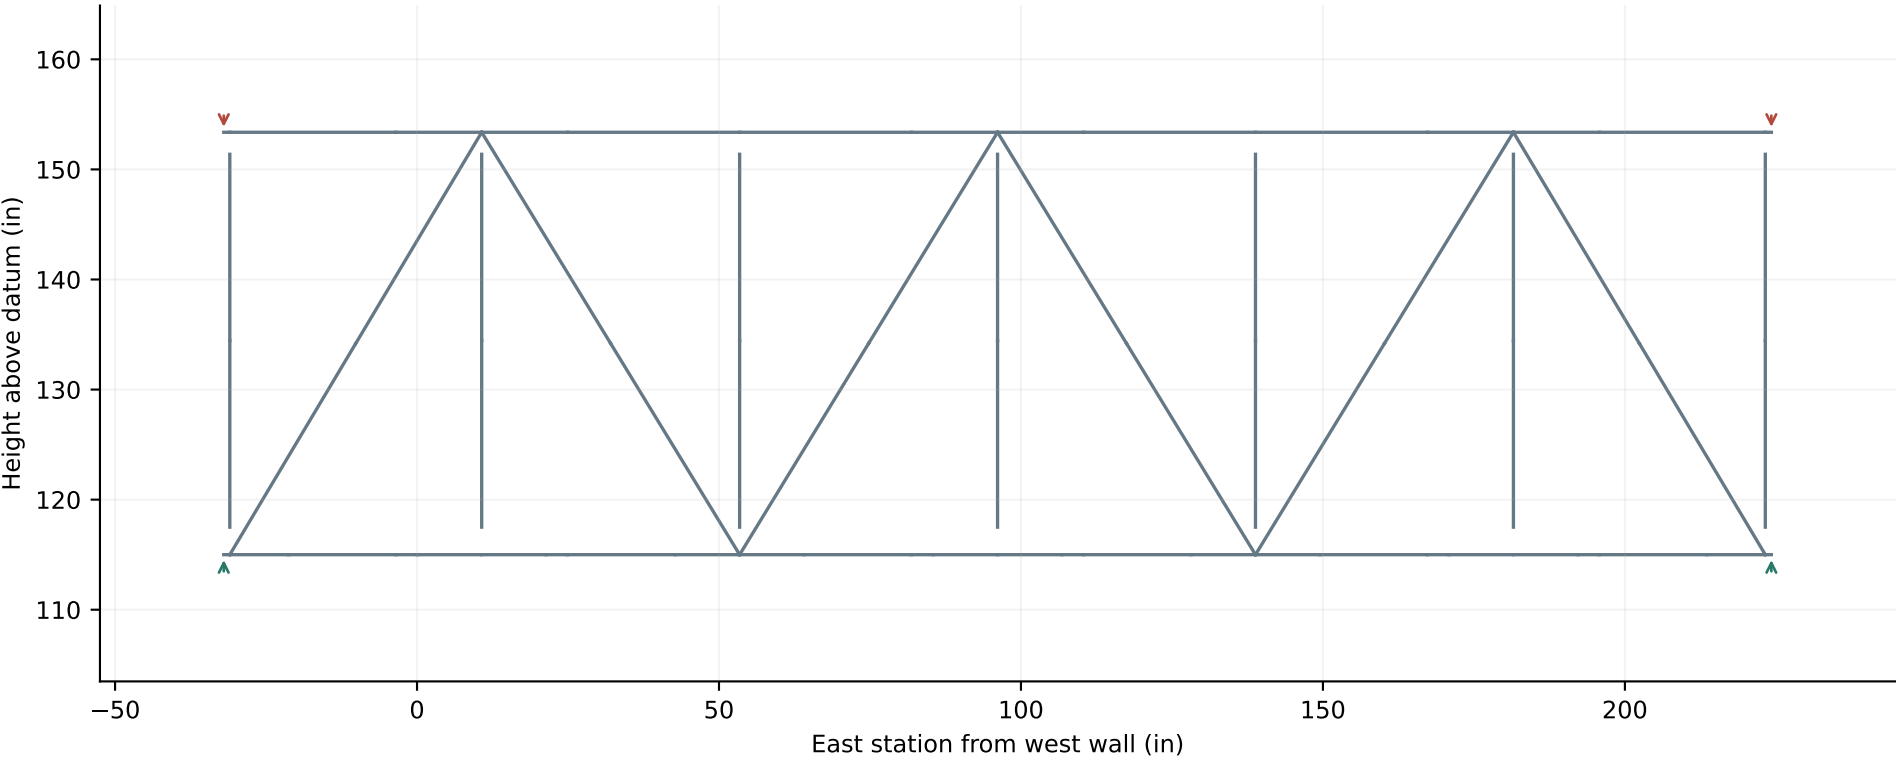

Interface actions: +FY upward, −FY downward. FX east; FZ north. Vertical arrows only; six largest interface forces labeled. Moments and exact vectors are in the CSV/JSON. Interior loads are also included there. Rounded labels are for reading only.

Point	Station in	Height in	Connected to	FY lb	FX lb	FZ lb
TS-P001	-32.00	115.00	T-W / B-WO, T-W diagonal 9, T-W...	699	-110	7
TS-P002	-32.00	153.37	BR-R-main-1, T-W top / segment 1,...	-454	12	-8
TS-P068	224.25	115.00	BR-E-ground-1, S3, T-E	667	136	14
TS-P069	224.25	153.37	BR-R-main-2, S3, T-E top / segment...	-429	-38	-13


T1 | Completed loft | service_patches

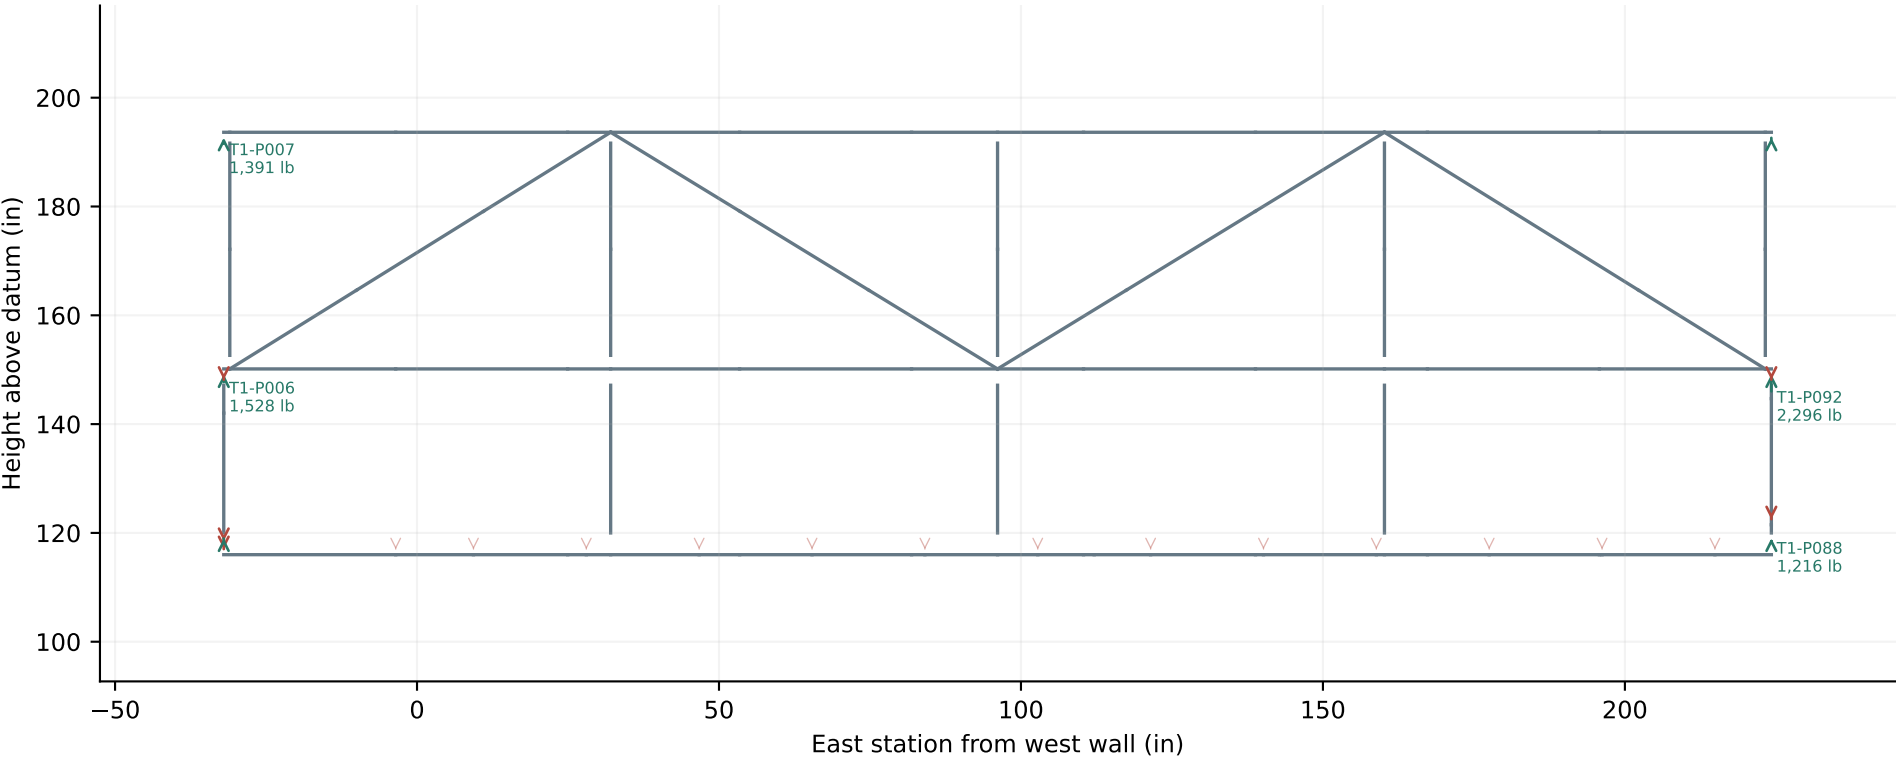

Interface actions: +FY upward, −FY downward. FX east; FZ north. Vertical arrows only; six largest interface forces labeled. Moments and exact vectors are in the CSV/JSON. Interior loads are also included there. Rounded labels are for reading only.

Point	Station in	Height in	Connected to	FY lb	FX lb	FZ lb
T1-P001	-32.00	116.00	T-W / B-WO, T-W vertical 3	-129	-288	2
T1-P002	-32.00	117.50	T-W / B-WO, T-W vertical 3	-398	187	30
T1-P003	-32.00	120.00	T-W vertical 3	395	-187	-30
T1-P004	-32.00	142.02	T-W vertical 3	-2	-0	0
T1-P005	-32.00	147.14	T-W vertical 3	-404	187	30
T1-P006	-32.00	150.14	T-W vertical 3	1,528	10	-29
T1-P007	-32.00	193.64	T-W diagonal 10, T-W diagonal 9,...	1,391	-19	-26
T1-P088	224.25	120.00	T-E, T-E vertical 3	1,216	681	23
T1-P089	224.25	121.50	T-E, T-E vertical 3	-224	-80	4
T1-P090	224.25	144.69	T-E vertical 3	-3	0	0
T1-P091	224.25	147.14	T-E vertical 3	-665	-500	22
T1-P092	224.25	150.14	T-E vertical 3	2,296	-89	-18
T1-P093	224.25	193.64	T-E diagonal 11, T-E diagonal 12,...	805	97	-8

T1 | Roof-first stage | roof_first_service

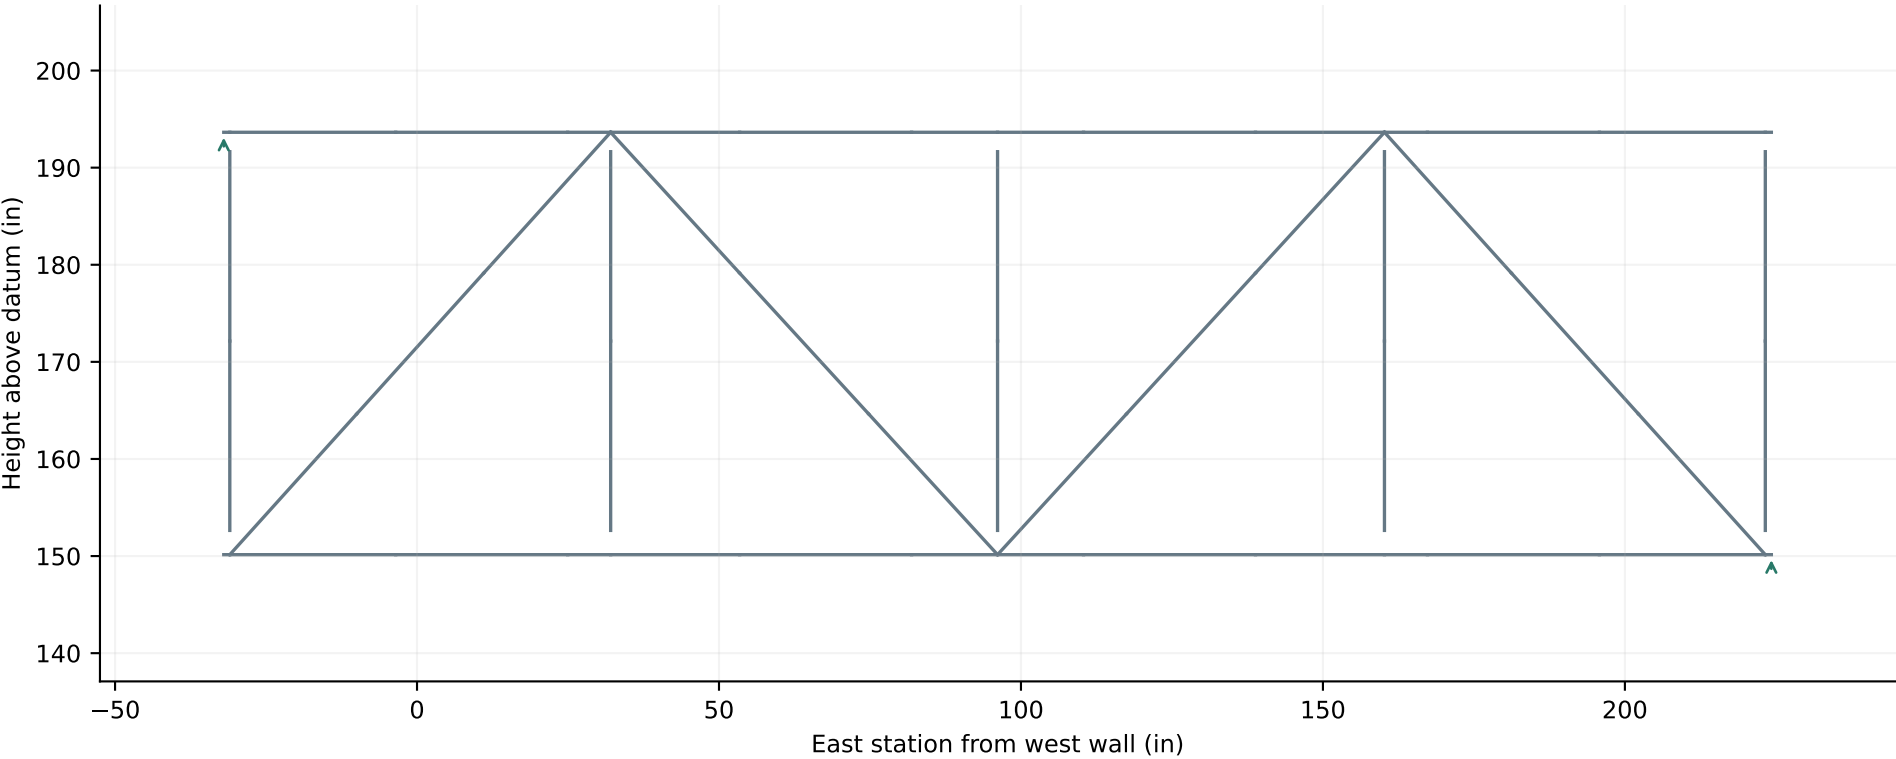

Interface actions: +FY upward, −FY downward. FX east; FZ north. Vertical arrows only; six largest interface forces labeled. Moments and exact vectors are in the CSV/JSON. Interior loads are also included there. Rounded labels are for reading only.

Point	Station in	Height in	Connected to	FY lb	FX lb	FZ lb
T1-P001	-32.00	150.14	T-W vertical 3	12	-46	8
T1-P002	-32.00	193.64	T-W diagonal 10, T-W diagonal 9,...	209	10	-8
T1-P052	224.25	150.14	T-E vertical 3	246	26	2
T1-P053	224.25	193.64	T-E diagonal 11, T-E diagonal 12,...	-5	10	-3