


# T-E · TRUSS ELEVATION

South → north · station zero = south exterior garage wall · member layout projected directly from the current 3D model

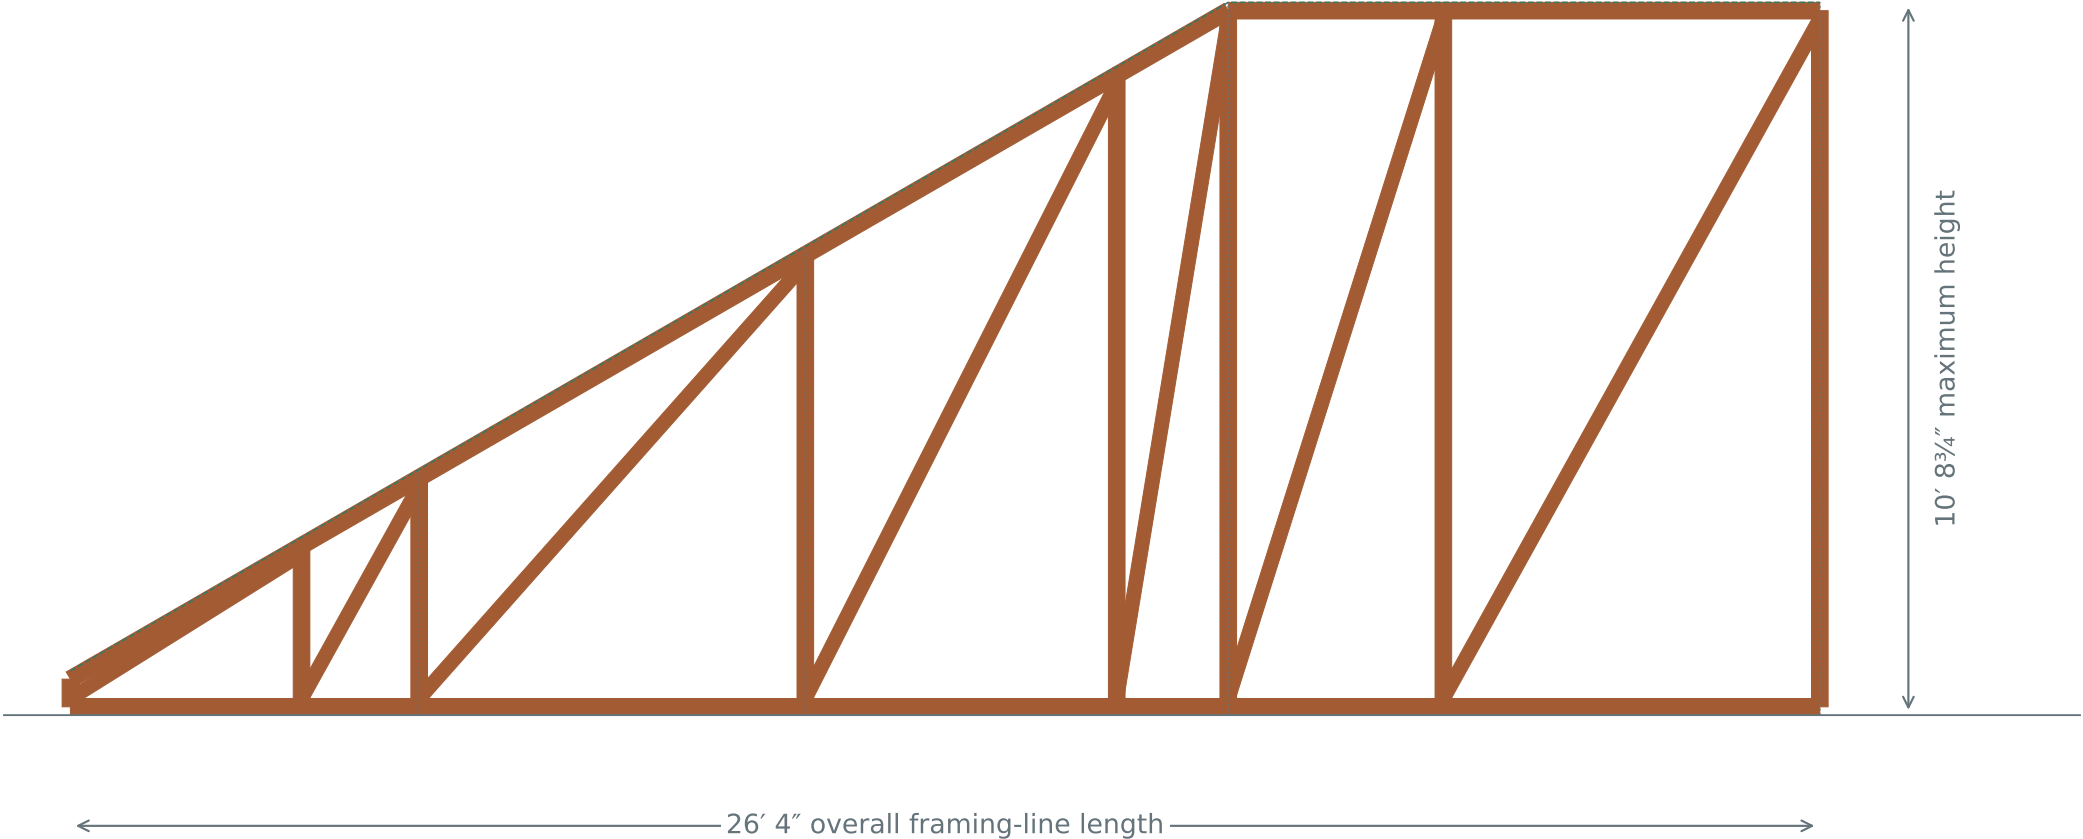

**COMMON BOTTOM = 8' 2½" ABOVE GROUND · COLUMN-SUPPORTED**

UPRIGHT STATIONS FROM SOUTH WALL (in): -63, -21.25, 0, 69.75, 126, 146.15, 185, 253  
PANEL SPACINGS (in): 41.75, 21.25, 69.75, 56.25, 20.15, 38.85, 68  
DEPTHS: south tip 8"; south wall 3' 8⅜"; at T1 7' 0⅝"; plateau 10' 8¾".  
Support axis: N2 / S2 / optional S3.

Concept geometry, not fabrication drawings. Member sizes, joints, bracing and bearing details require design.  
The shallow hip roof cap sits above the rear ceiling datum; its internal framing has not been laid out.