


T-N · TRUSS ELEVATION

West → east · dimensions along the framing line · member layout projected directly from the current 3D model

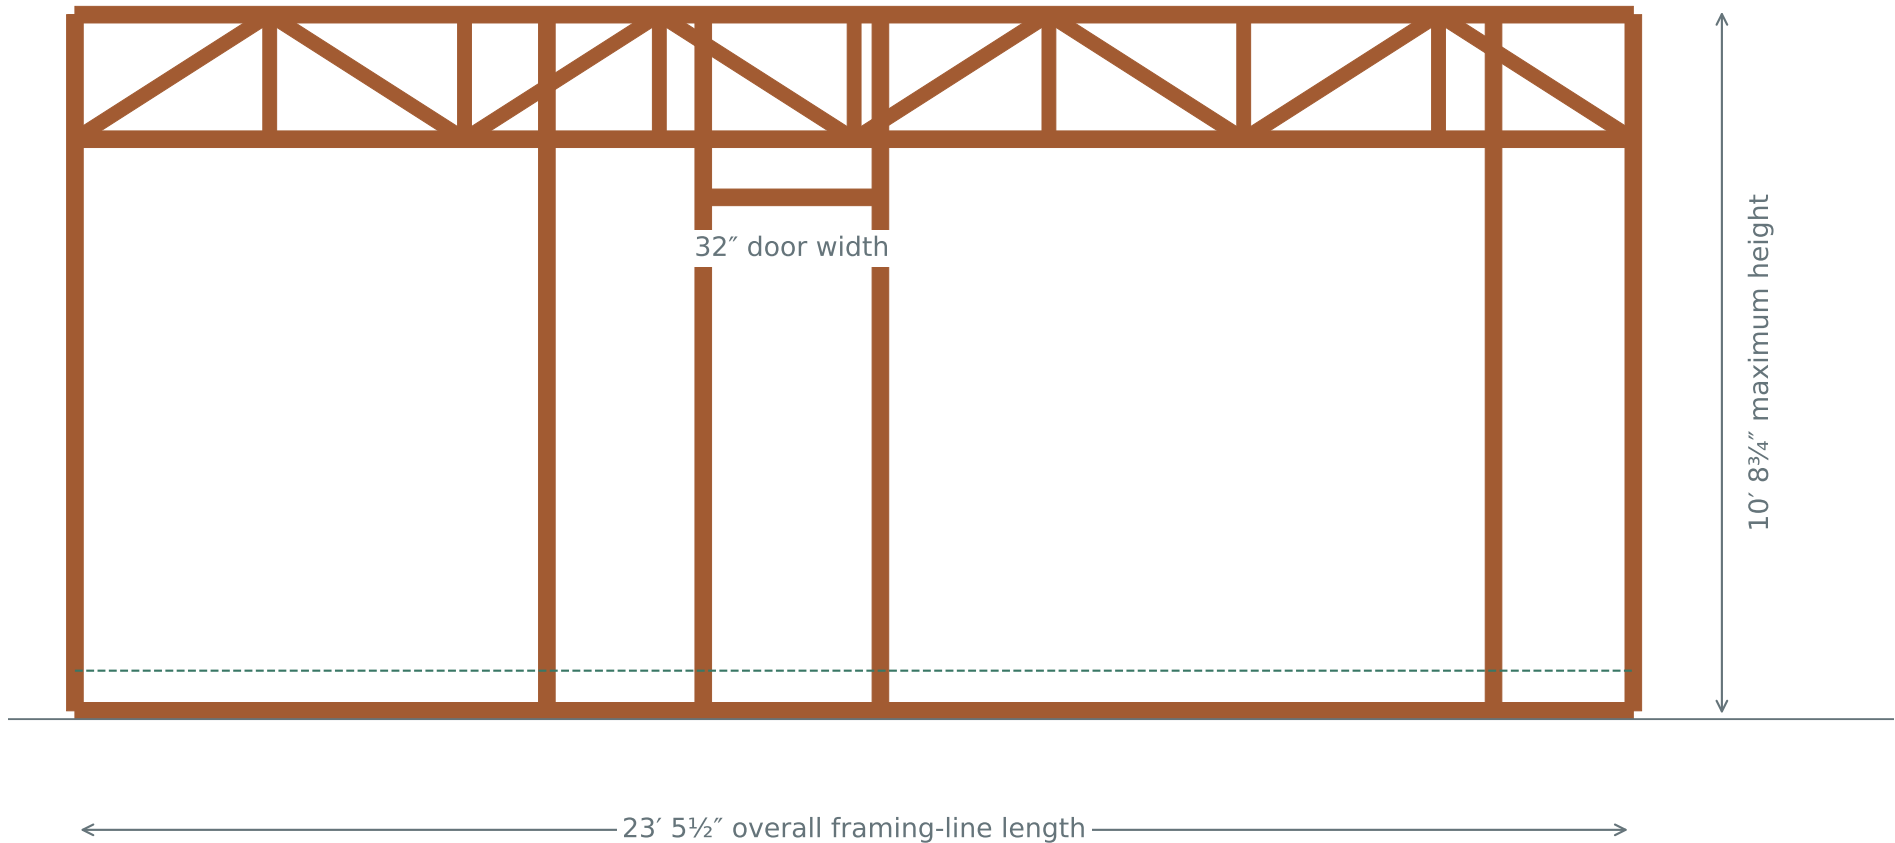

COMMON BOTTOM = 8' 2½" ABOVE GROUND · COLUMN-SUPPORTED

UPRIGHT STATIONS X (in): -32, 53.25, 81.5, 113.5, 224.25, 249.5.
HEADER: nominal 24" deep; eight equal bays of 35 3/16 in. Door: 32" wide × 84" high above loft floor.
DOOR center X = 97½"; opening edges X = 81½" / 113½". Floor is 8¾" above common truss bottom.
North wall windows and side webs require coordination. Overall truss includes west walkway width; it is not loft-floor width.

Concept geometry, not fabrication drawings. Member sizes, joints, bracing and bearing details require design.
The shallow hip roof cap sits above the rear ceiling datum; its internal framing has not been laid out.