


GARAGE / UPPER STRUCTURE + COLUMNS

03 Earlier floor-plan base • north up • dimensions in feet and inches

Discussion sketch | September 15, 2026

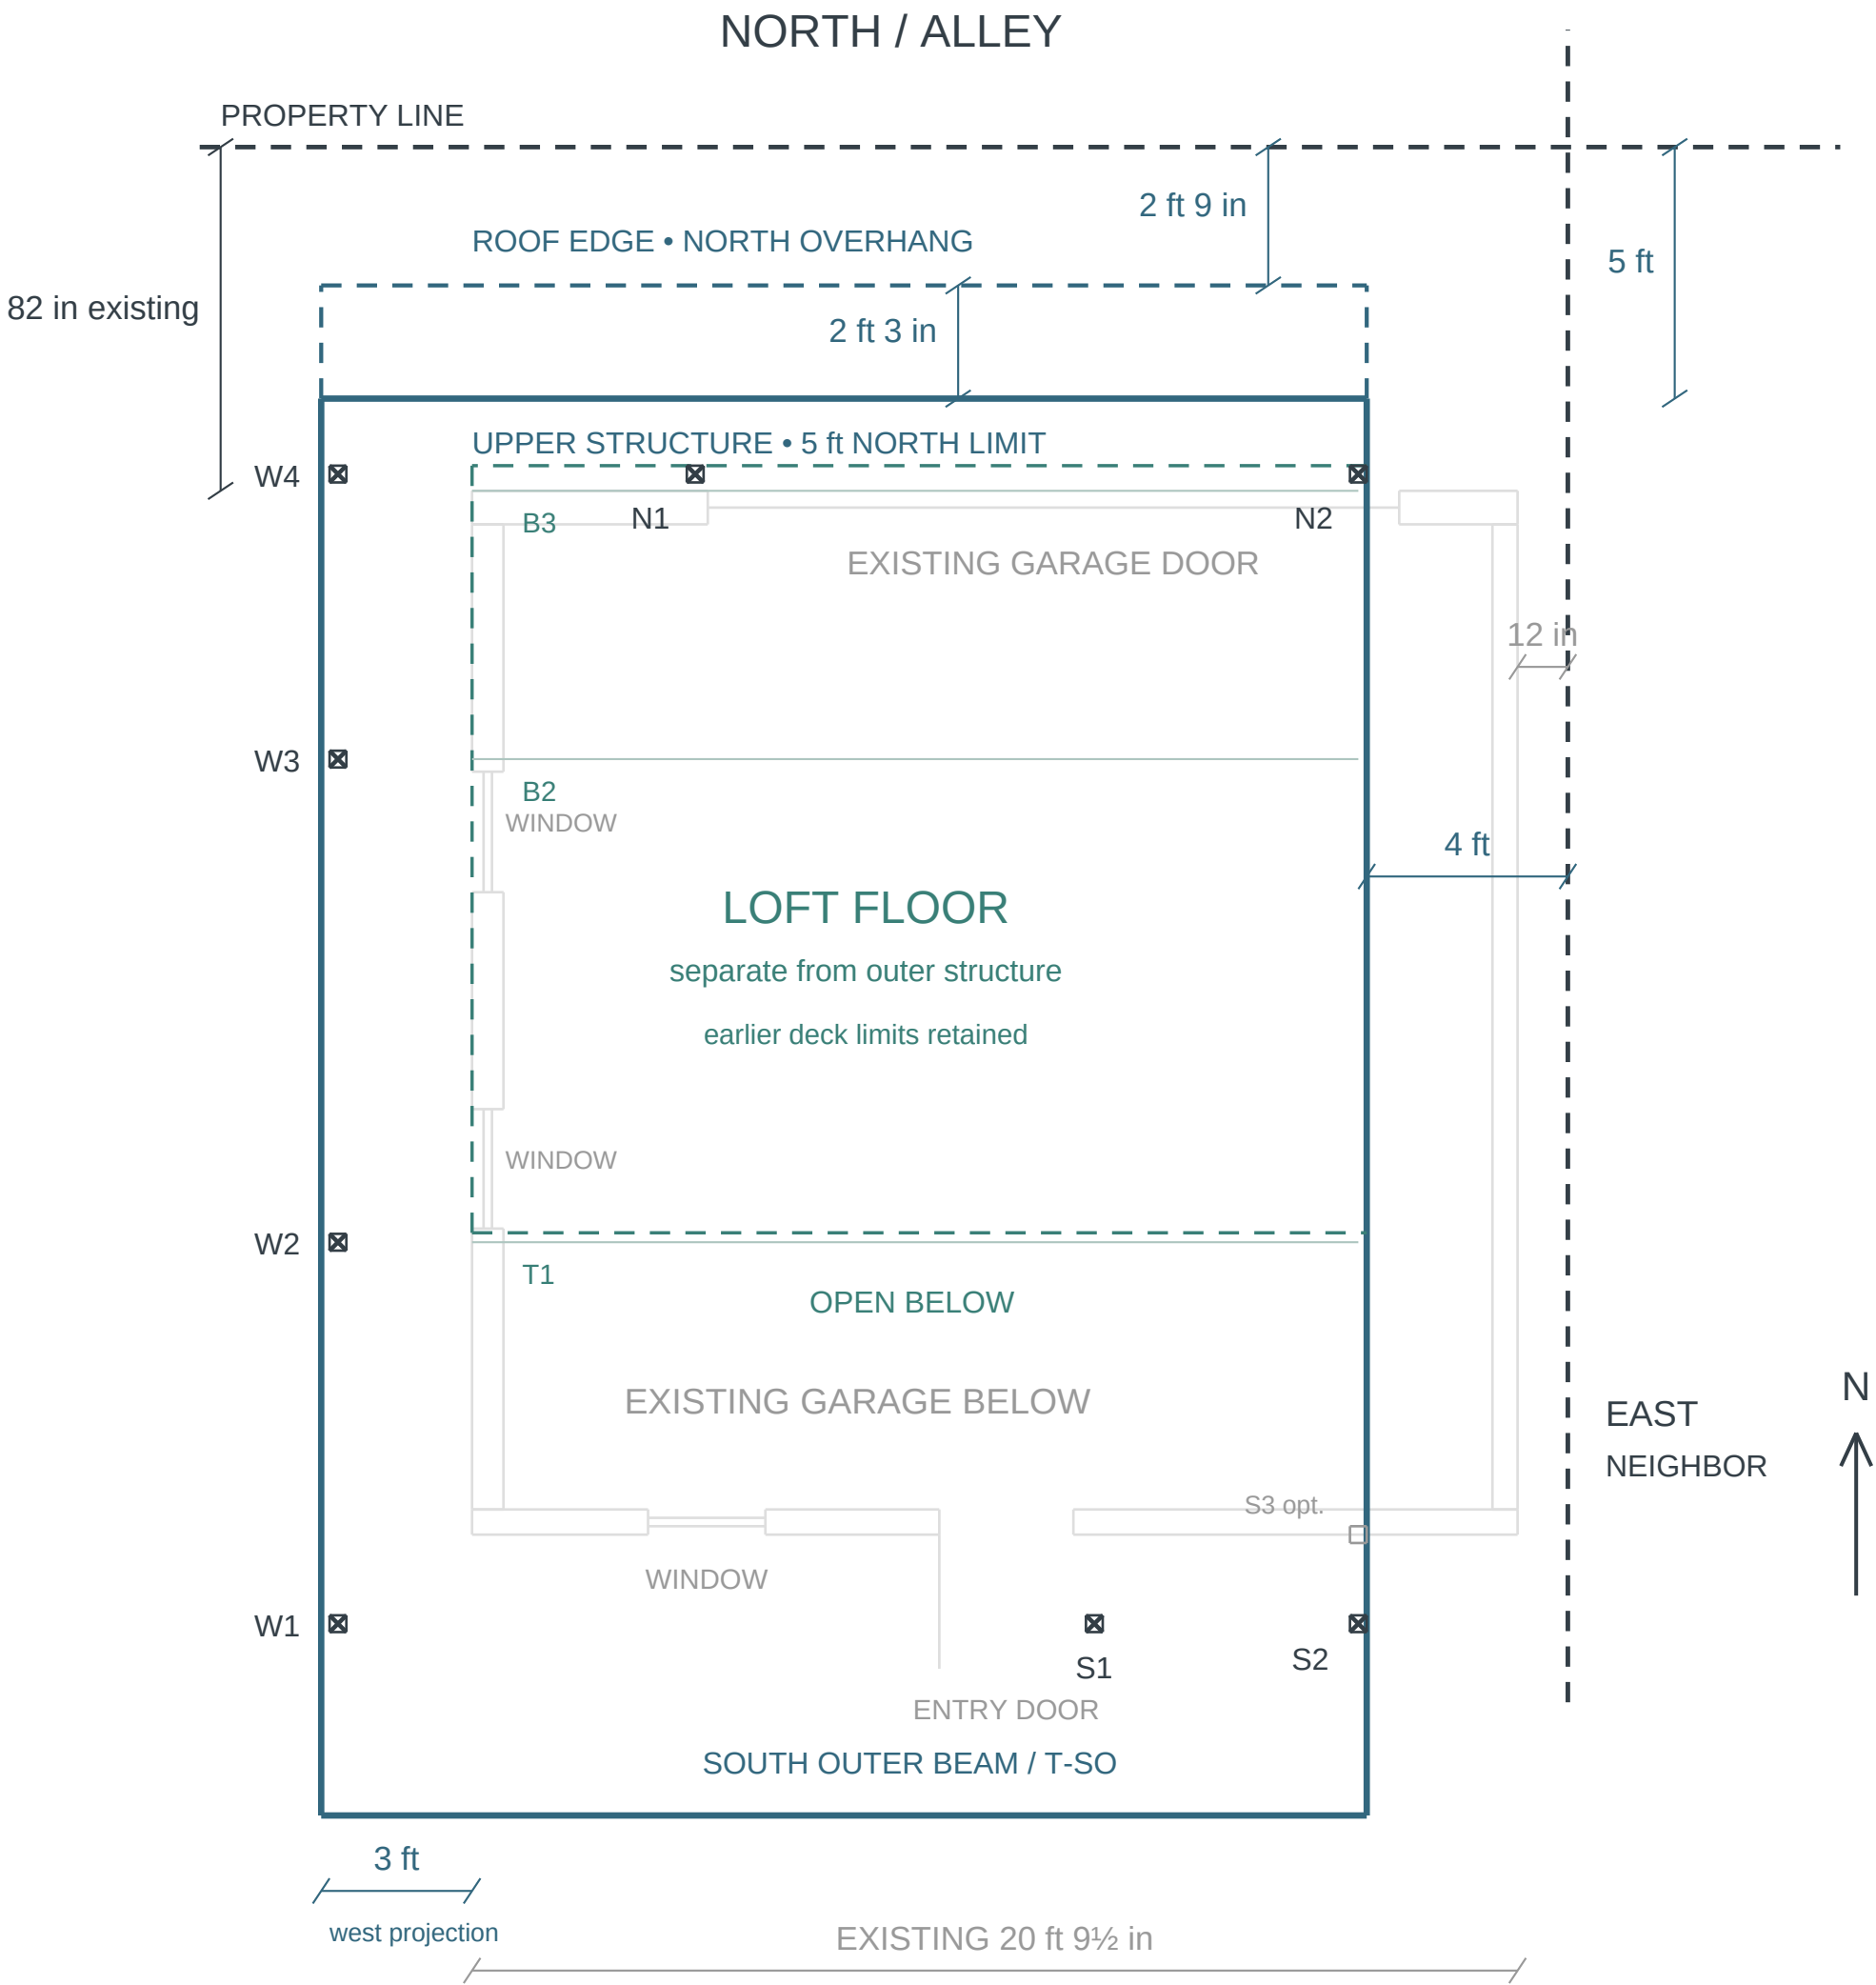

OUTLINES + SUPPORTS

Blue / full upper structure

West and south follow the outer beams.

East outside face: 4 ft from property line.

North outside face: 5 ft from property line.

Dashed blue: 2 ft 3 in north roof overhang.

Teal / loft floor

Separate, smaller deck from earlier model.

West edge over existing west wall.

South edge: 72 in north of south wall.

North edge: 255 in from south wall.

T1, B2 and B3 shown as framing references.

Columns / earlier plan

W1–W4, S1–S2 and N1–N2 retained.

S3 shown as optional in the source.

4-in square concept symbols from model.

East row moved inward to fit 4 ft limit.

Outer beam locations

West beam centerline: 32 in west of wall.

South beam centerline: 63 in south of wall.

Outline adds 4 in for earlier beam flange.

COORDINATION NOTES

East column centers shifted 12¾ in west.

North columns remain at original Y = 253 in.

New north face is 18 in beyond that row.

Beam connections and sizes remain to develop.

Sources: labeled framing plan / member register; earlier rendered model for beam widths, columns and loft deck.