
GARAGE / UPPER STRUCTURE + COLUMNS

04 Earlier floor-plan base • north up • dimensions in feet and inches

Discussion sketch | September 15, 2026

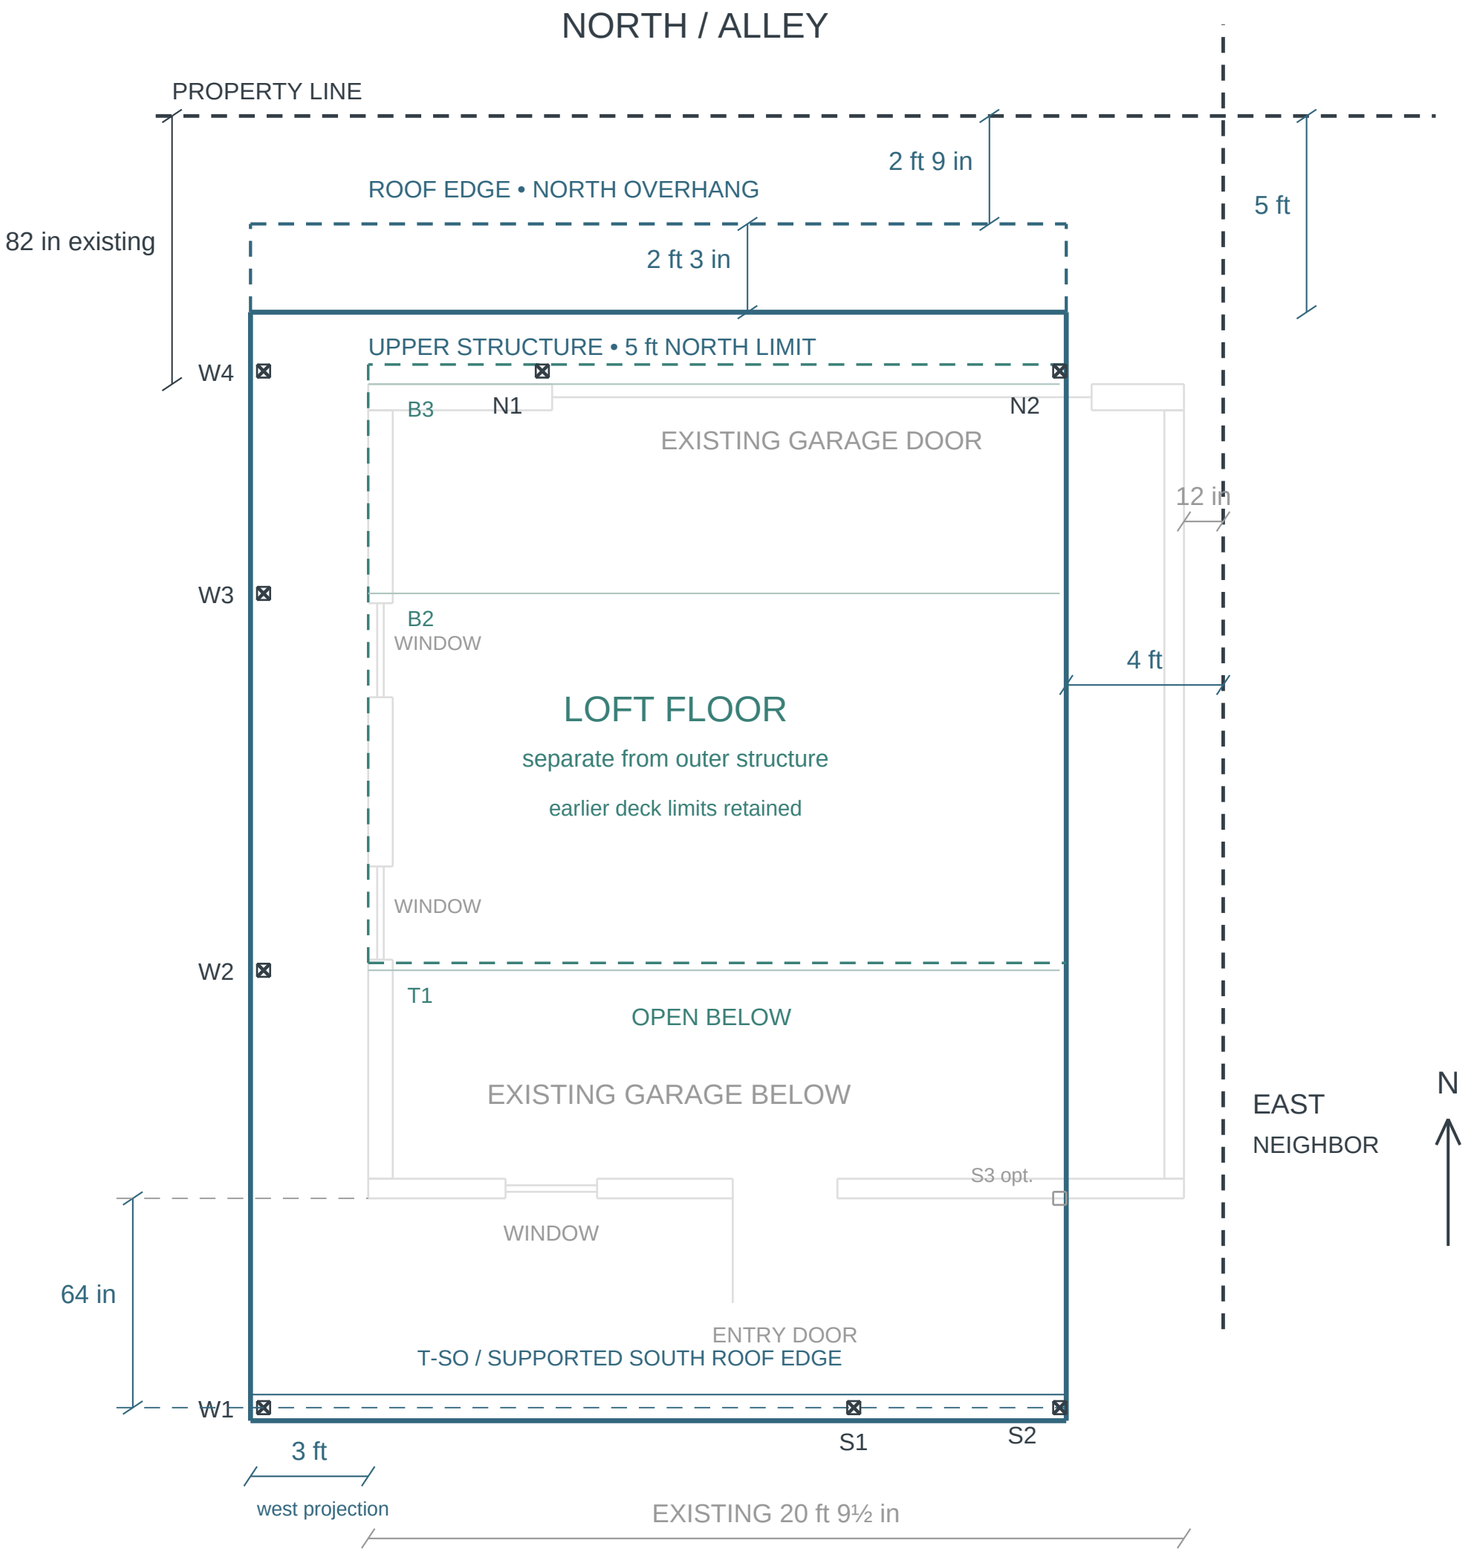

OUTLINES + SUPPORTS

Blue / full upper structure

West and south follow the outer beams.

East outside face: 4 ft from property line.

North outside face: 5 ft from property line.

Dashed blue: 2 ft 3 in north roof overhang.

Teal / loft floor

Separate, smaller deck from earlier model.

West edge over existing west wall.

South edge: 72 in north of south wall.

North edge: 255 in from south wall.

T1, B2 and B3 shown as framing references.

Columns / revised south row

W1, S1, S2 centers: 64 in south of wall.

S3 shown as optional in the source.

4-in square concept symbols from model.

East row moved inward to fit 4 ft limit.

Outer beam locations

West beam centerline: 32 in west of wall.

South beam centered over W1, S1 and S2.

Roof edge at beam outside face (assumed).

COORDINATION NOTES

East column centers shifted 12¾ in west.

North columns remain at original Y = 253 in.

New north face is 18 in beyond that row.

South beam width: 8 in provisional; edge 68 in.

Sources: labeled framing plan / member register; earlier rendered model for beam widths, columns and loft deck.

0 ft 2 ft 4 ft 6 ft

Local boundary segments only • no surveyed bearings • layout study using requested setbacks, not a code determination.