


GARAGE / UPPER STRUCTURE + COLUMNS

07 Earlier floor-plan base • north up • dimensions in feet and inches

Discussion sketch | September 15, 2026

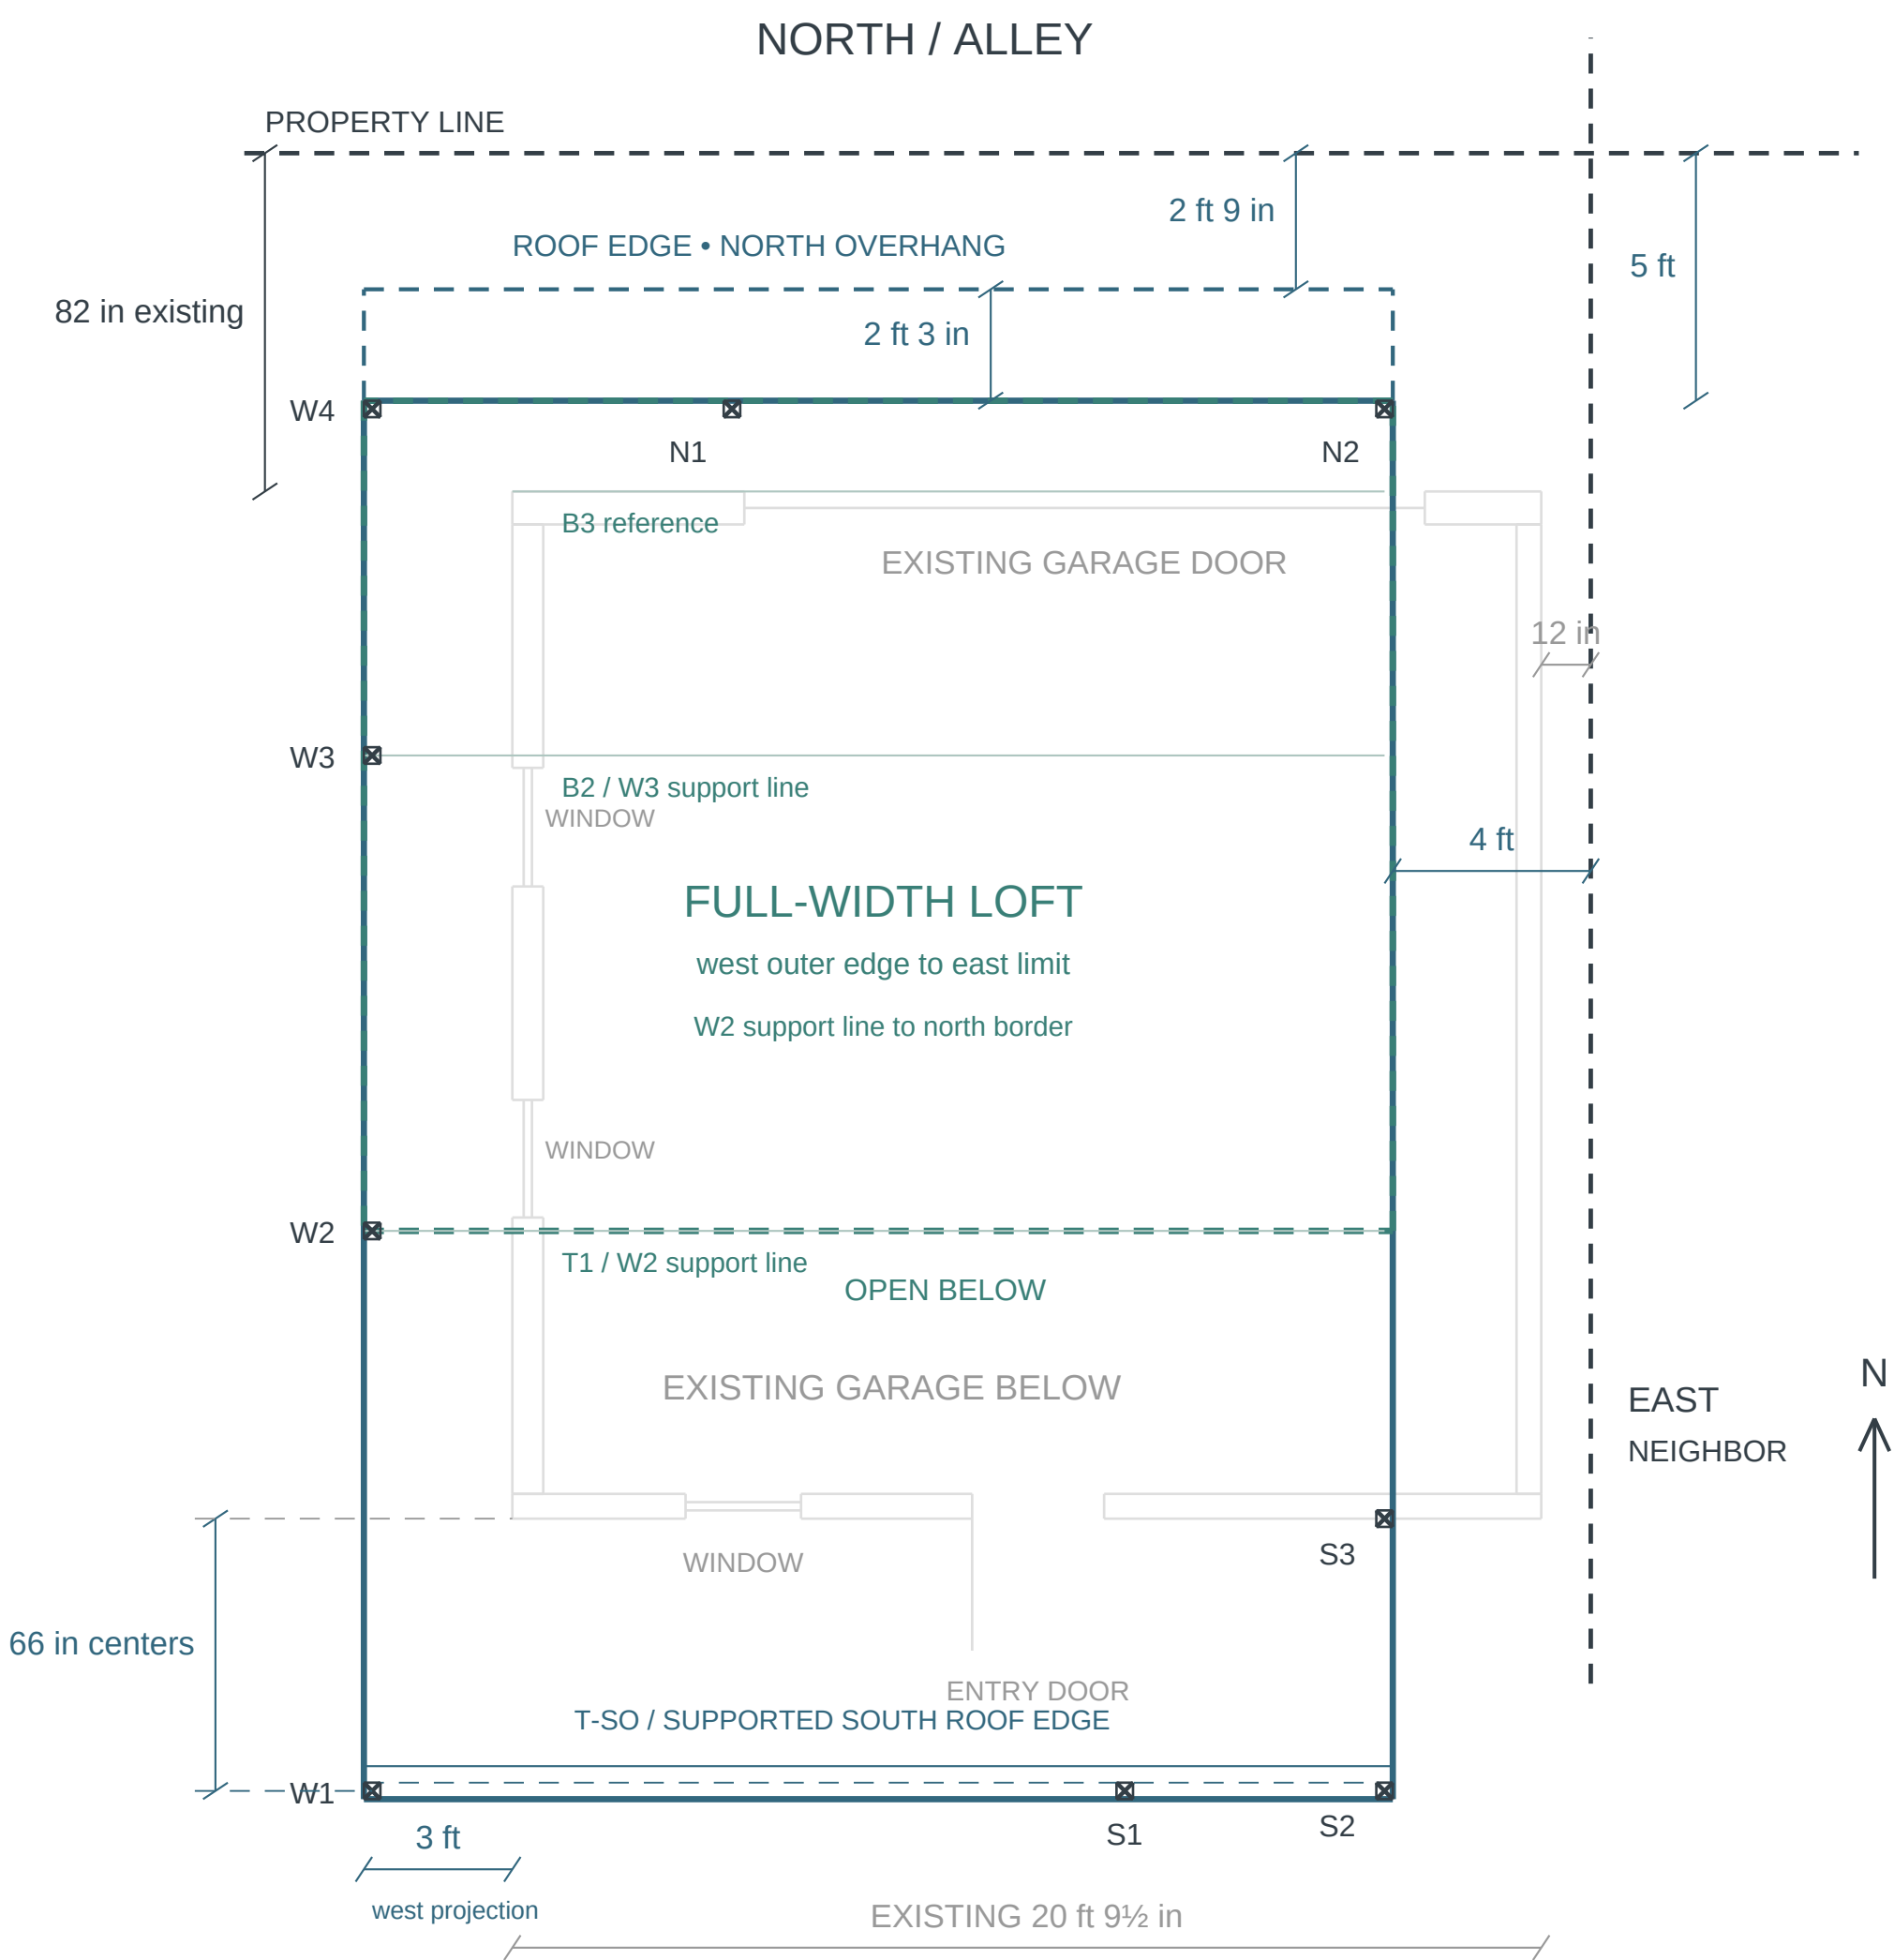

OUTLINES + SUPPORTS

Blue / full upper structure

West and south follow the outer beams.

East outside face: 4 ft from property line.

North outside face: 5 ft from property line.

Dashed blue: 2 ft 3 in north roof overhang.

Teal / loft floor

Expanded to the full available width.

West, east and north edges meet blue outline.

South edge follows W2 at Y = 69¾ in.

Supported along the west by W2, W3, W4.

Teal dashes overlay shared blue boundaries.

Columns / flush outside edges

W1 sits flush in the southwest corner.

S1 and S2 south faces meet the blue edge.

S2 east face also meets the blue edge.

S3 restored as a required column.

Outer beam locations

West beam centerline: 32 in west of wall.

South beam supported by W1, S1 and S2.

Roof edge at beam outside face (assumed).

COORDINATION NOTES

Blue outline retained; column symbols are 4 in.

W1/S1/S2 centers: 66 in south; faces at 68 in.

W1–W4 west faces meet the blue outline.

North column faces remain flush with 5-ft limit.

Sources: labeled framing plan / member register; earlier model for member widths; loft and north supports revised to your instructions.