


GARAGE · SECTION + FRAMING PLAN


Matching member names · all beam and truss bottoms at 8' 2½" · columns carry the loads

01 WEST SECTION — LOOKING EAST

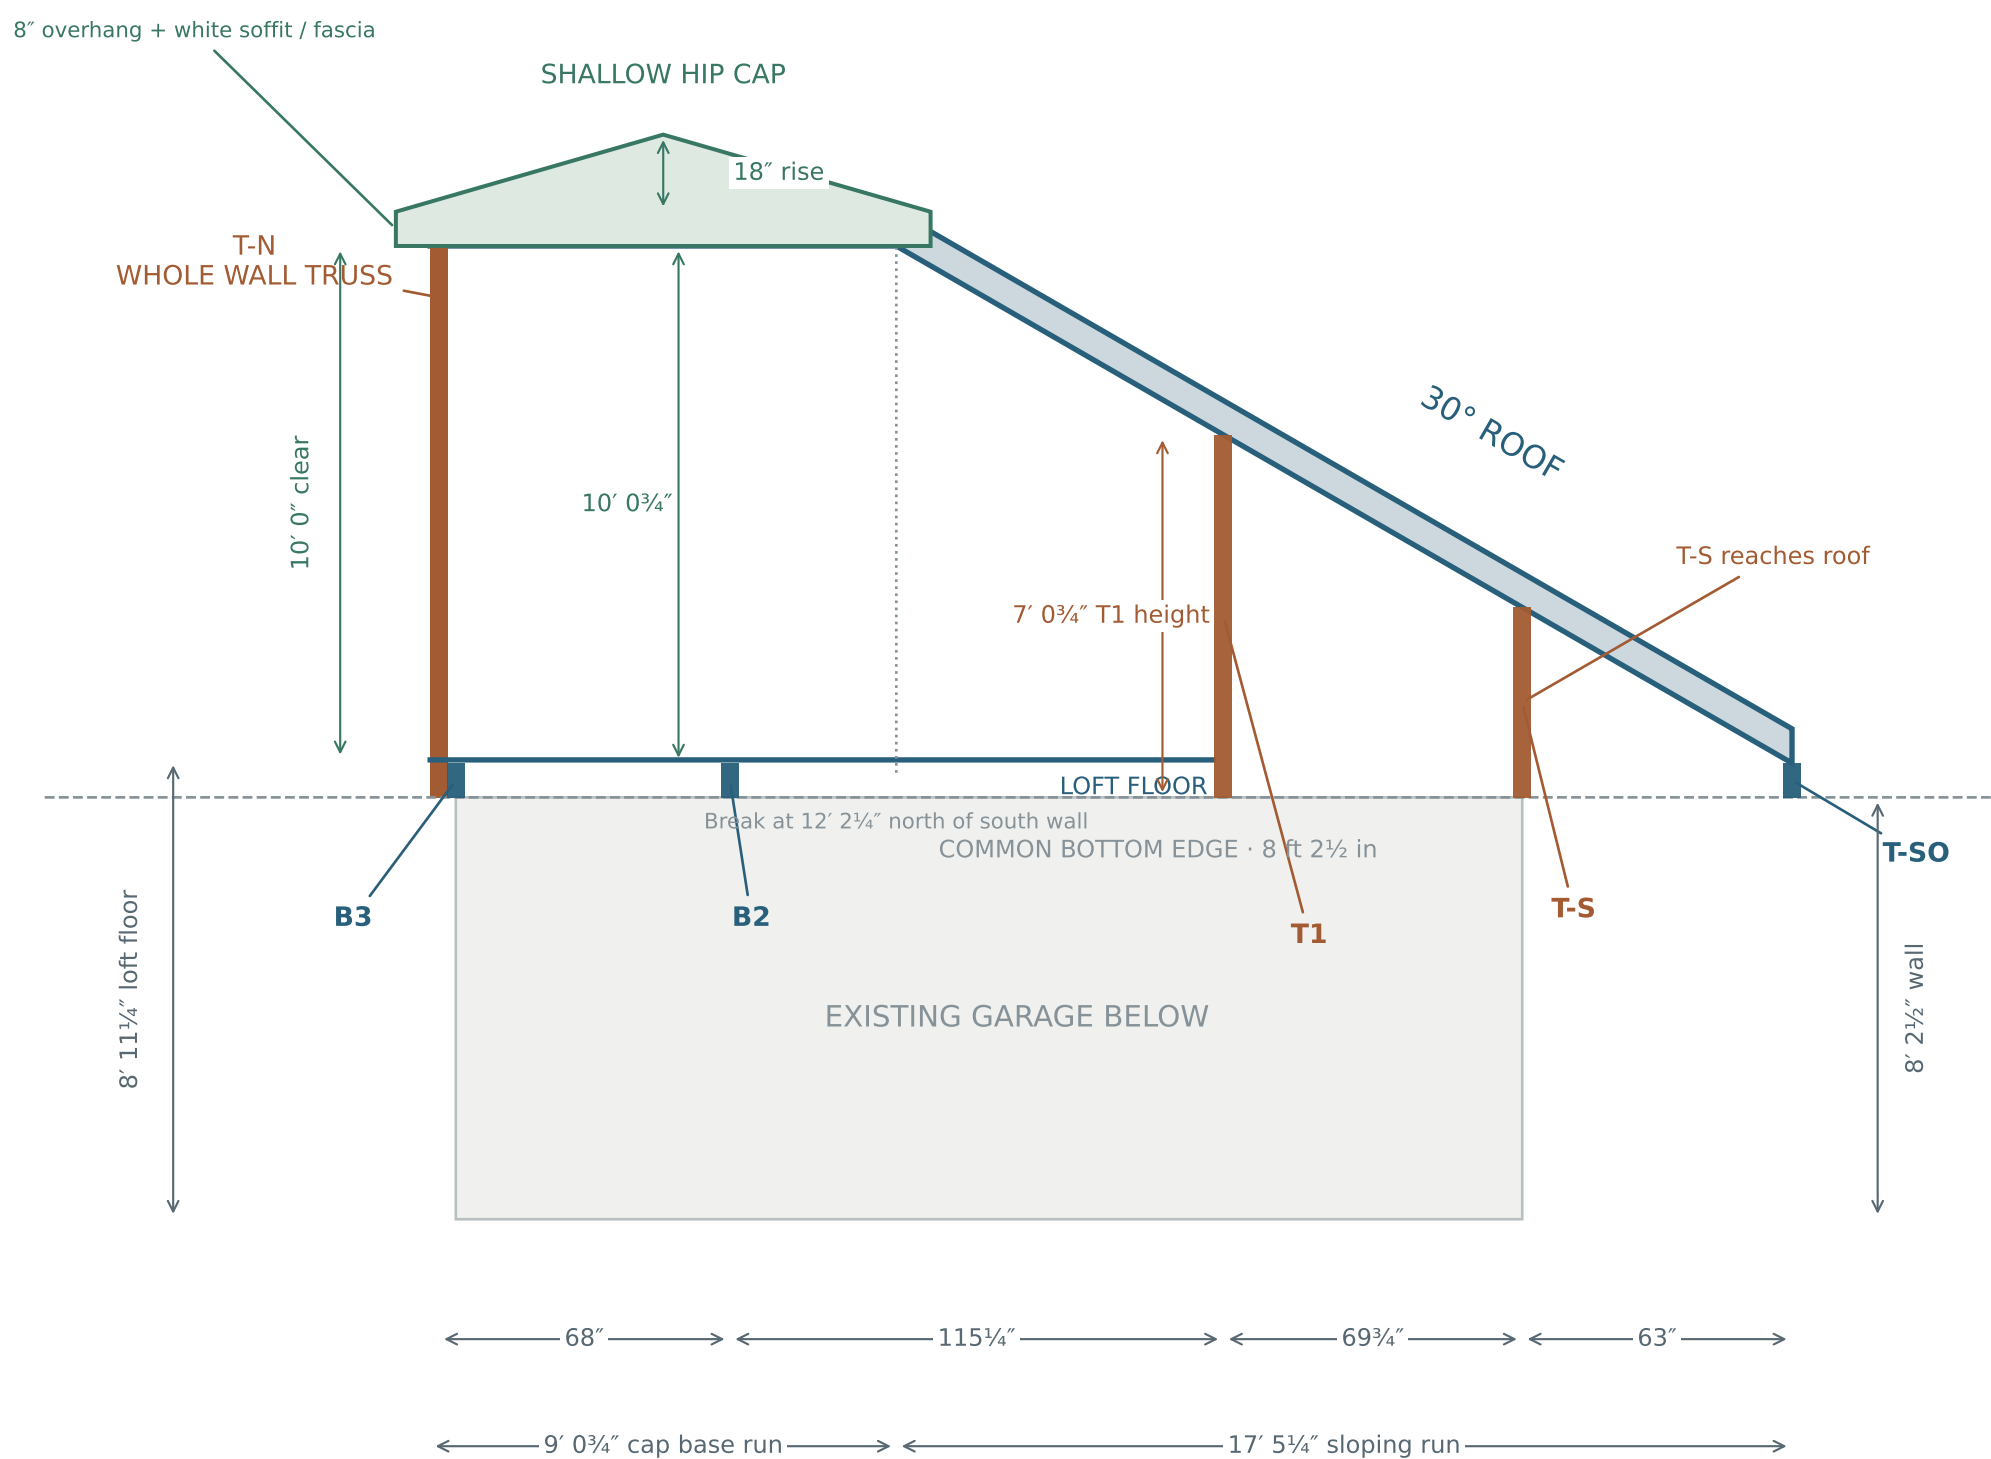

02 TOP-DOWN FRAMING PLAN — NORTH UP

Orange = truss Blue = beam Green dashed = hip cap outline / hips. T-SO is a BEAM.

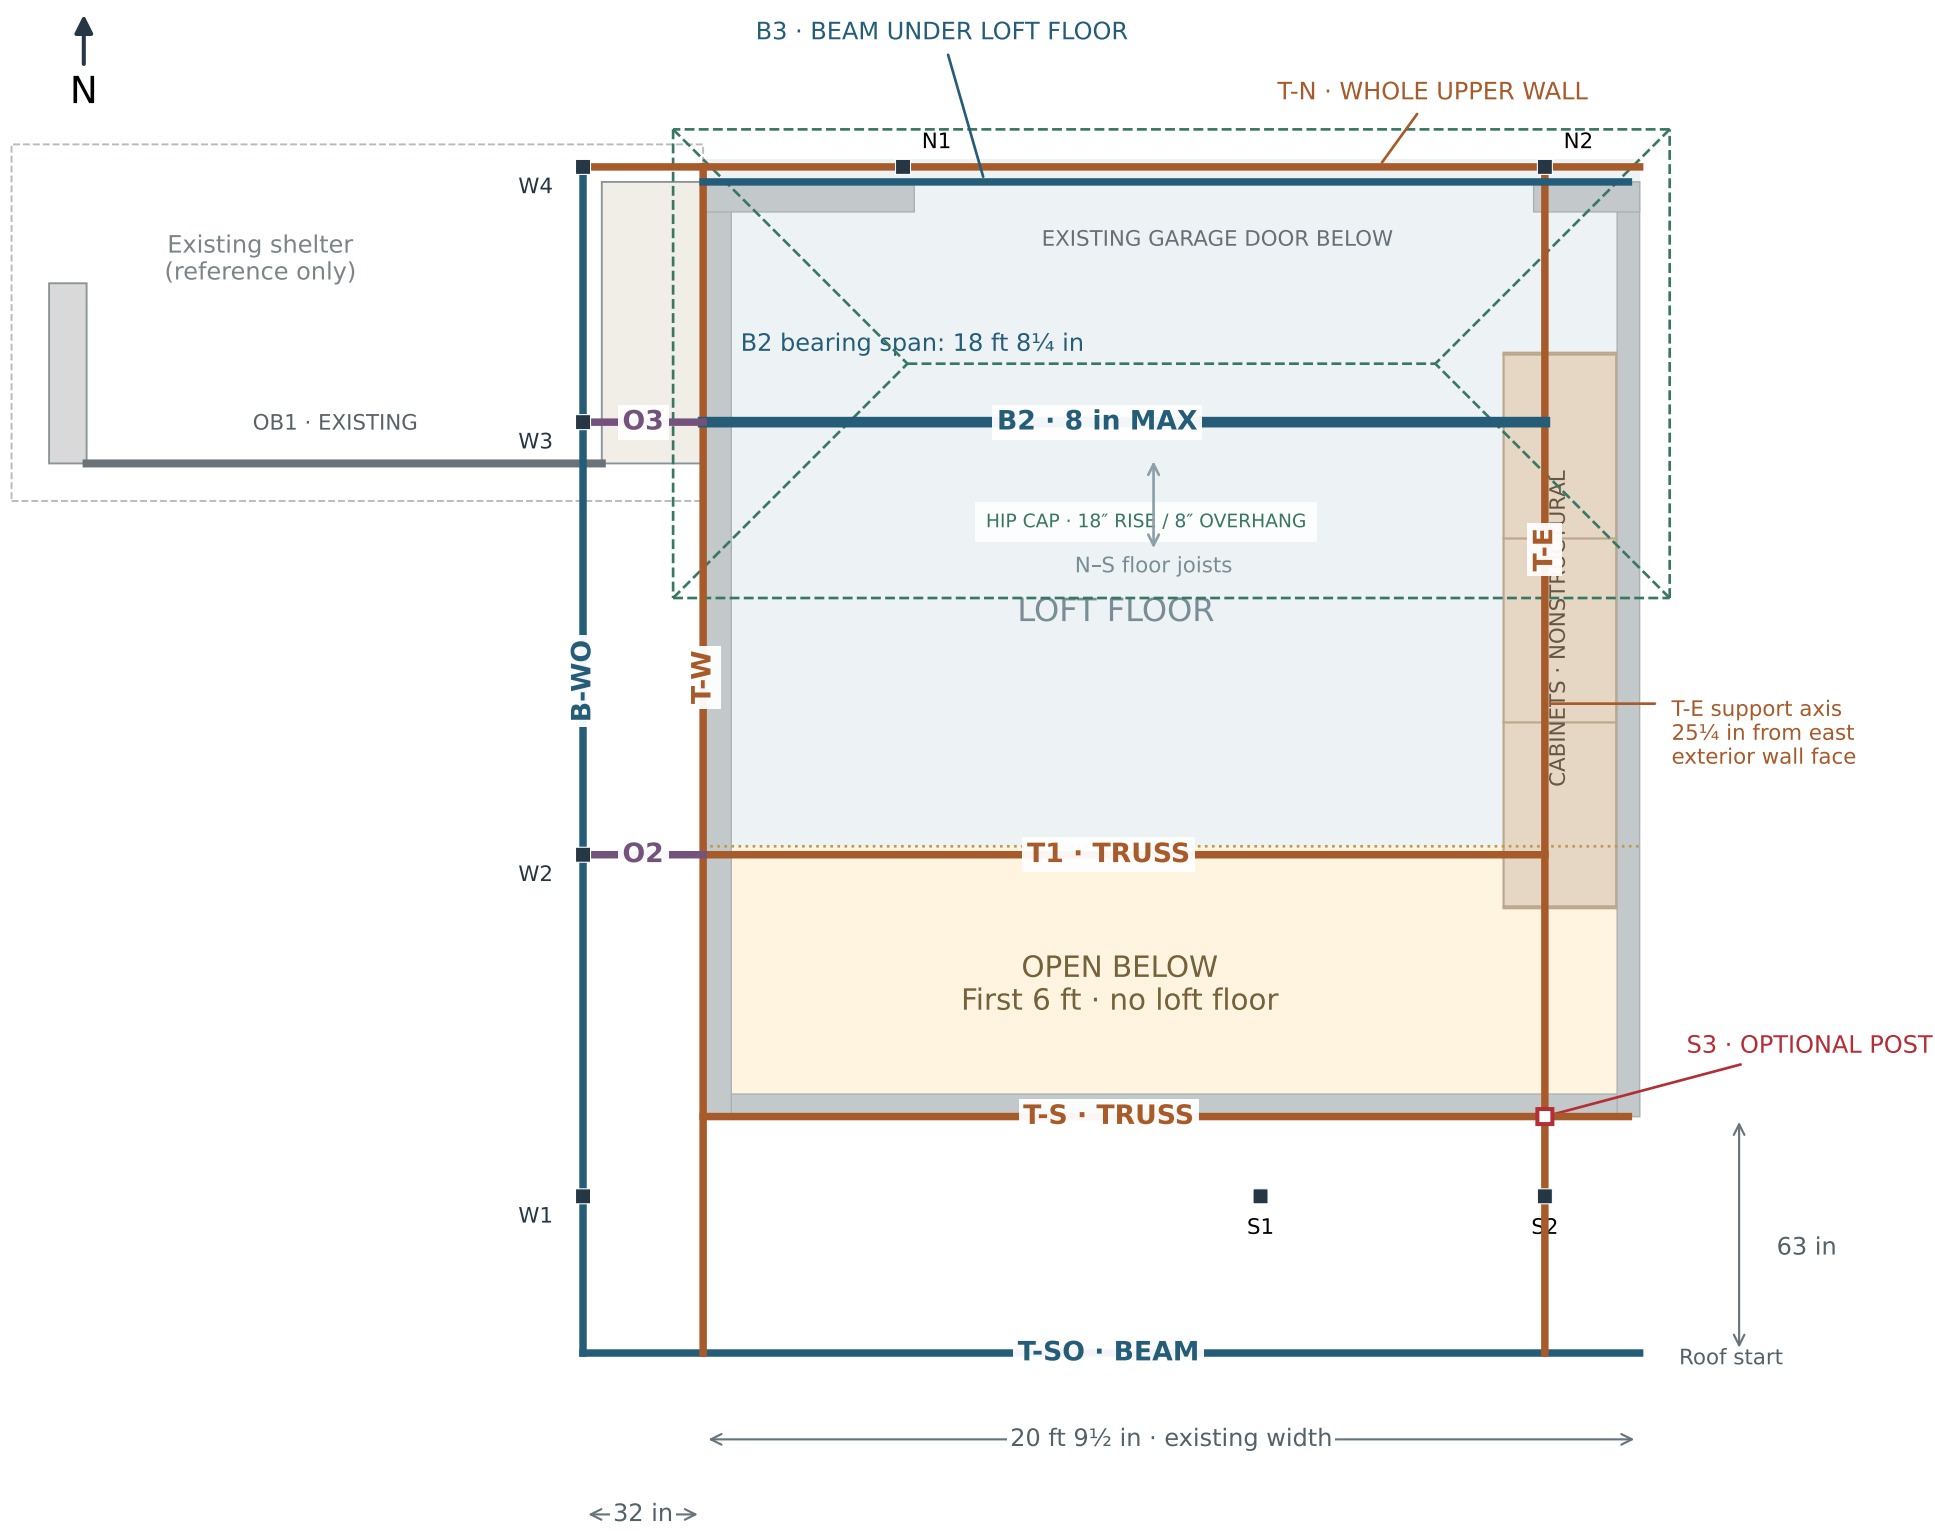

MEMBER REGISTER

T-S	Wall-top datum truss · reaches roof
T-E	East truss · aligned S2 / S3 / N2
T-W	West wall truss
B3	North wall BEAM · under loft floor
T-SO	Southernmost BEAM · common datum
T1	Truss · wall-top datum to roof
B2	Main loft beam · 8 in max depth
T-N	North wall truss · includes loft door
B-WO	West outer longitudinal beam
O2 / O3	Transfers from west wall to outer posts
OB1	Existing shelter front beam

DRAWING BASIS

- S2 moved east 12¼ in to align with N2.
- Gray = existing walls; brown fill = cabinets.
- Hollow red S3 = optional 4-inch post.
- Solid orange = truss; B-S removed.
- Truss depth is vertical, not plan width.
- All bottoms = wall top; columns carry loads.

T1 replaces B1 and reaches the roof. T-N is the whole north upper-wall truss. B3 is the north beam below the loft floor. B-S is removed.

Roof: 30° from T-SO, then 18-in hip cap with 8-in overhang / fascia. Rear ceiling remains 10 ft above trial loft floor.

T-W / T-E / B-WO are outside the interior section cut and appear in plan. South support-row / T-SO connections remain unresolved; sizes are conceptual.