


T1 · TRUSS ELEVATION

West → east · dimensions along the framing line · member layout projected directly from the current 3D model

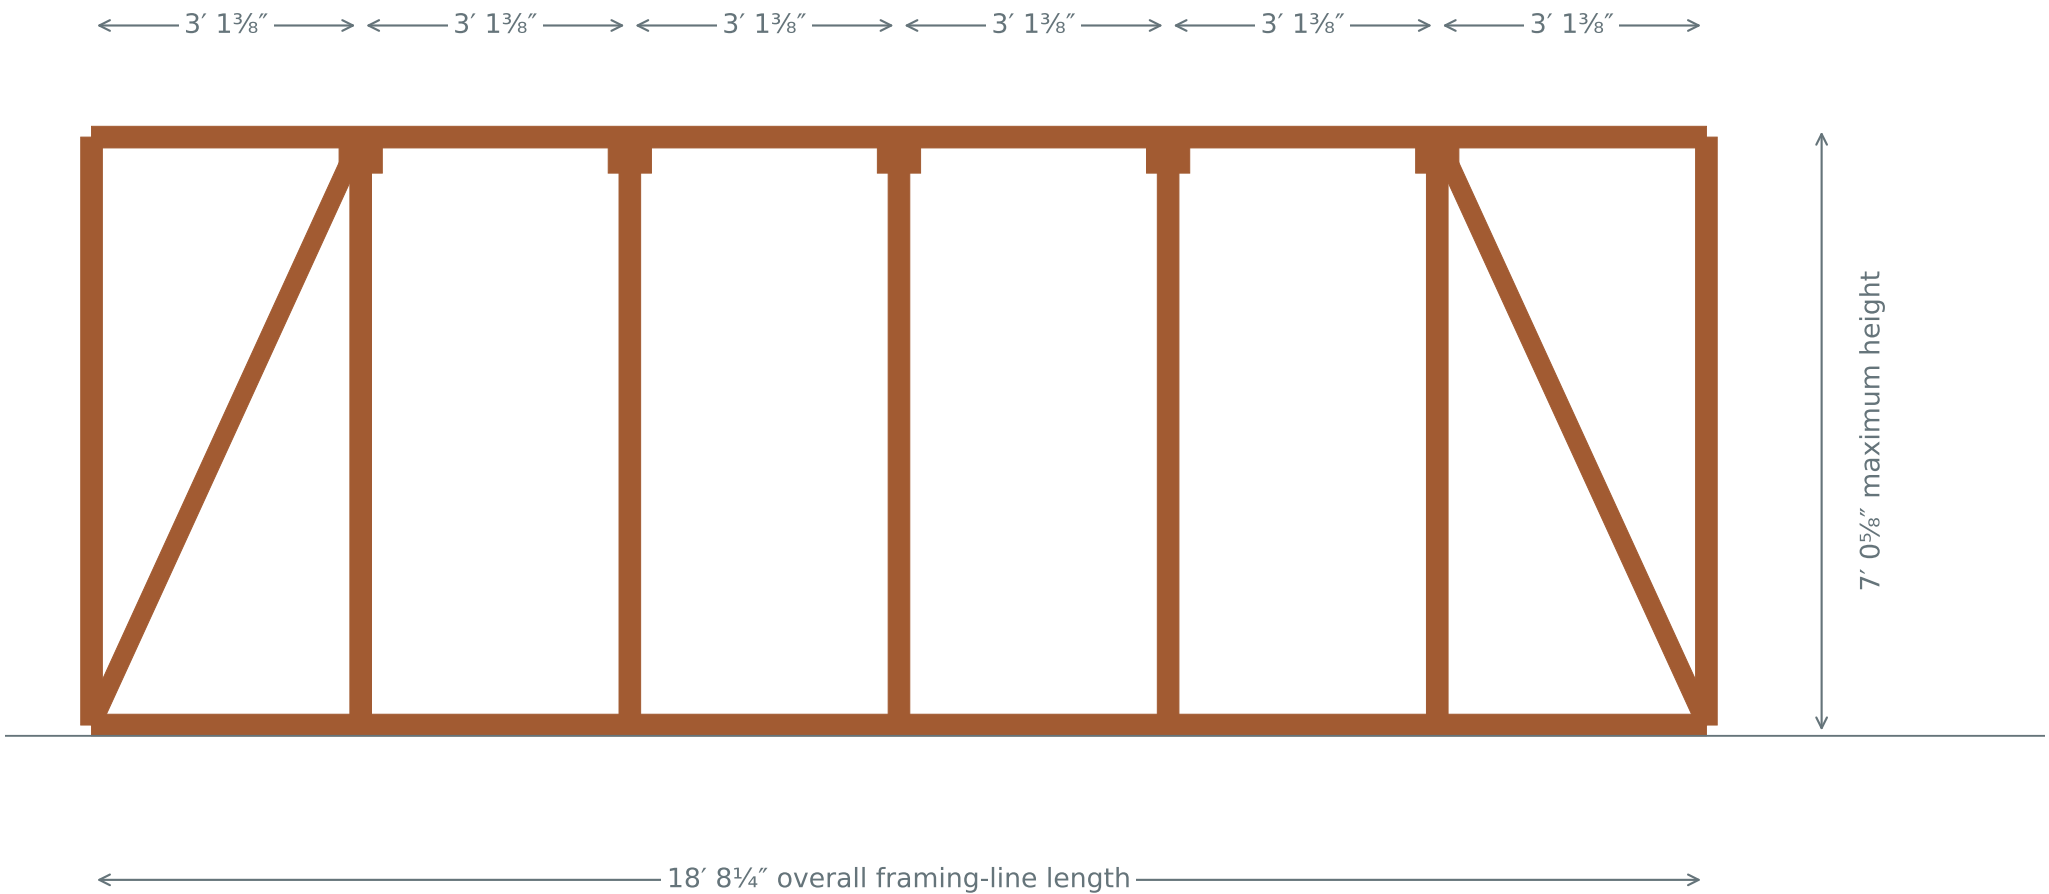

COMMON BOTTOM = 8' 2 1/2" ABOVE GROUND · COLUMN-SUPPORTED

Six equal panel bays; dimensions are centerline spacing, not clear openings.
Model layout: verticals throughout; diagonals in the two end bays; central storage bays open.
At station 69 3/4" north of south wall.
End-braced rectangles require engineered moment joints / Vierendeel action; web layout is illustrative.

Concept geometry, not fabrication drawings. Member sizes, joints, bracing and bearing details require design.
The shallow hip roof cap sits above the rear ceiling datum; its internal framing has not been laid out.