


T-W · TRUSS ELEVATION

South → north · station zero = south exterior garage wall · member layout projected directly from the current 3D model

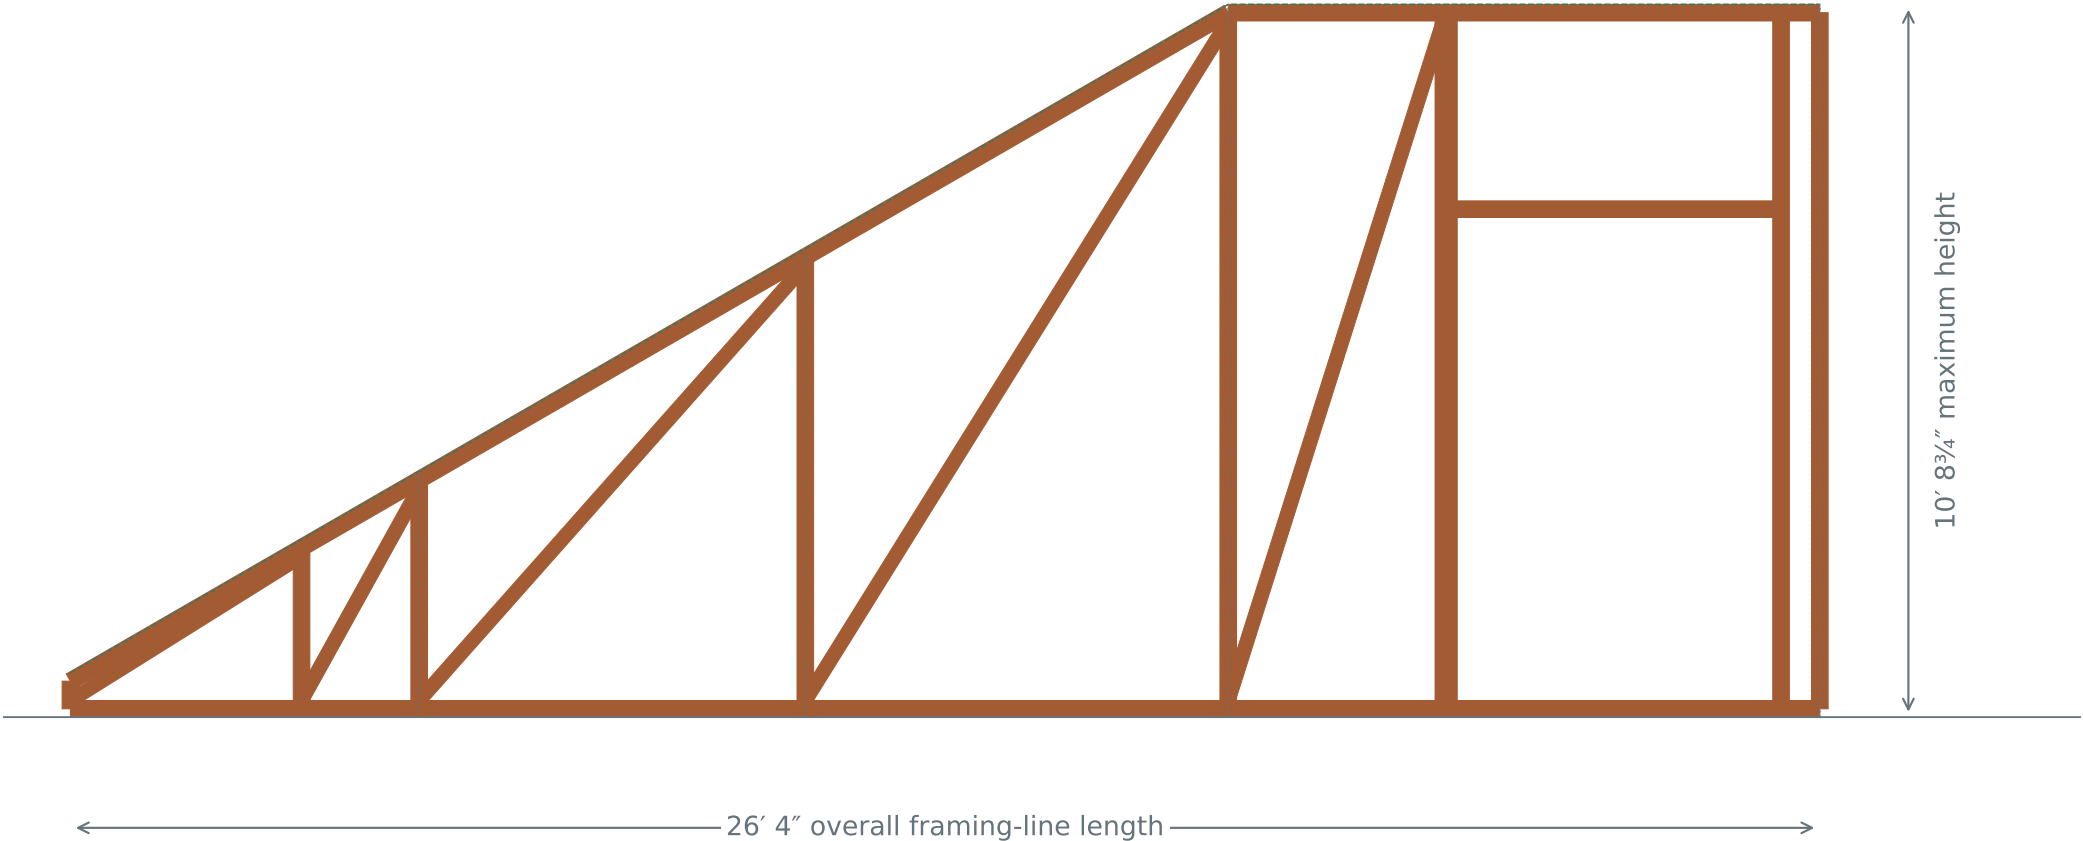

COMMON BOTTOM = 8' 2½" ABOVE GROUND · COLUMN-SUPPORTED

UPRIGHT STATIONS FROM SOUTH WALL (in): -63, -21.25, 0, 69.75, 146.15, 185, 186, 246, 253

PANEL SPACINGS (in): 41.75, 21.25, 69.75, 76.4, 38.85, 1, 60, 7

DEPTHS: south tip 8"; south wall 3' 8⅜"; at T1 7' 0⅝"; plateau 10' 8¾".

West door header is included. Closely spaced uprights at 185 / 186 in are retained from the model; opening framing needs coordination.

Concept geometry, not fabrication drawings. Member sizes, joints, bracing and bearing details require design.

The shallow hip roof cap sits above the rear ceiling datum; its internal framing has not been laid out.