


T-S · TRUSS ELEVATION

West → east · dimensions along the framing line · member layout projected directly from the current 3D model

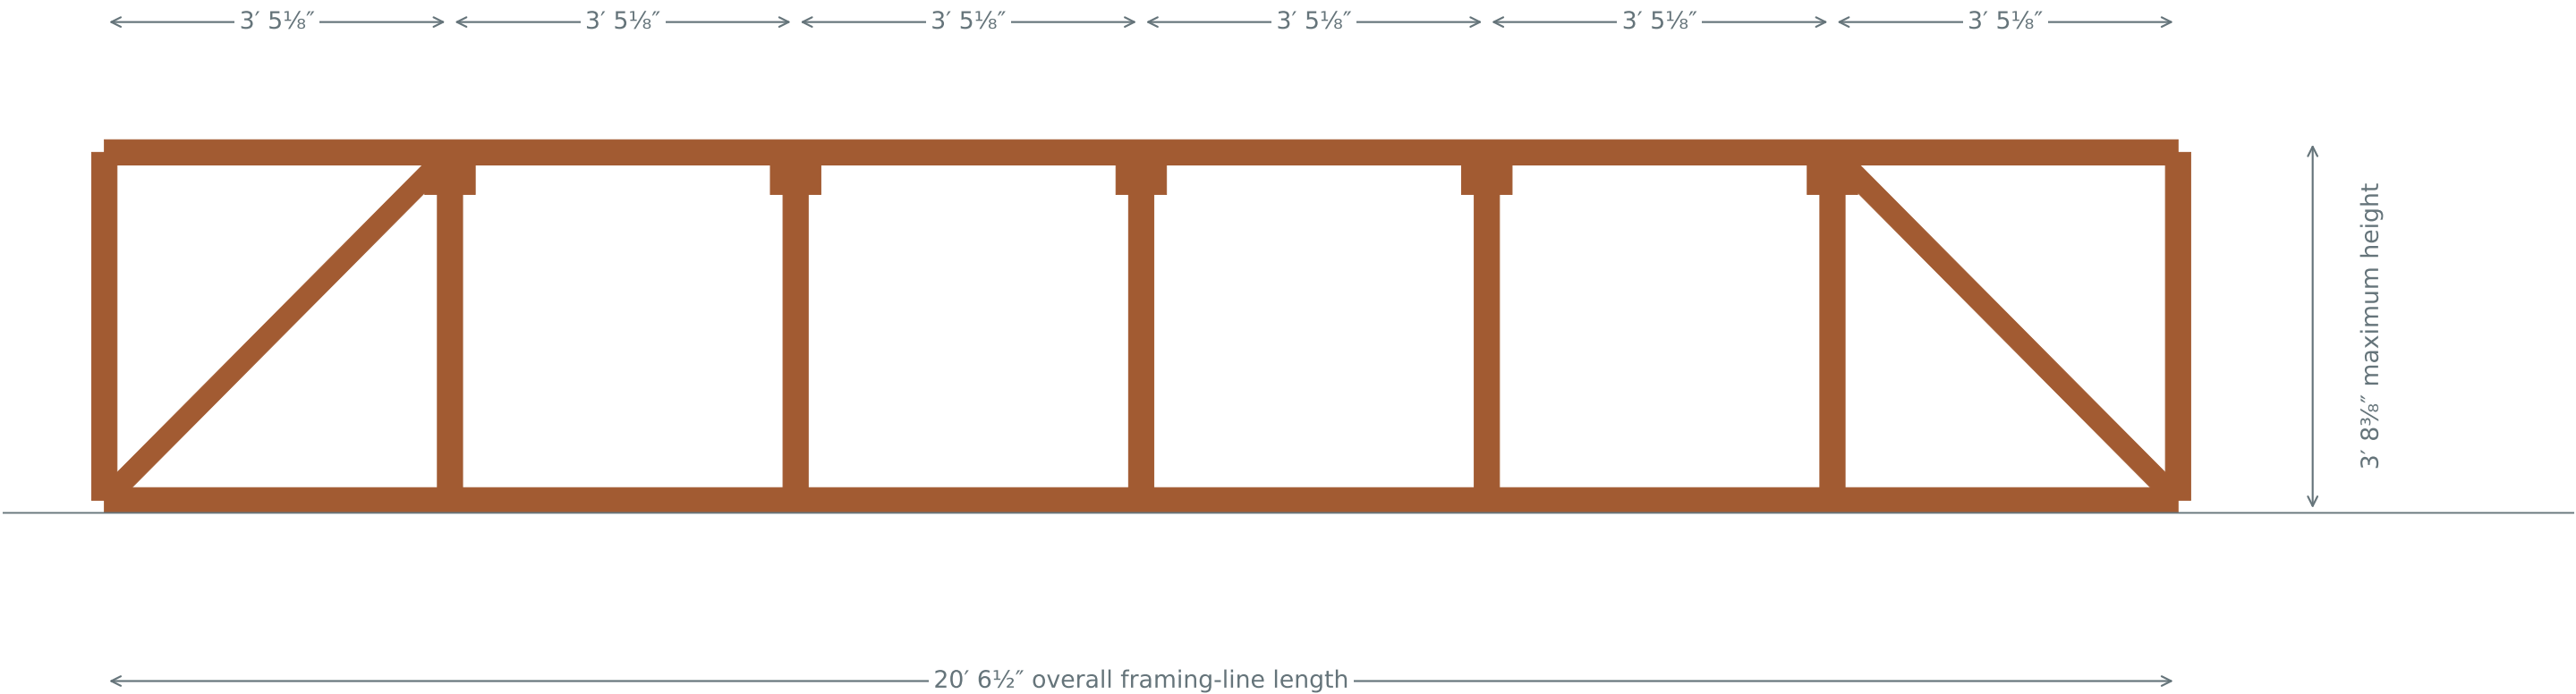


COMMON BOTTOM = 8' 2½" ABOVE GROUND · COLUMN-SUPPORTED

Six equal panel bays; dimensions are centerline spacing, not clear openings.
Model layout: verticals throughout; diagonals in the two end bays; central storage bays open.
At station 0" (south wall).
End-braced rectangles require engineered moment joints / Vierendeel action; web layout is illustrative.

Concept geometry, not fabrication drawings. Member sizes, joints, bracing and bearing details require design.
The shallow hip roof cap sits above the rear ceiling datum; its internal framing has not been laid out.

T1 · TRUSS ELEVATION

West → east · dimensions along the framing line · member layout projected directly from the current 3D model

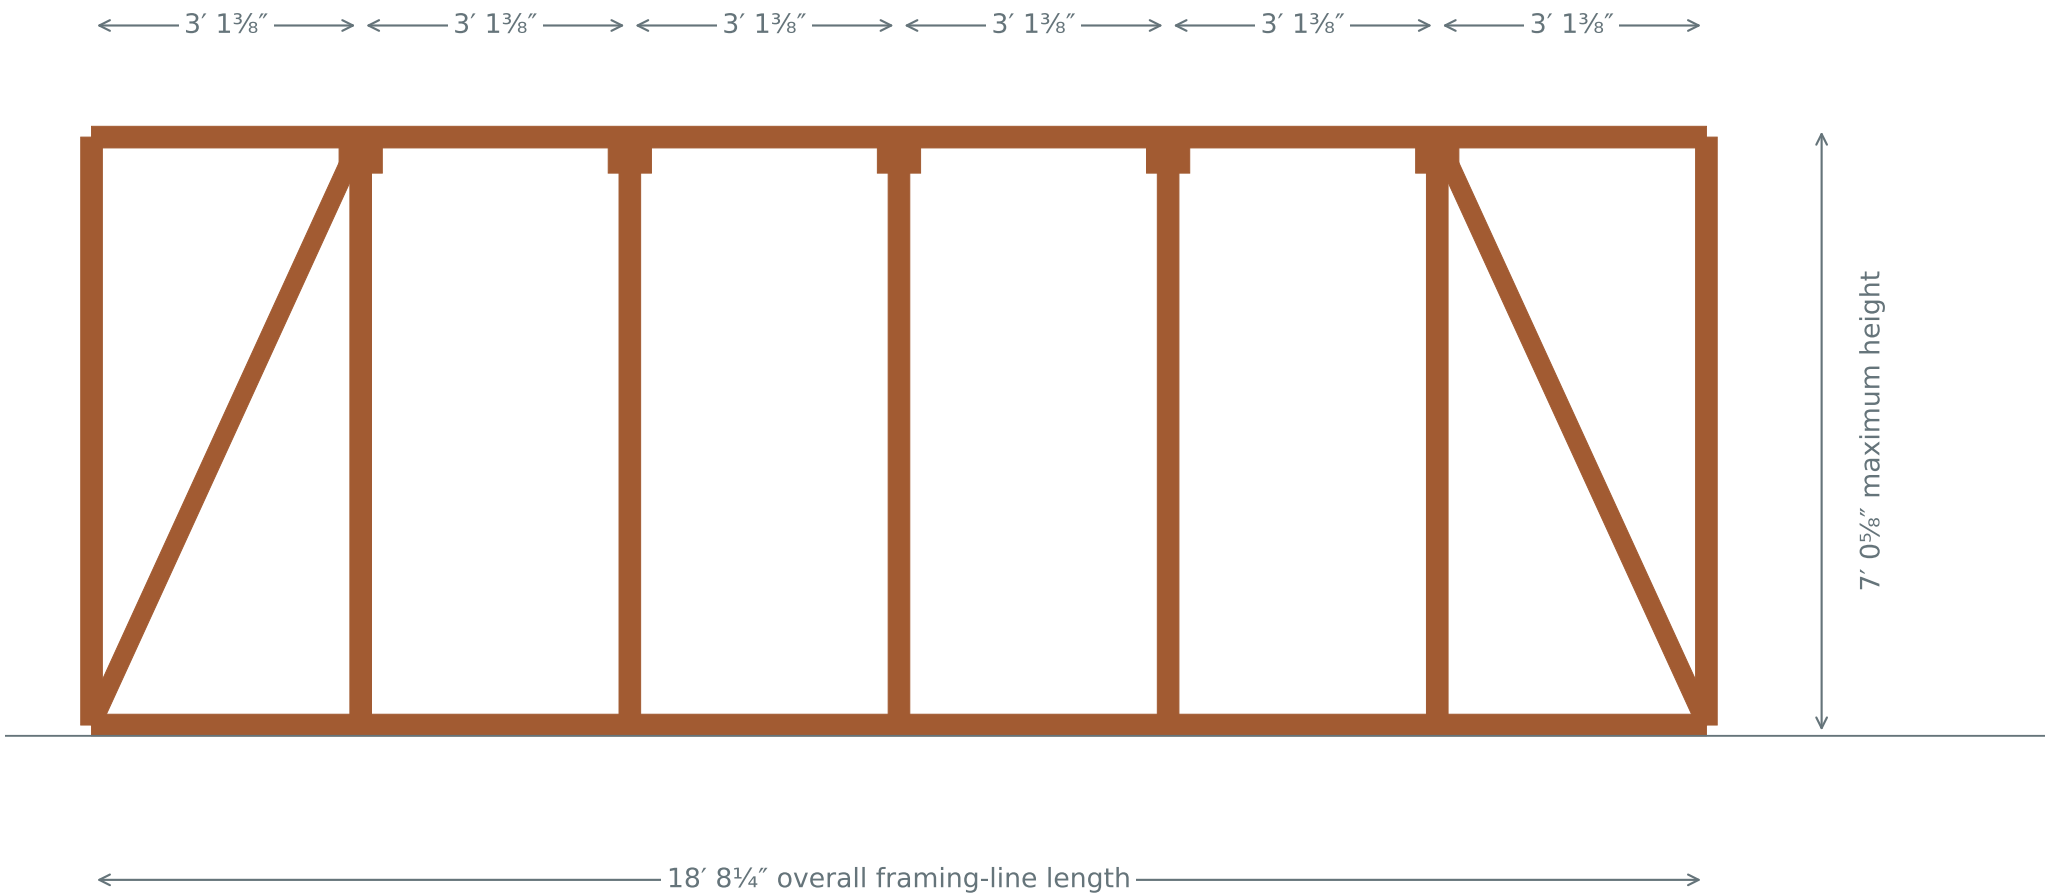


COMMON BOTTOM = 8' 2 1/2" ABOVE GROUND · COLUMN-SUPPORTED

Six equal panel bays; dimensions are centerline spacing, not clear openings.
Model layout: verticals throughout; diagonals in the two end bays; central storage bays open.
At station 69 3/4" north of south wall.
End-braced rectangles require engineered moment joints / Vierendeel action; web layout is illustrative.

Concept geometry, not fabrication drawings. Member sizes, joints, bracing and bearing details require design.
The shallow hip roof cap sits above the rear ceiling datum; its internal framing has not been laid out.

T-W · TRUSS ELEVATION

South → north · station zero = south exterior garage wall · member layout projected directly from the current 3D model

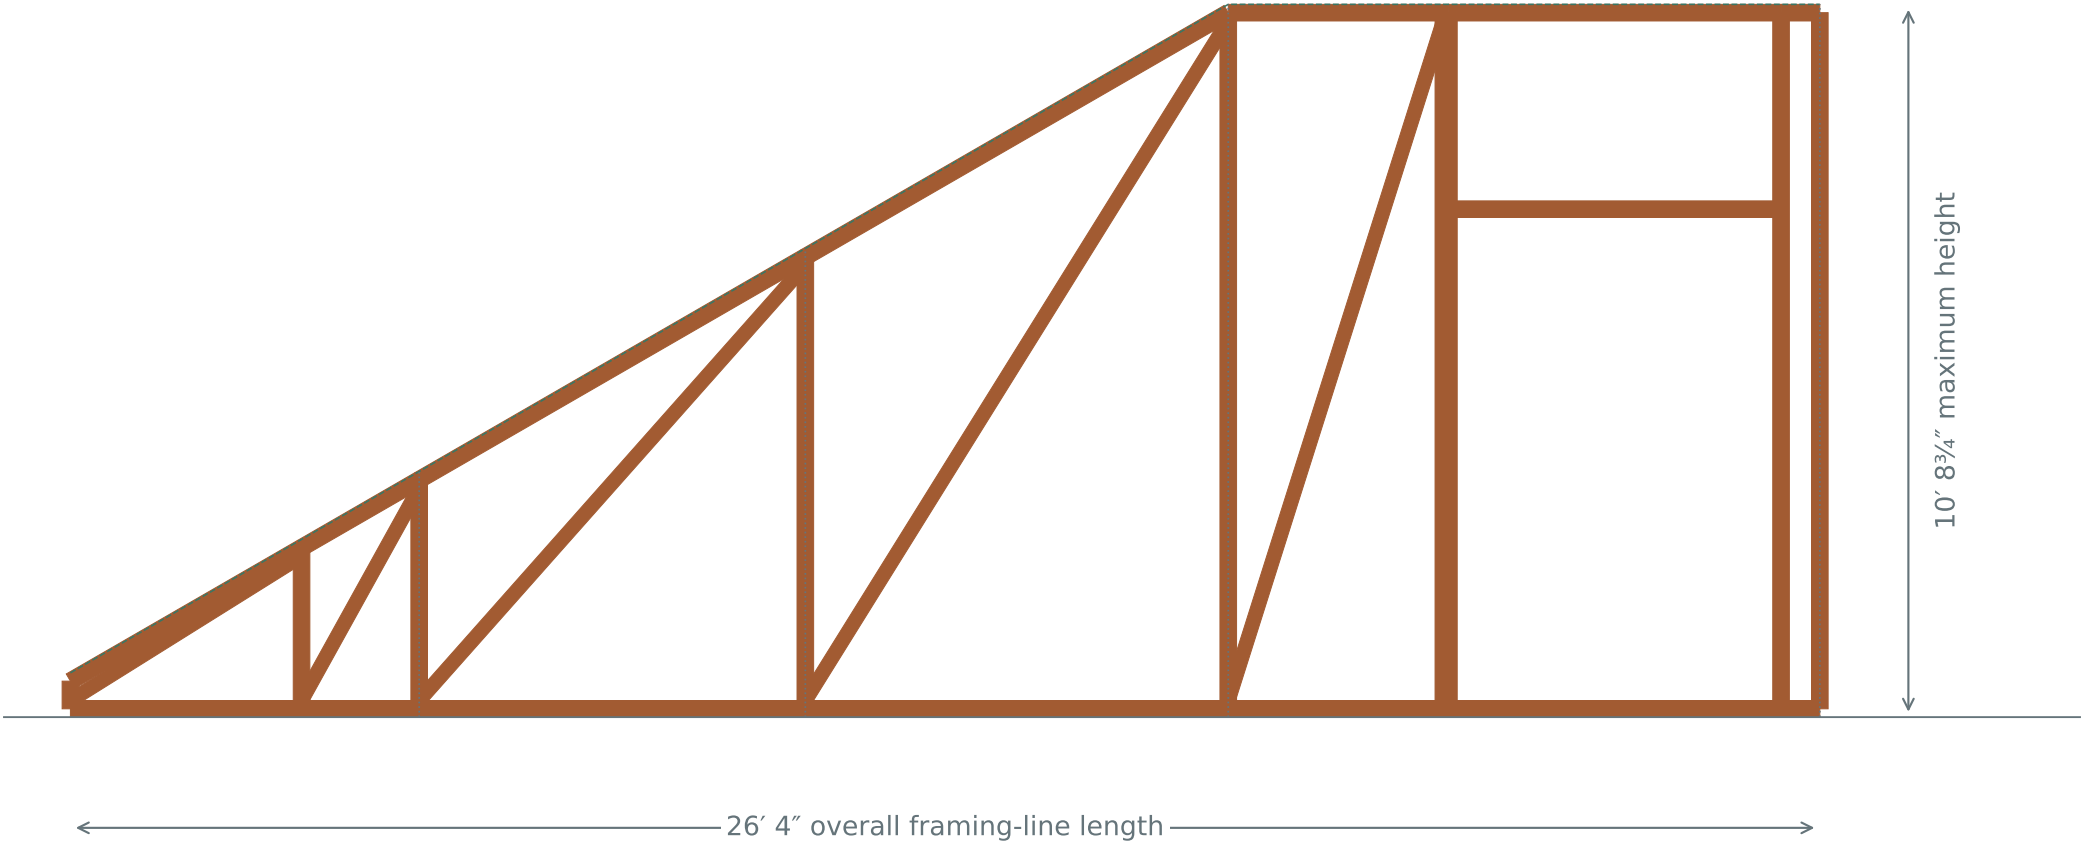

COMMON BOTTOM = 8' 2½" ABOVE GROUND · COLUMN-SUPPORTED

UPRIGHT STATIONS FROM SOUTH WALL (in): -63, -21.25, 0, 69.75, 146.15, 185, 186, 246, 253

PANEL SPACINGS (in): 41.75, 21.25, 69.75, 76.4, 38.85, 1, 60, 7

DEPTHS: south tip 8"; south wall 3' 8⅜"; at T1 7' 0⅝"; plateau 10' 8¾".


West door header is included. Closely spaced uprights at 185 / 186 in are retained from the model; opening framing needs coordination.

Concept geometry, not fabrication drawings. Member sizes, joints, bracing and bearing details require design.

The shallow hip roof cap sits above the rear ceiling datum; its internal framing has not been laid out.

T-E · TRUSS ELEVATION

South → north · station zero = south exterior garage wall · member layout projected directly from the current 3D model

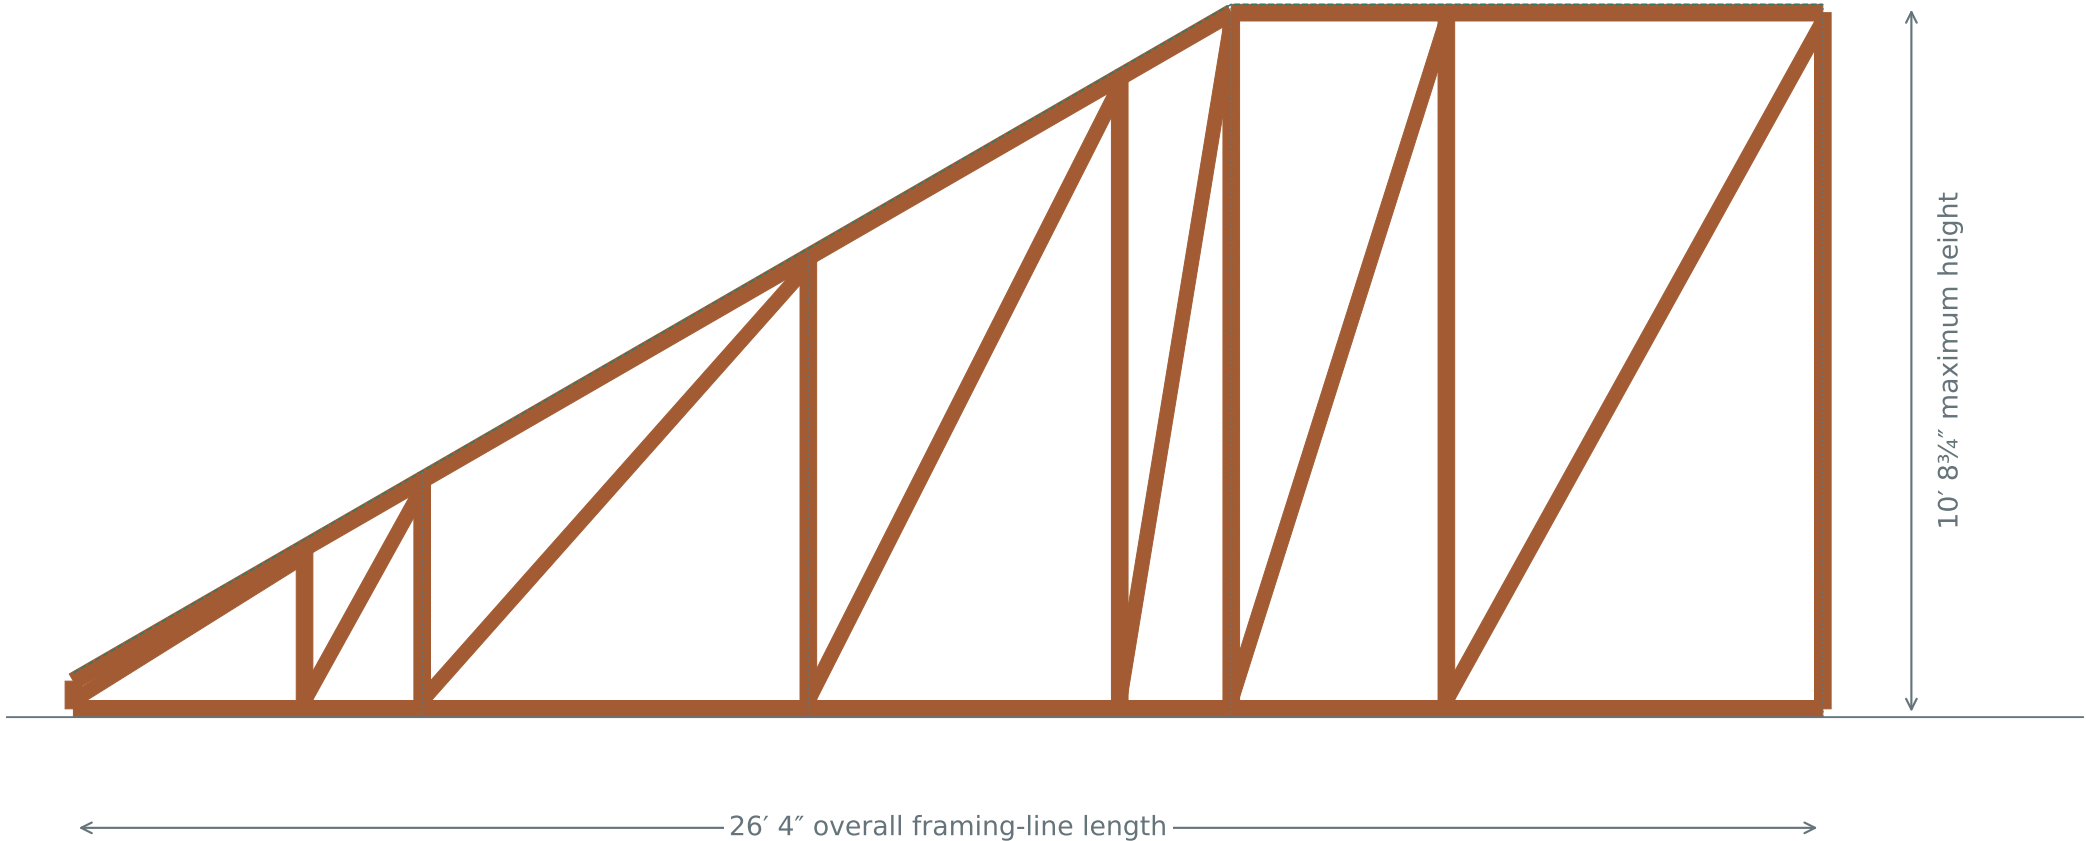


COMMON BOTTOM = 8' 2½" ABOVE GROUND · COLUMN-SUPPORTED

UPRIGHT STATIONS FROM SOUTH WALL (in): -63, -21.25, 0, 69.75, 126, 146.15, 185, 253
PANEL SPACINGS (in): 41.75, 21.25, 69.75, 56.25, 20.15, 38.85, 68
DEPTHS: south tip 8"; south wall 3' 8⅜"; at T1 7' 0⅝"; plateau 10' 8¾".
Support axis: N2 / S2 / optional S3.

Concept geometry, not fabrication drawings. Member sizes, joints, bracing and bearing details require design.
The shallow hip roof cap sits above the rear ceiling datum; its internal framing has not been laid out.

T-N · TRUSS ELEVATION

West → east · dimensions along the framing line · member layout projected directly from the current 3D model

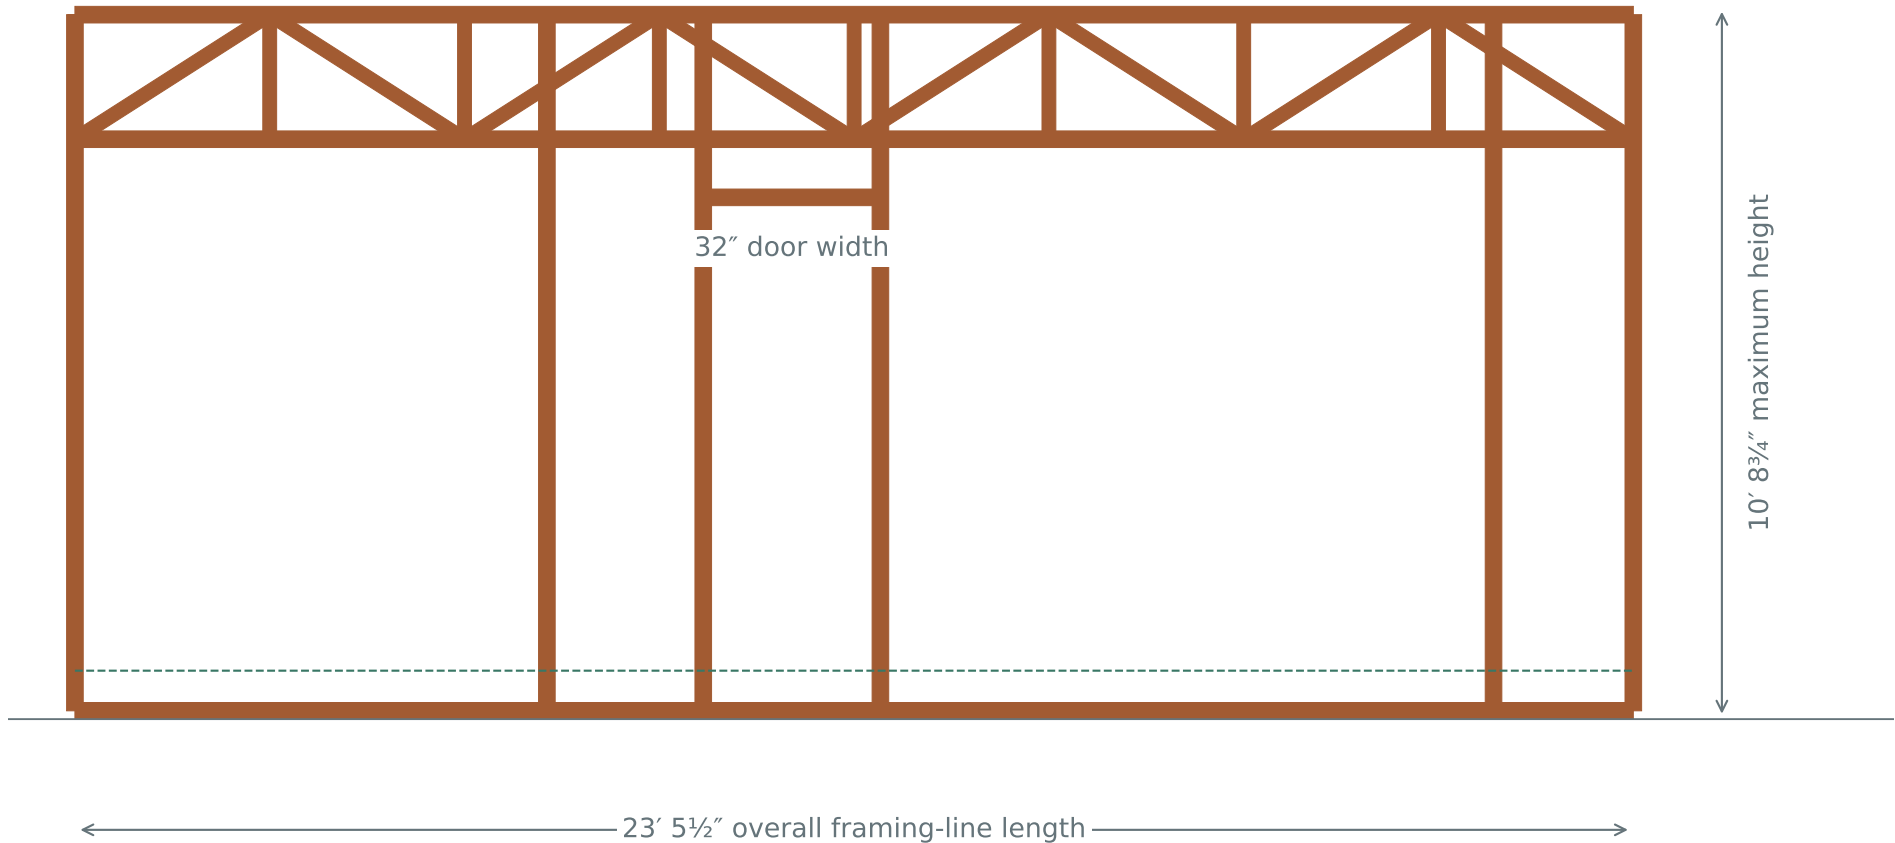

COMMON BOTTOM = 8' 2½" ABOVE GROUND · COLUMN-SUPPORTED

UPRIGHT STATIONS X (in): -32, 53.25, 81.5, 113.5, 224.25, 249.5.
HEADER: nominal 24" deep; eight equal bays of 35 3/16 in. Door: 32" wide × 84" high above loft floor.
DOOR center X = 97½"; opening edges X = 81½" / 113½". Floor is 8¾" above common truss bottom.
North wall windows and side webs require coordination. Overall truss includes west walkway width; it is not loft-floor width.

Concept geometry, not fabrication drawings. Member sizes, joints, bracing and bearing details require design.
The shallow hip roof cap sits above the rear ceiling datum; its internal framing has not been laid out.