



The connected Python frame model

T1, T-E and T-W contain upper chords, lower chords and webs — not standalone beams.

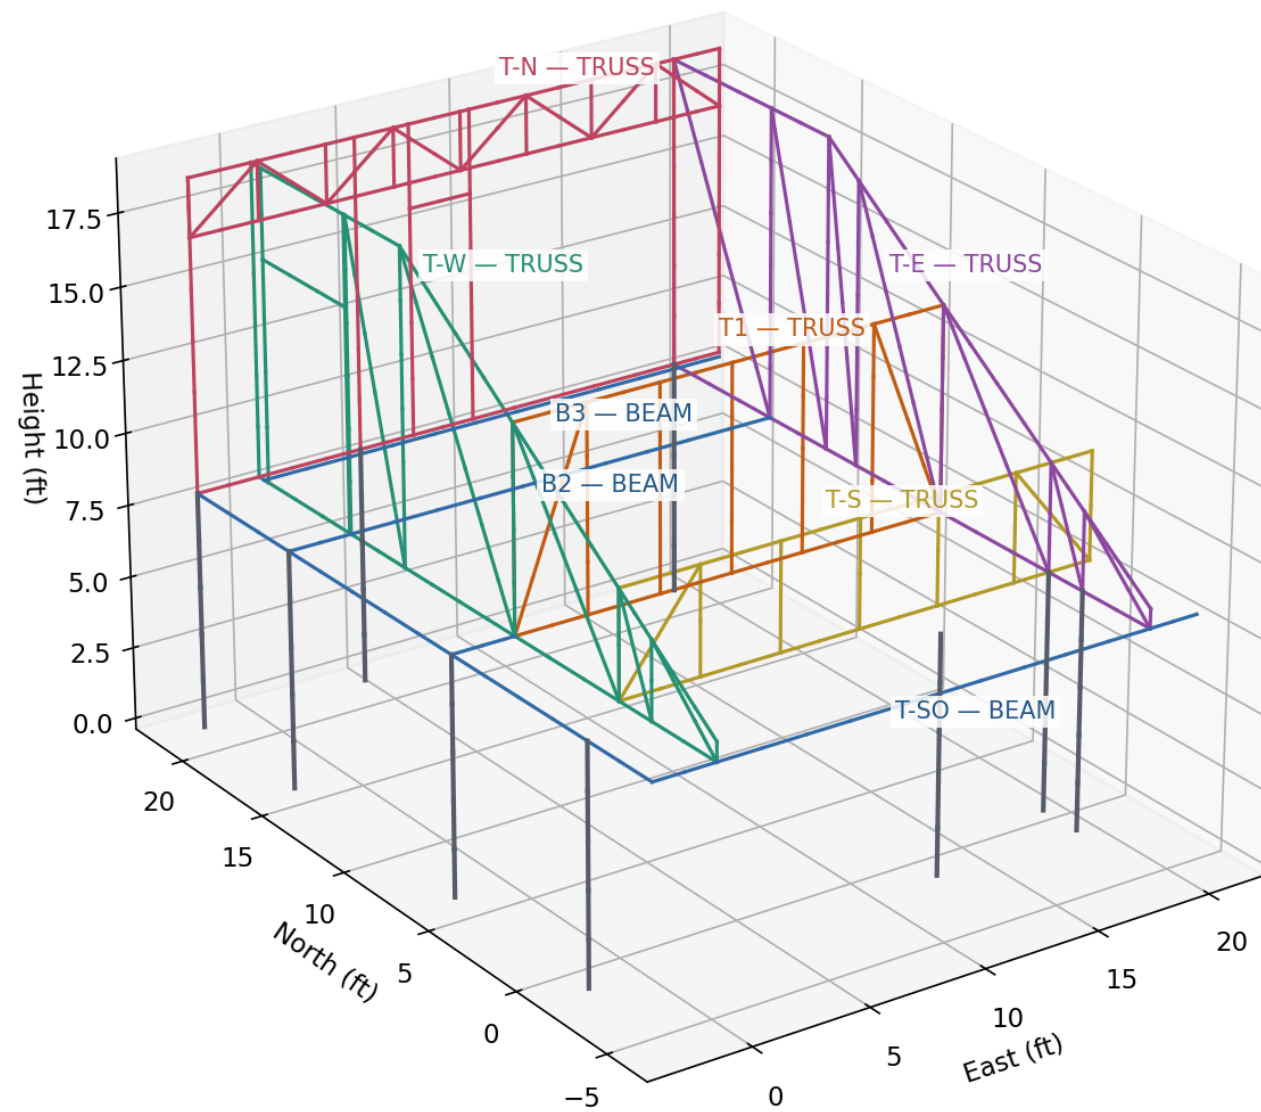

Saved HSS baseline • W-section trolley revision is not yet calculated • hip-cap rafters are not modeled


Framing plan — corrected member labels

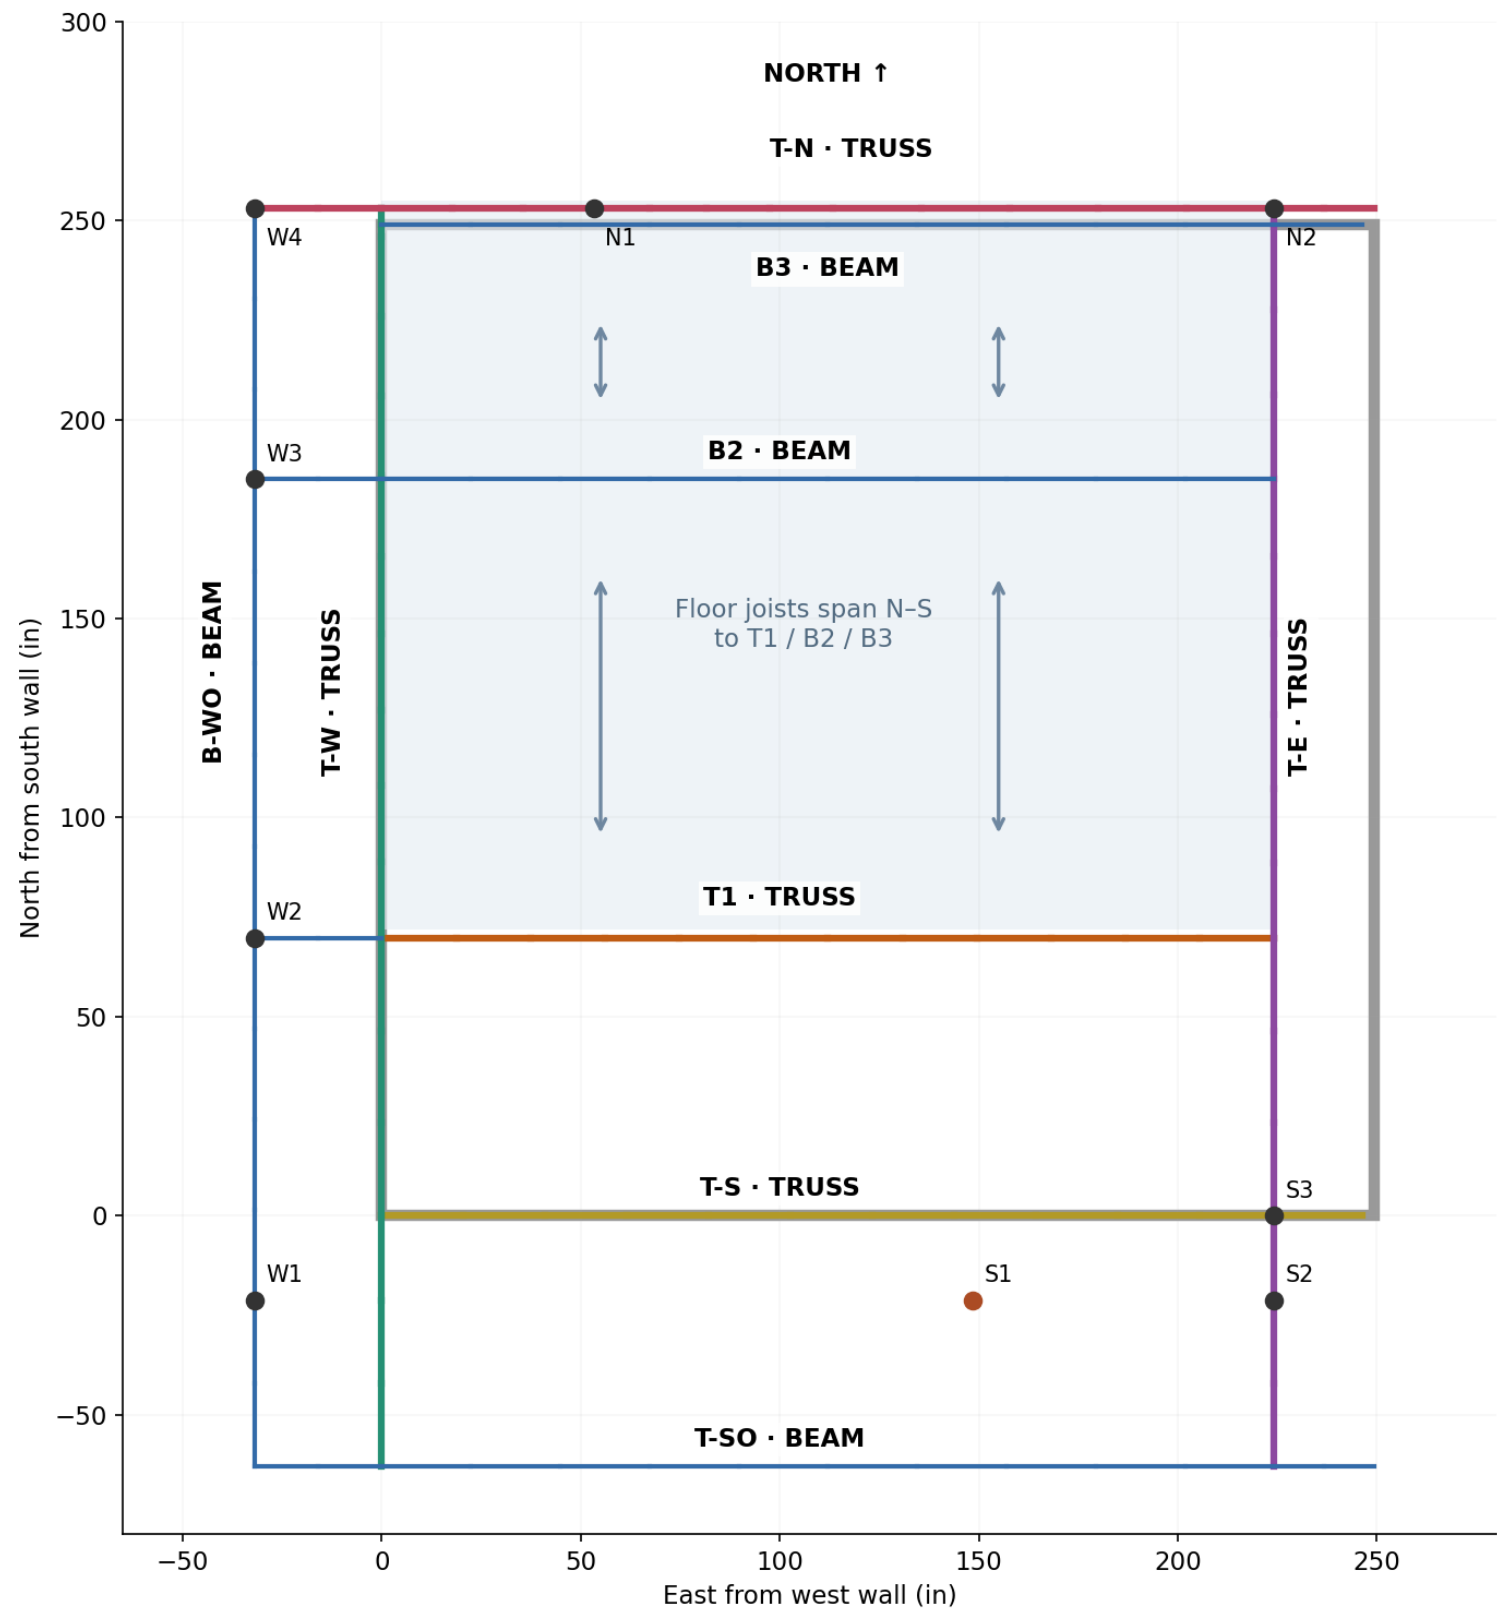


Colored truss lines represent complete vertical trusses shown on the elevation sheet.
Gray outline = existing walls; no added wall support credited. S1 currently disconnected; S3 assumed present.

Actual truss geometry and calculated movement


T1 — transverse TRUSS

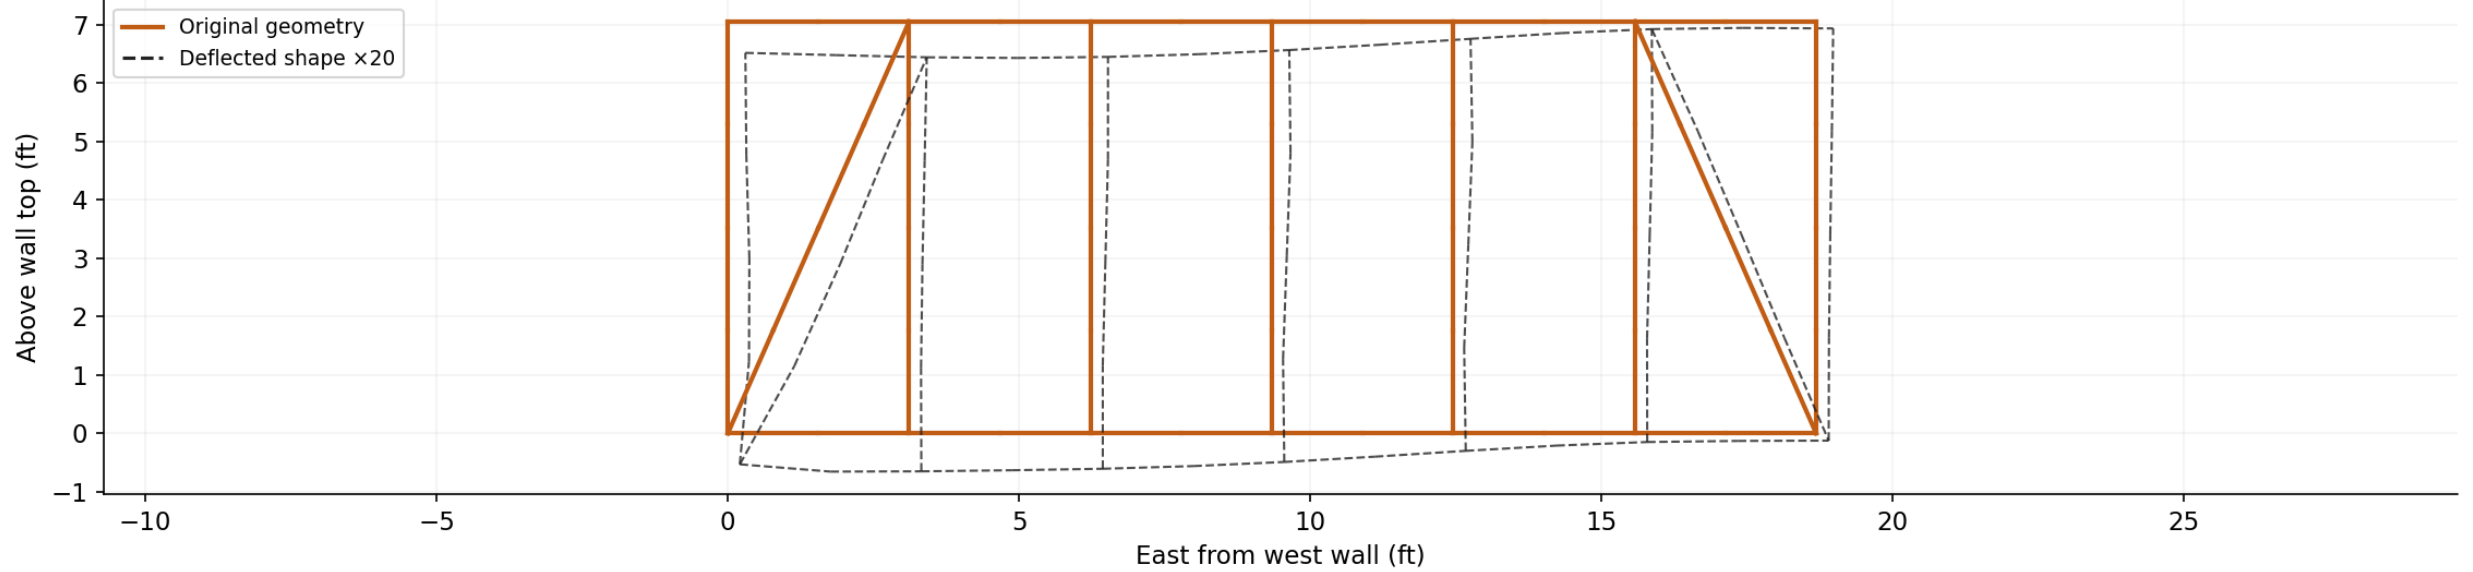

T-E — east longitudinal TRUSS

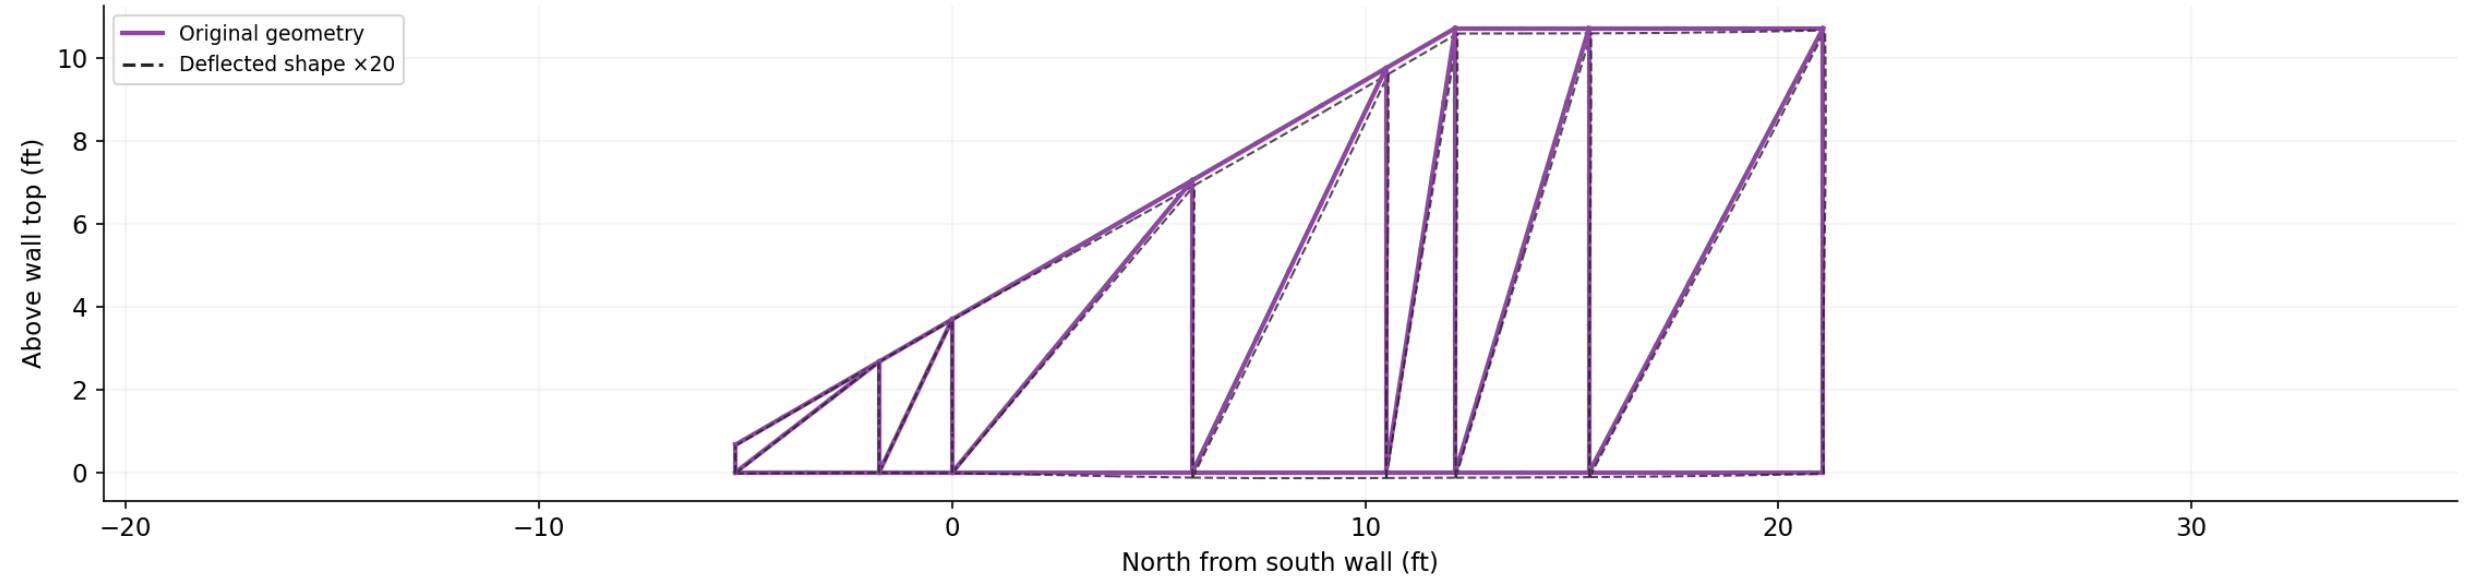

T-W — west longitudinal TRUSS

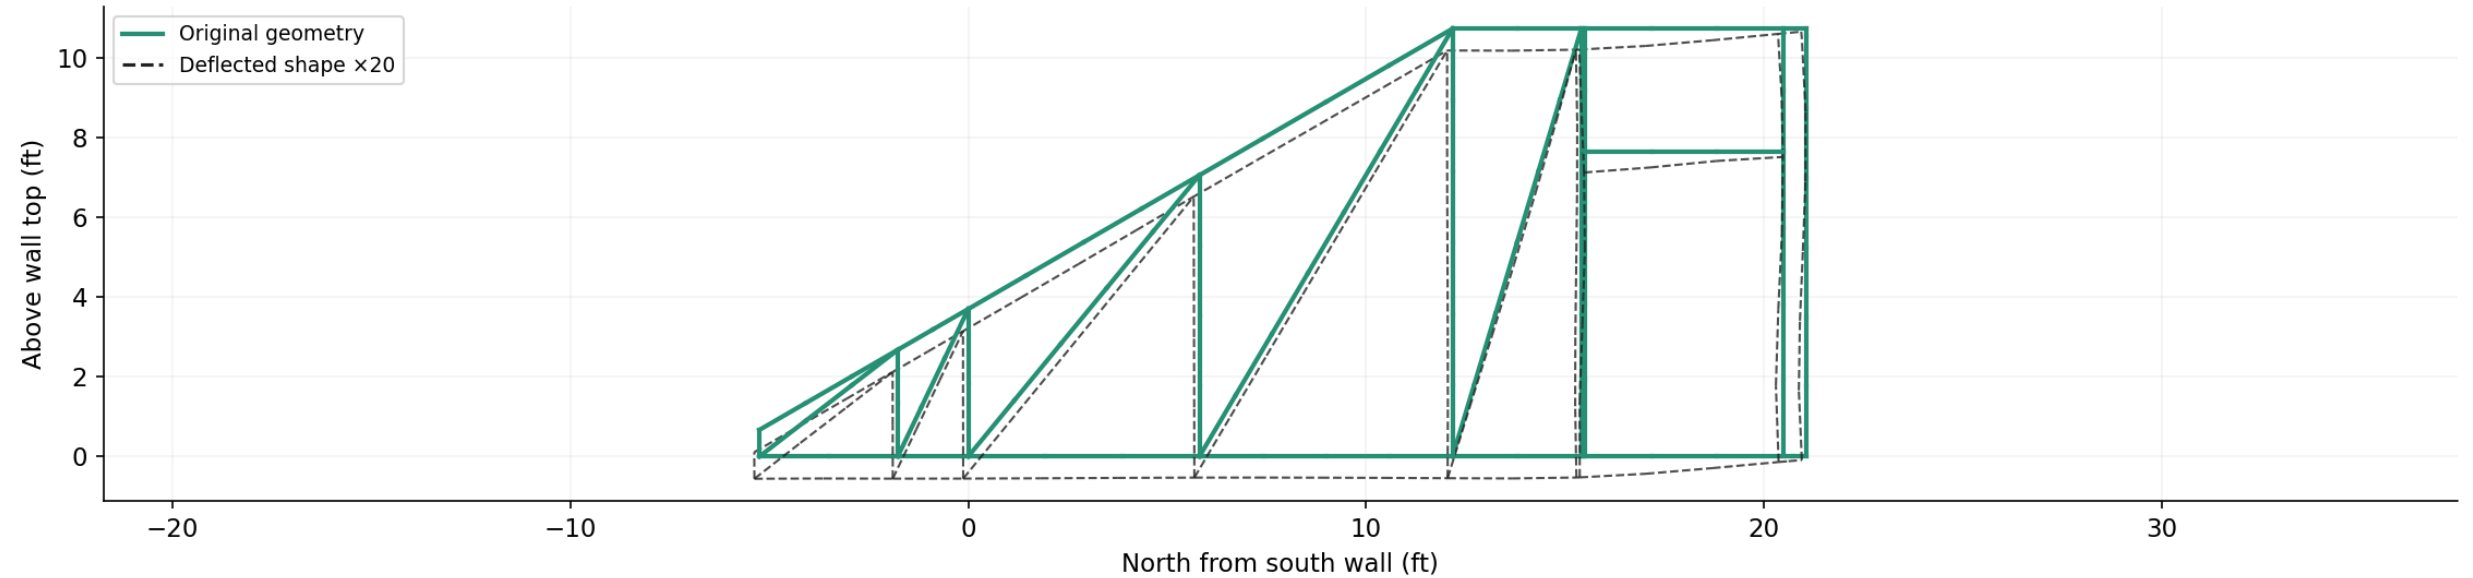

Perimeter-storage service case • global maximum vertical movement 0.644 in • rigid-joint HSS baseline