



Roof-first construction: where the current framing conflicts

T1 section · looking north · Y = 69.75 in

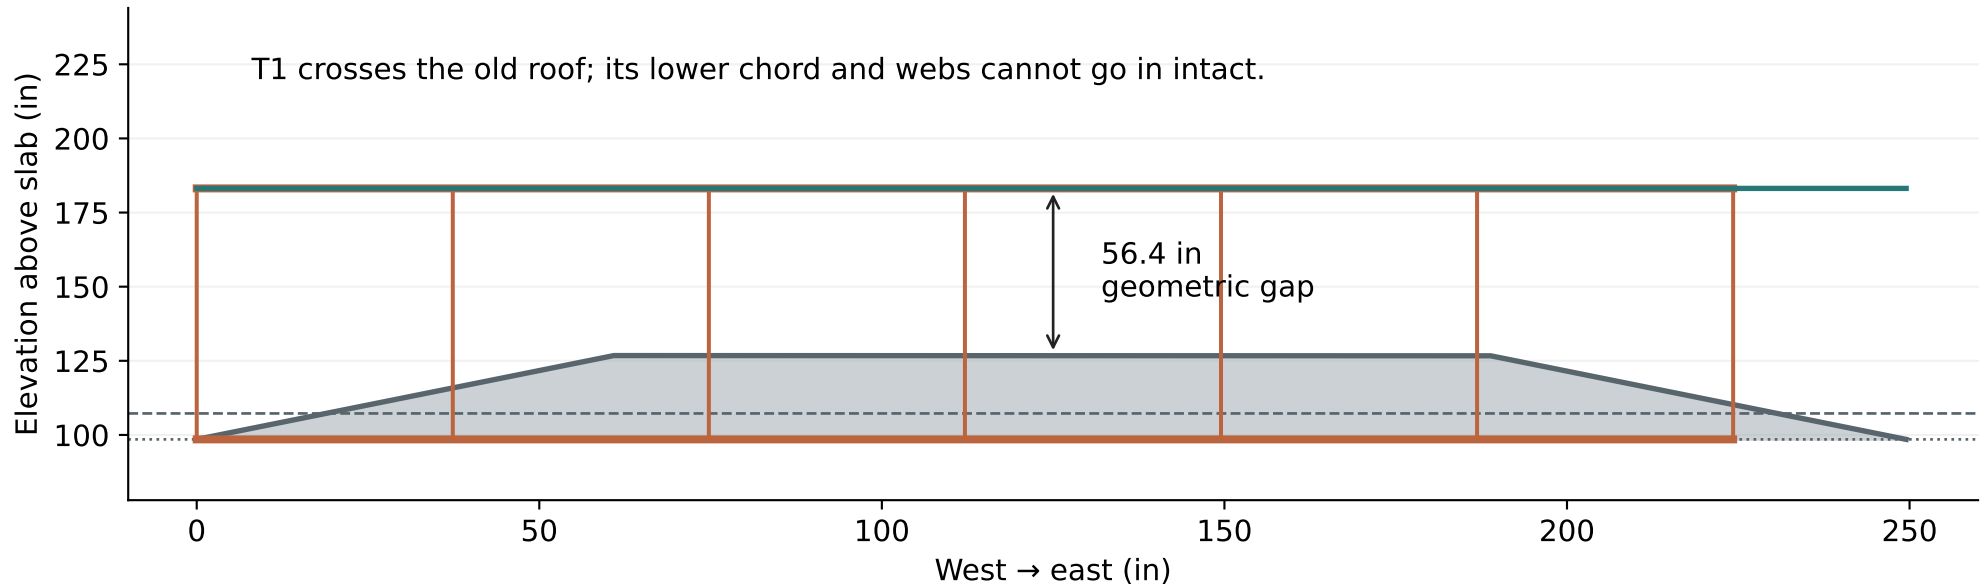

T-E section · looking west · X = 224.25 in

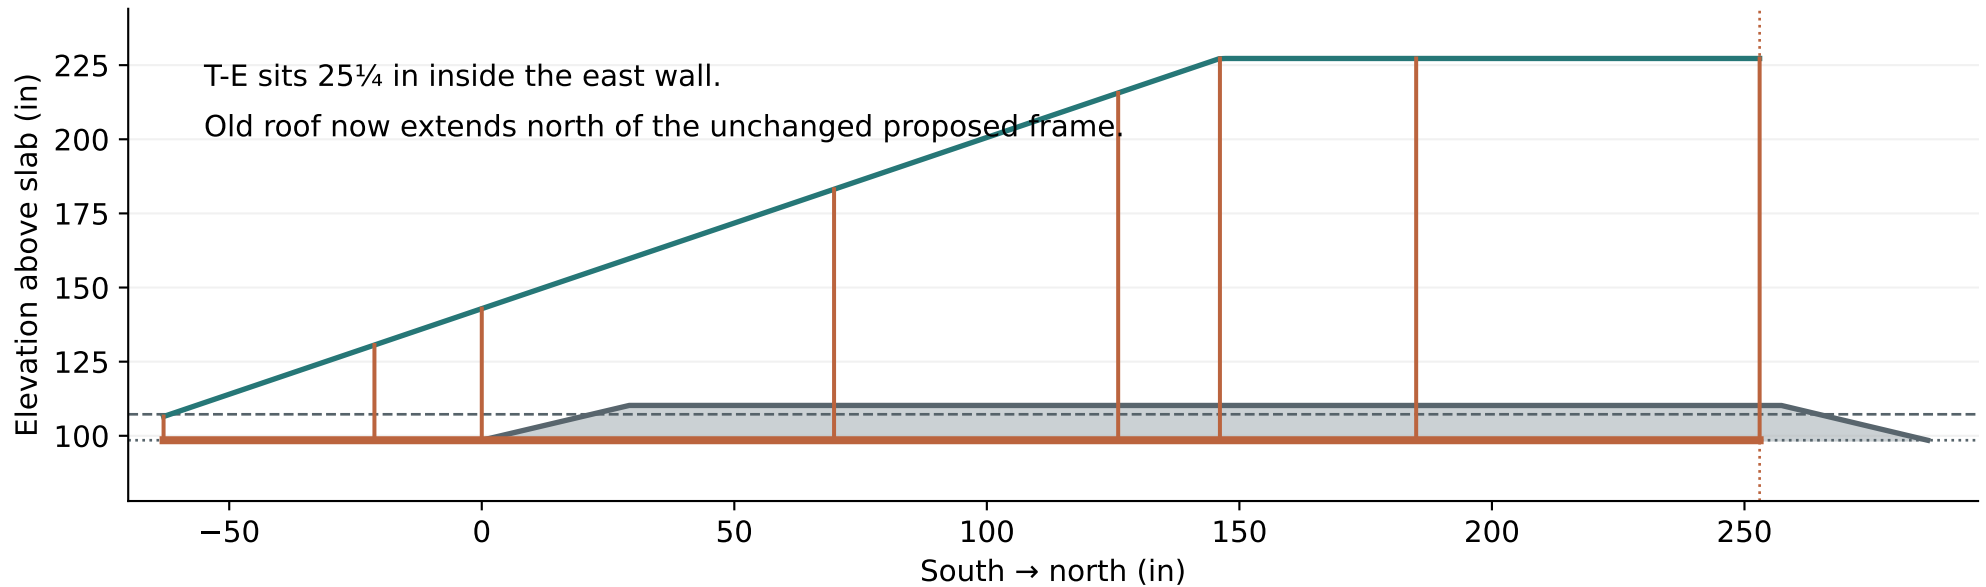

- Existing roof surface
- New roof underside
- Current full-depth truss
- Future loft datum