
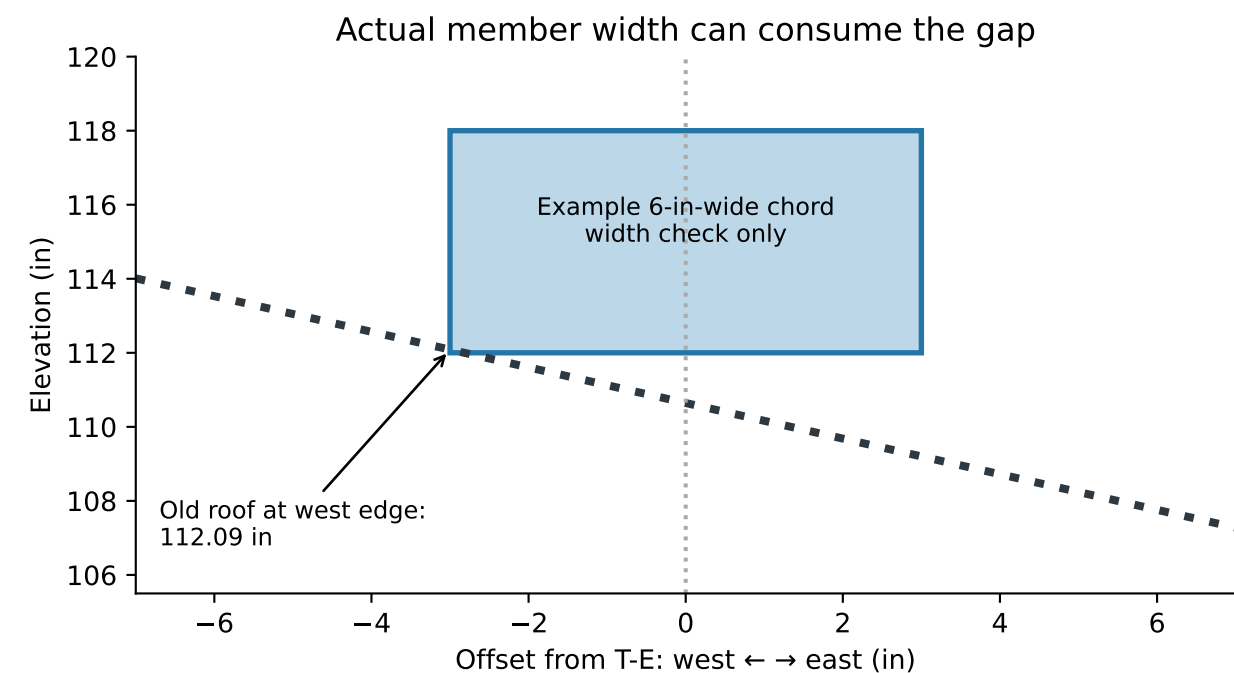
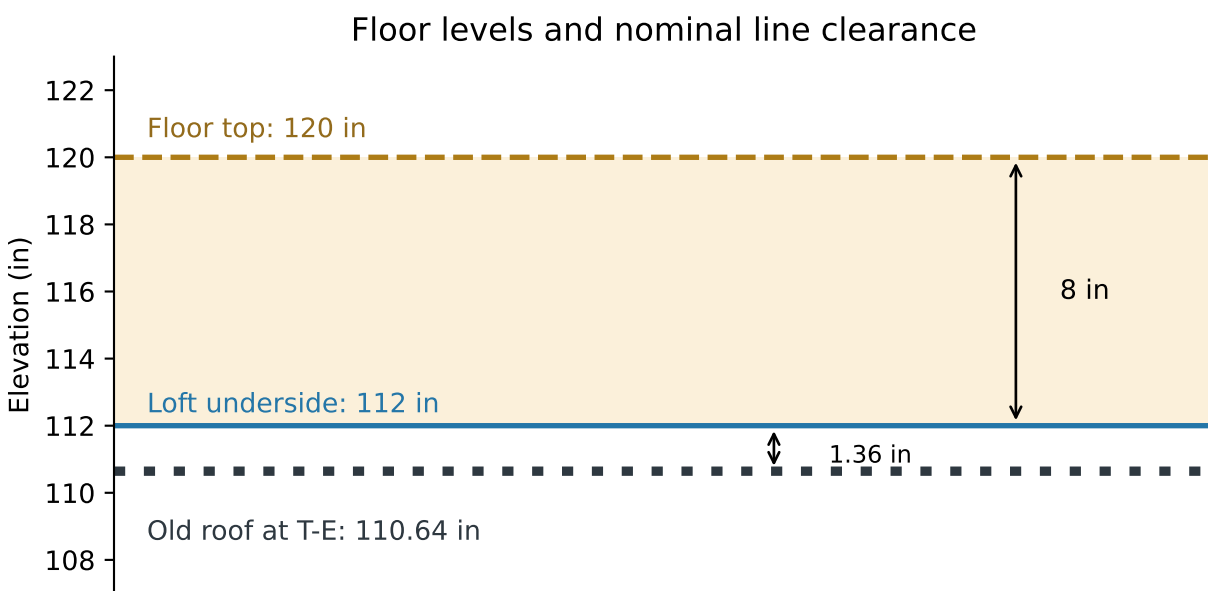


T-E with loft underside at 9 ft 4 in

East-side elevation • bottom chord horizontal; upper chord follows proposed roof

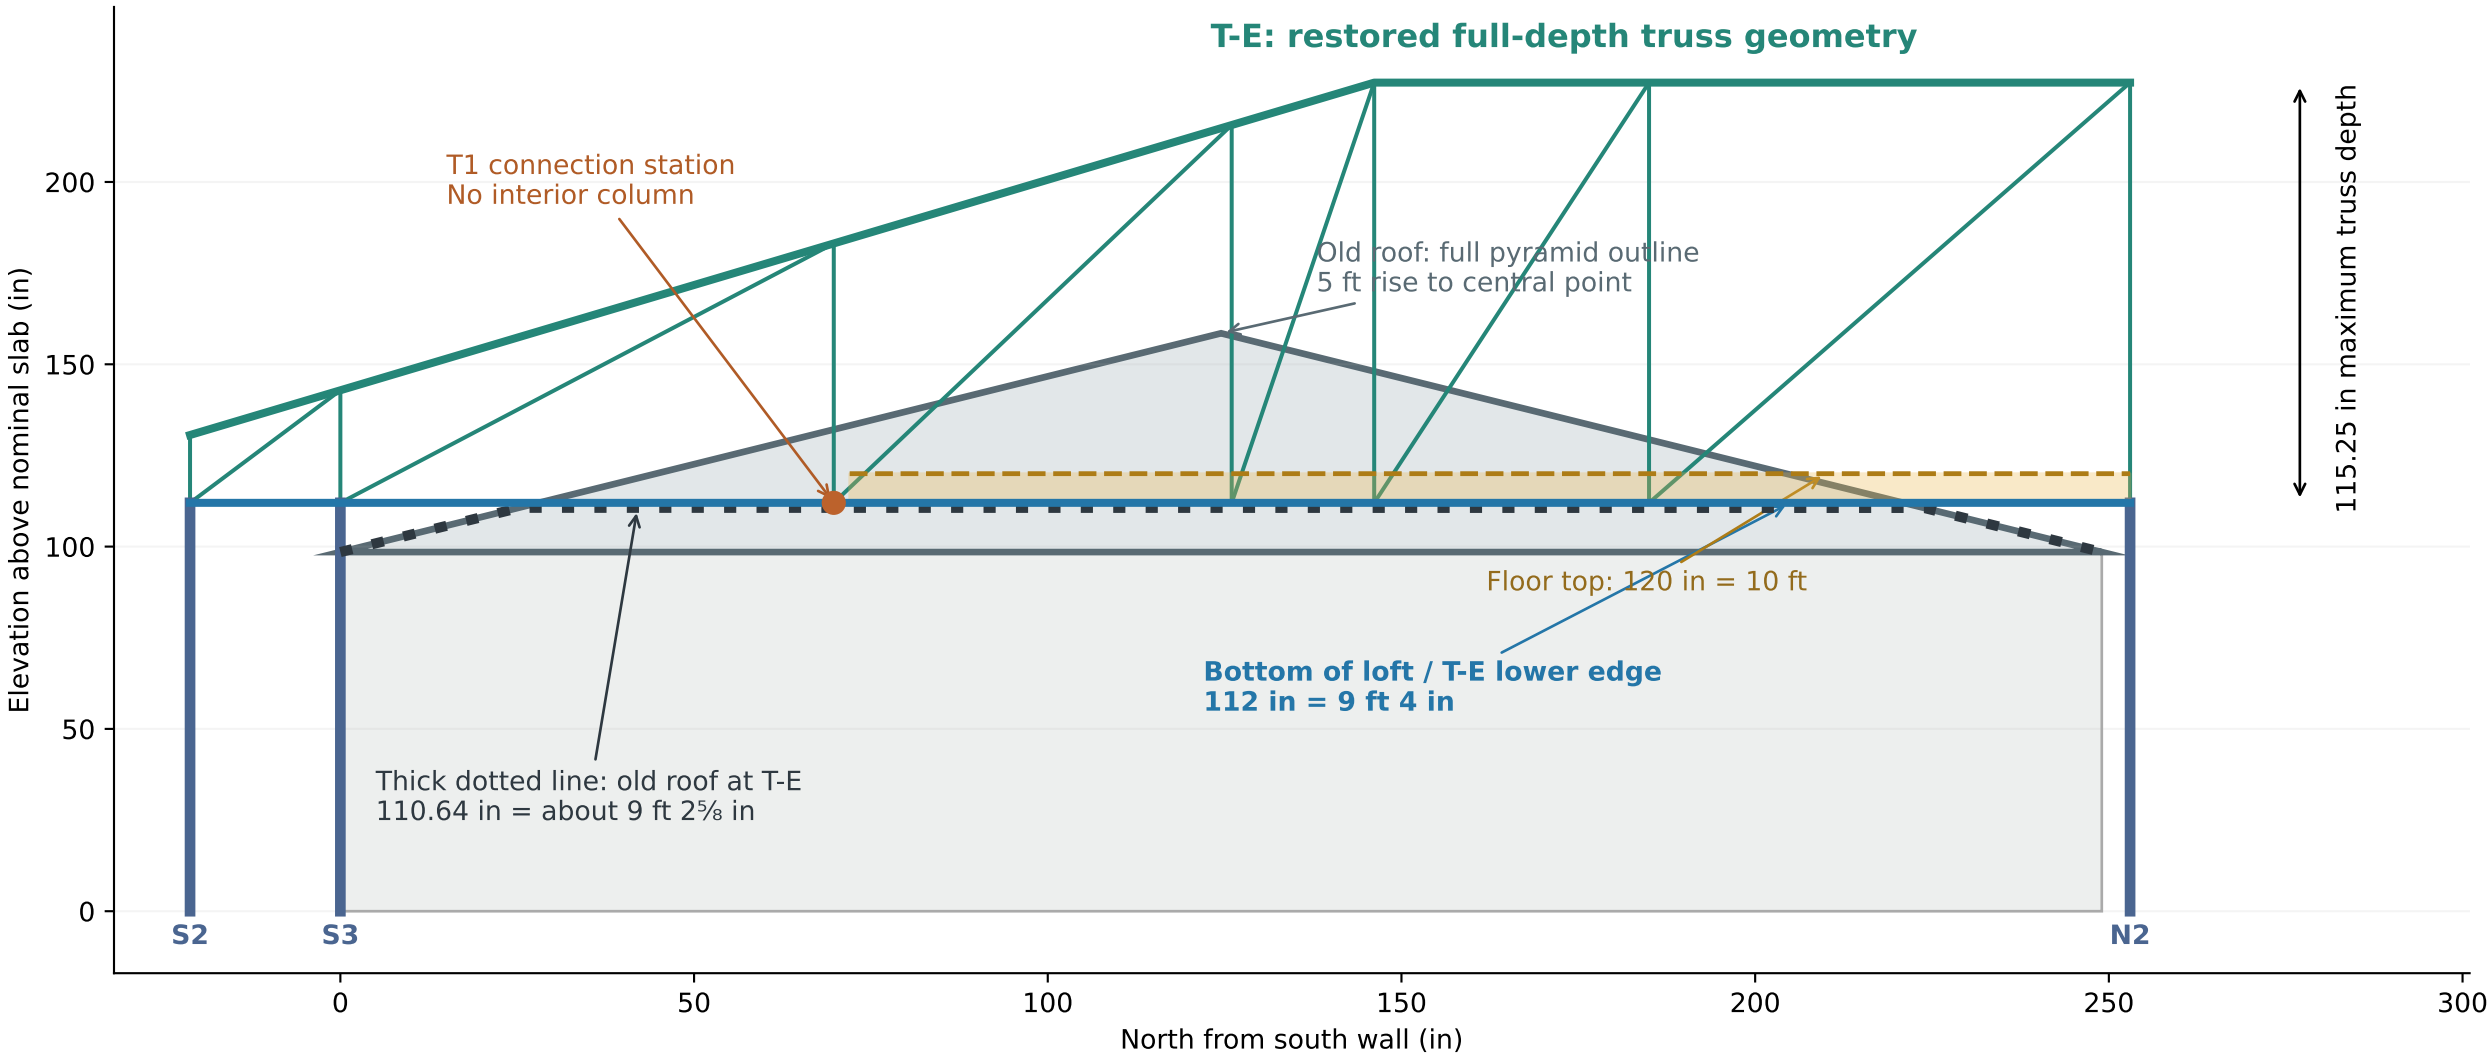

Geometry revision only: member sizes and web/connection details require reanalysis. Footprint retained at 249.5 × 249 in.
The 1.36-in gap is at the T-E line, not a verified construction clearance. Floor-height T1 and the full loft still intersect the old roof elsewhere.