


EAST WALL STUDY / FLOOR PLAN

EW-P6 Wall strengthening over the revision 11 plan • north up

Discussion sketch | September 15, 2026

ARCH-006 / P2 | Rev 3 | 2026-09-15 | Status: draft | Units: ft / in | Not to scale; use dimensions


ORANGE / POSSIBLE GROUND-FLOOR EXTENSION — option for discussion

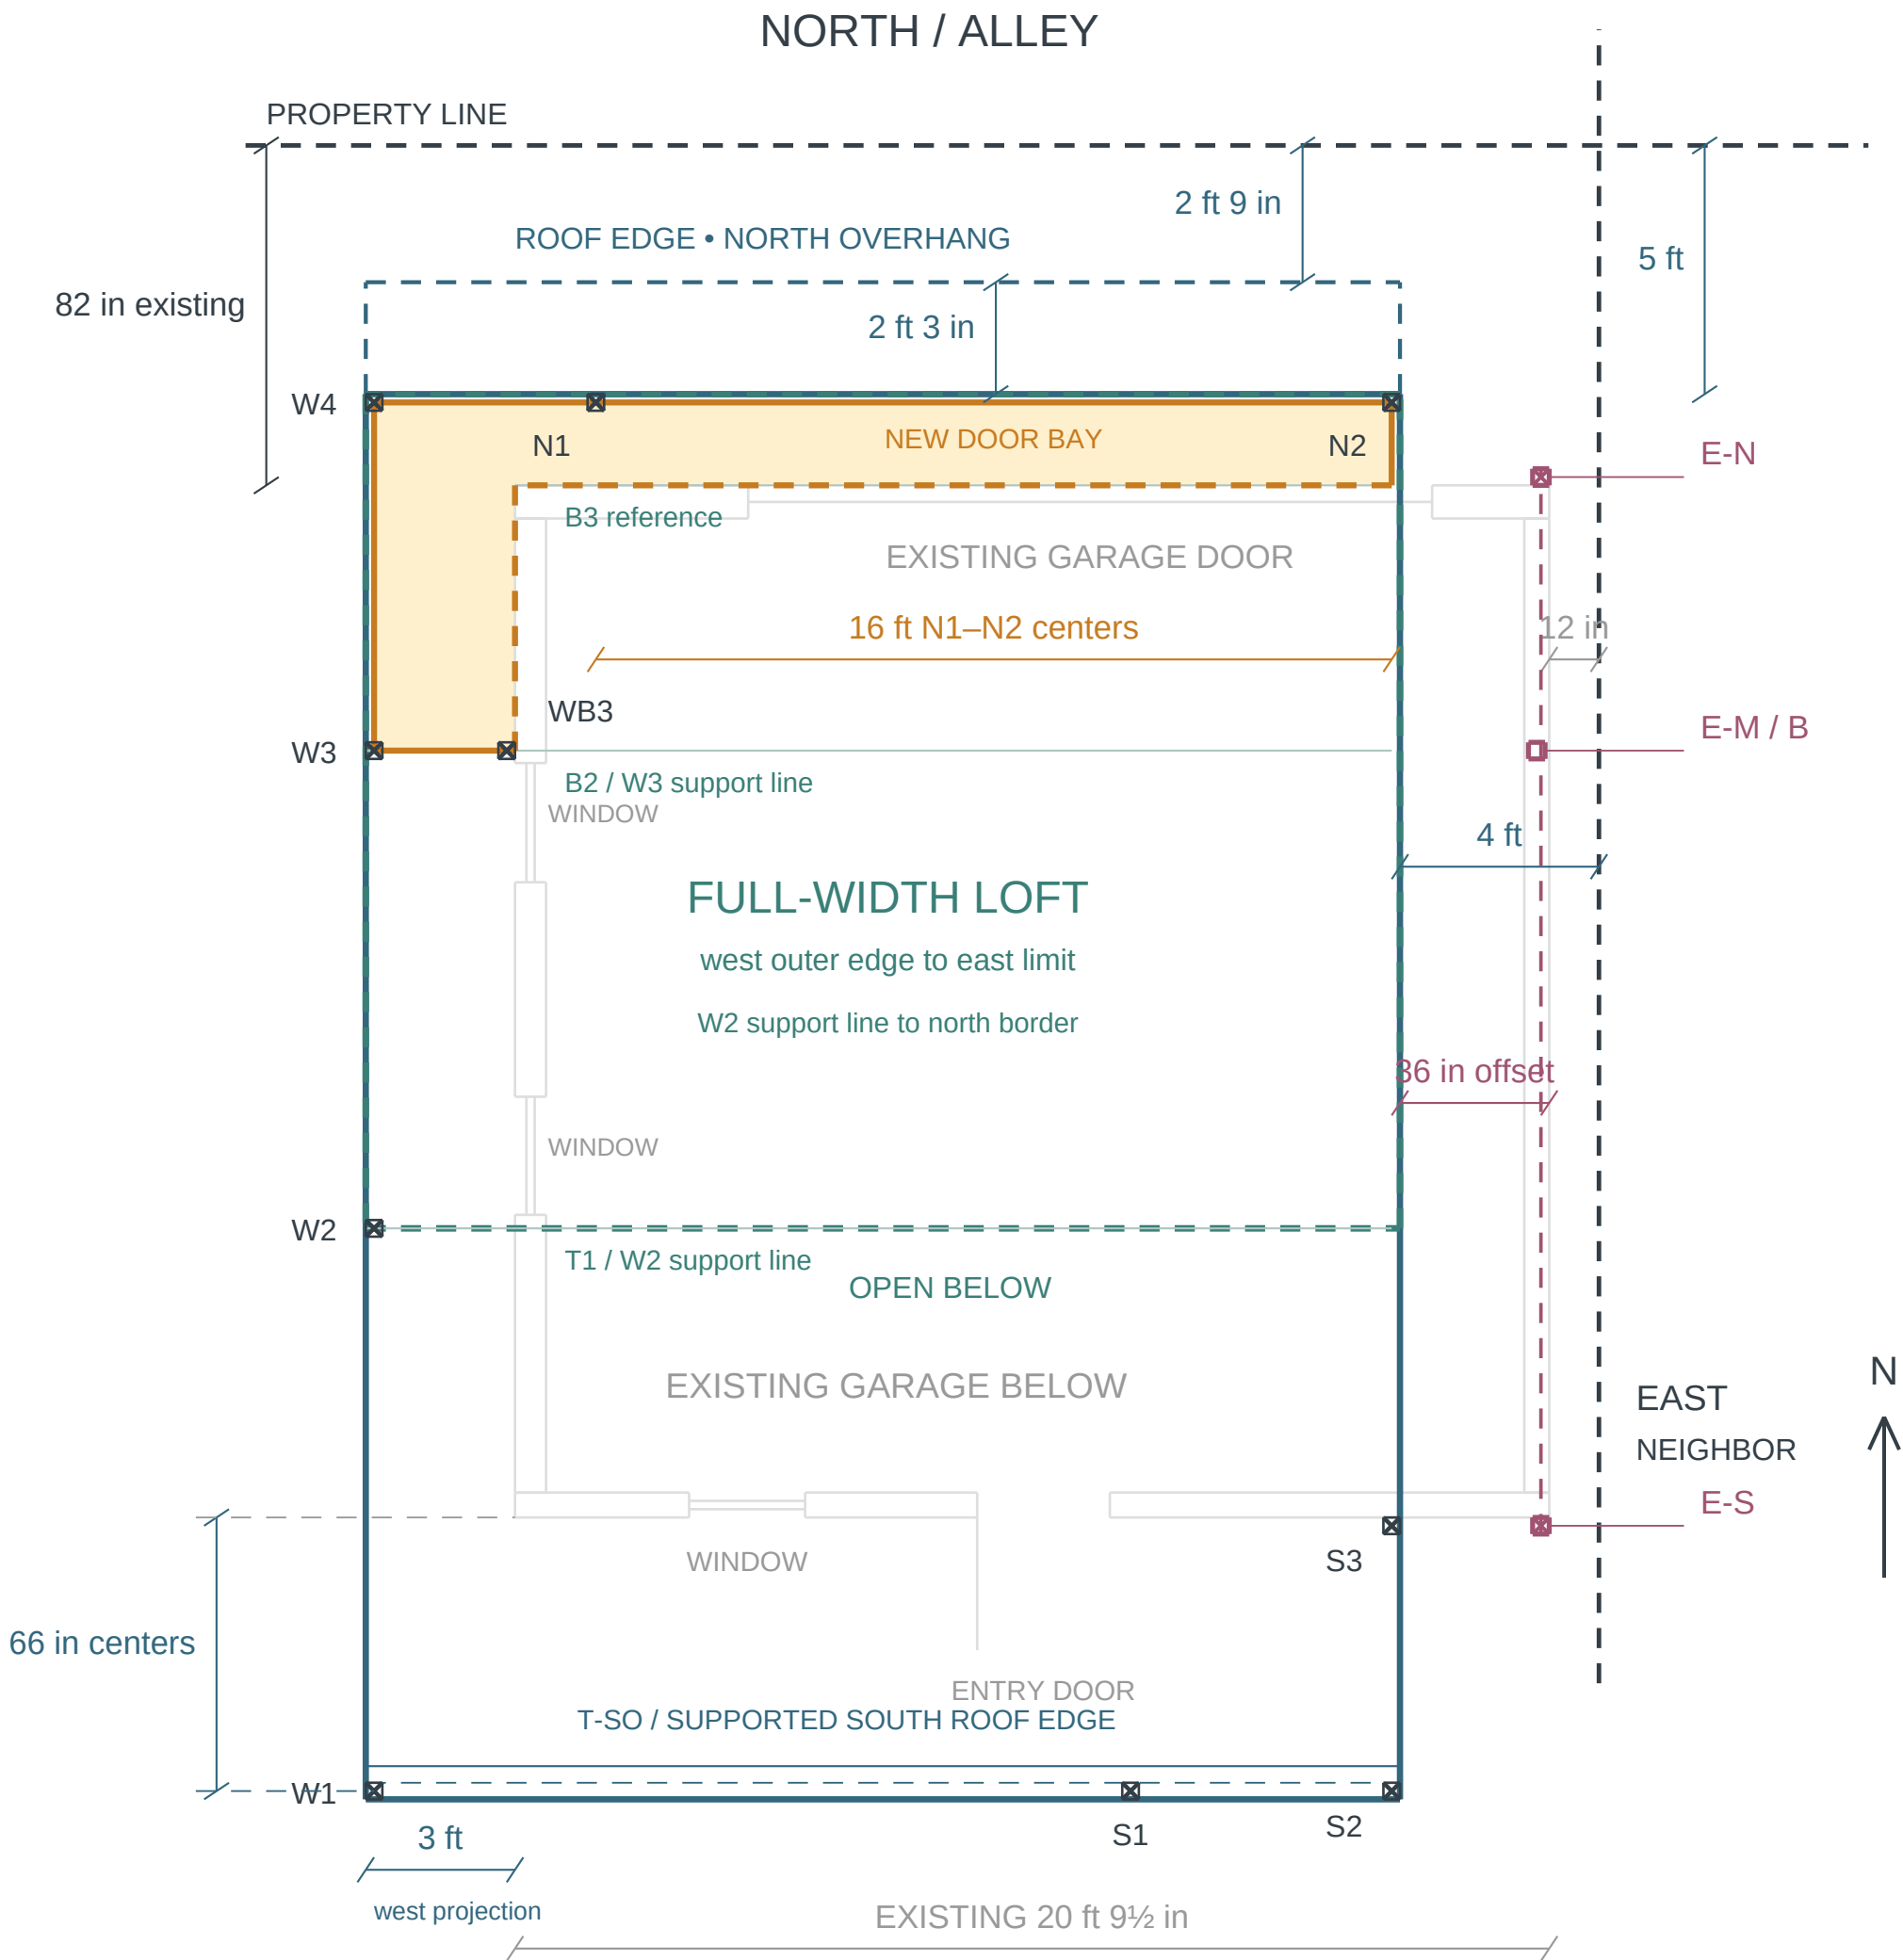

EAST WALL FRAME / TWO OPTIONS


A — E-S + E-N end posts with overhead beam/truss.
B — Same frame, plus concealed E-M aligned with W3.
Purple dashes along wall = overhead beam centerline.
E-S/E-N are separate from upper-frame S/N columns.
End-post east faces align with existing wall east face.
Entire 12-in east strip stays clear of posts.

1 / NORTH END POST — PLAN DETAIL

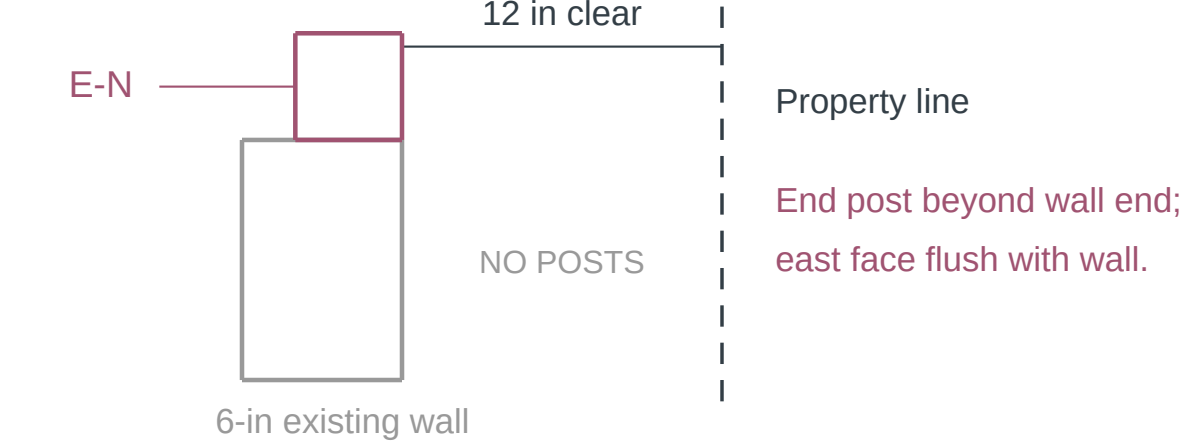

South end mirrors this: E-S lies just south of the wall.

2 / CENTER POST — PLAN DETAIL (B ONLY)

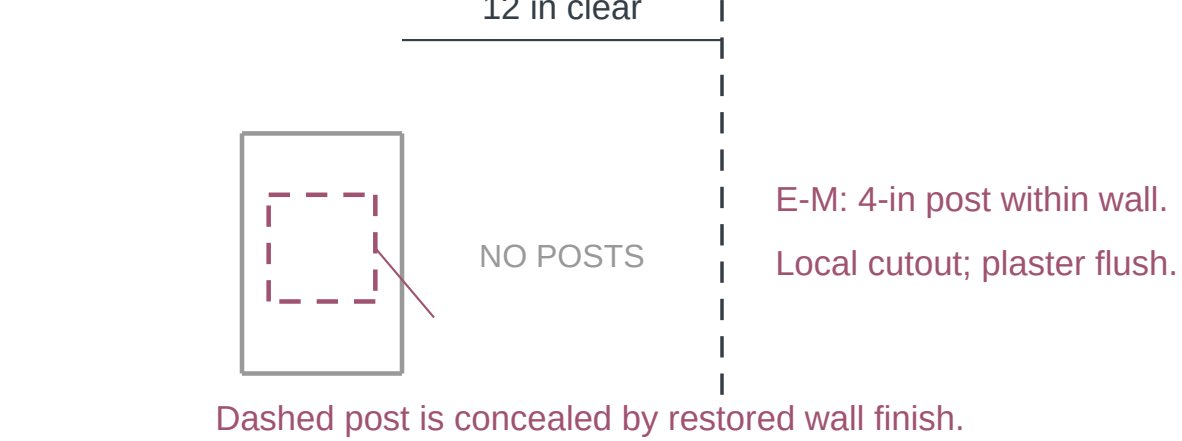

CONNECTIONS TO DEVELOP

Upper steel edge stays 36 in inward of the wall face.
Beam width, transfer connections and foundations are unresolved.
E-M/B now aligns with W3 at 185 in north of the south wall.
WBN removed; N1 moved 16 ft west of N2 (centers).

Sources: Draft East Wall strengthening (linked task), East Wall Study rev. 04, and current floor plan rev. 11.