


GARAGE / UPPER STRUCTURE + COLUMNS

11 Earlier floor-plan base • north up • dimensions in feet and inches

Discussion sketch | September 15, 2026

ARCH-006 / P1 | Rev 3 | 2026-09-15 | Status: draft | Units: ft / in | Not to scale; use dimensions

ORANGE / POSSIBLE GROUND-FLOOR EXTENSION — option for discussion

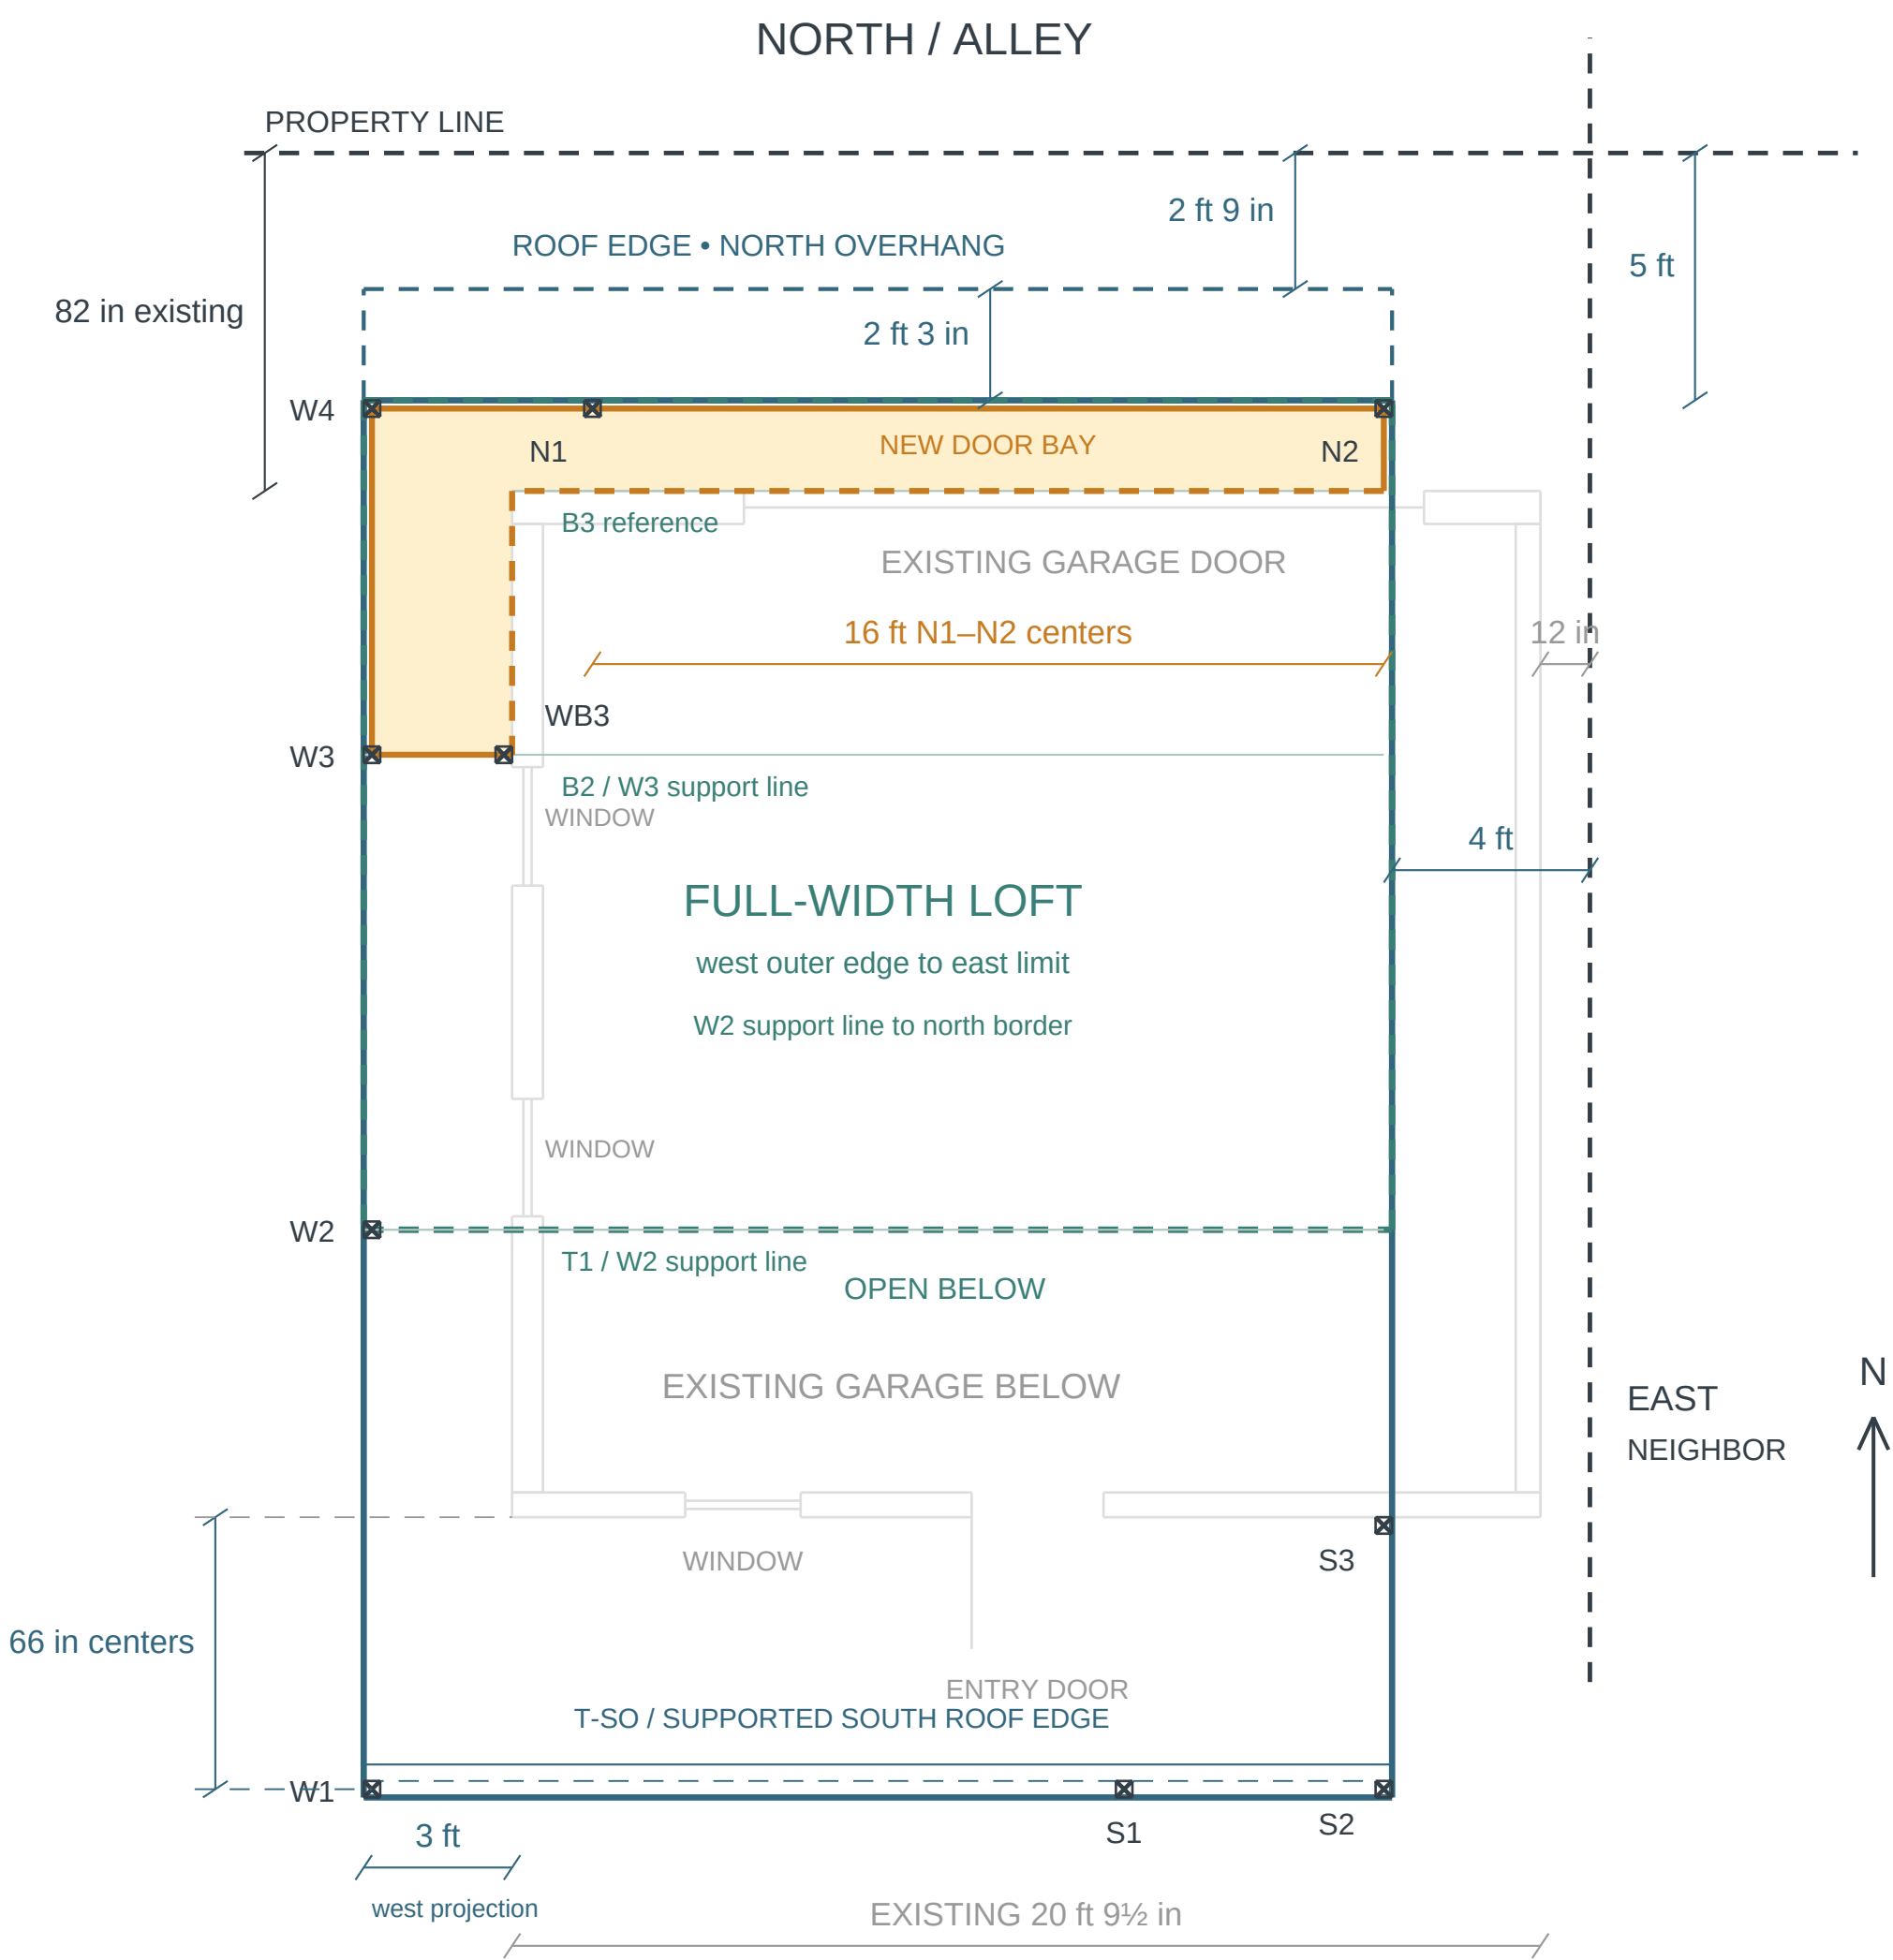

OUTLINES + SUPPORTS

Blue / full upper structure

West and south follow the outer beams.

East outside face: 4 ft from property line.

North outside face: 5 ft from property line.

Dashed blue: 2 ft 3 in north roof overhang.

Teal / loft floor

Expanded to the full available width.

West, east and north edges meet blue outline.

South edge follows W2 at Y = 69¾ in.

Supported along the west by W2, W3, W4.

Teal dashes overlay shared blue boundaries.

Columns / flush outside edges

W1 sits flush in the southwest corner.

S1 and S2 south faces meet the blue edge.

S2 east face also meets the blue edge.

S3 center aligned with east-wall post E-S.

Outer beam locations

West beam centerline: 32 in west of wall.

South beam supported by W1, S1 and S2.

Roof edge at beam outside face (assumed).

COORDINATION NOTES

Blue outline retained; column symbols are 4 in.

W1/S1/S2 centers: 66 in south; faces at 68 in.

WBN removed; N1–N2 centers spaced 16 ft.

North column faces remain flush with 5-ft limit.

Sources: labeled framing plan / member register; earlier model for member widths; loft and north supports revised to your instructions.