


GARAGE / UPPER STRUCTURE + COLUMNS

05 Earlier floor-plan base • north up • dimensions in feet and inches

Discussion sketch | September 15, 2026

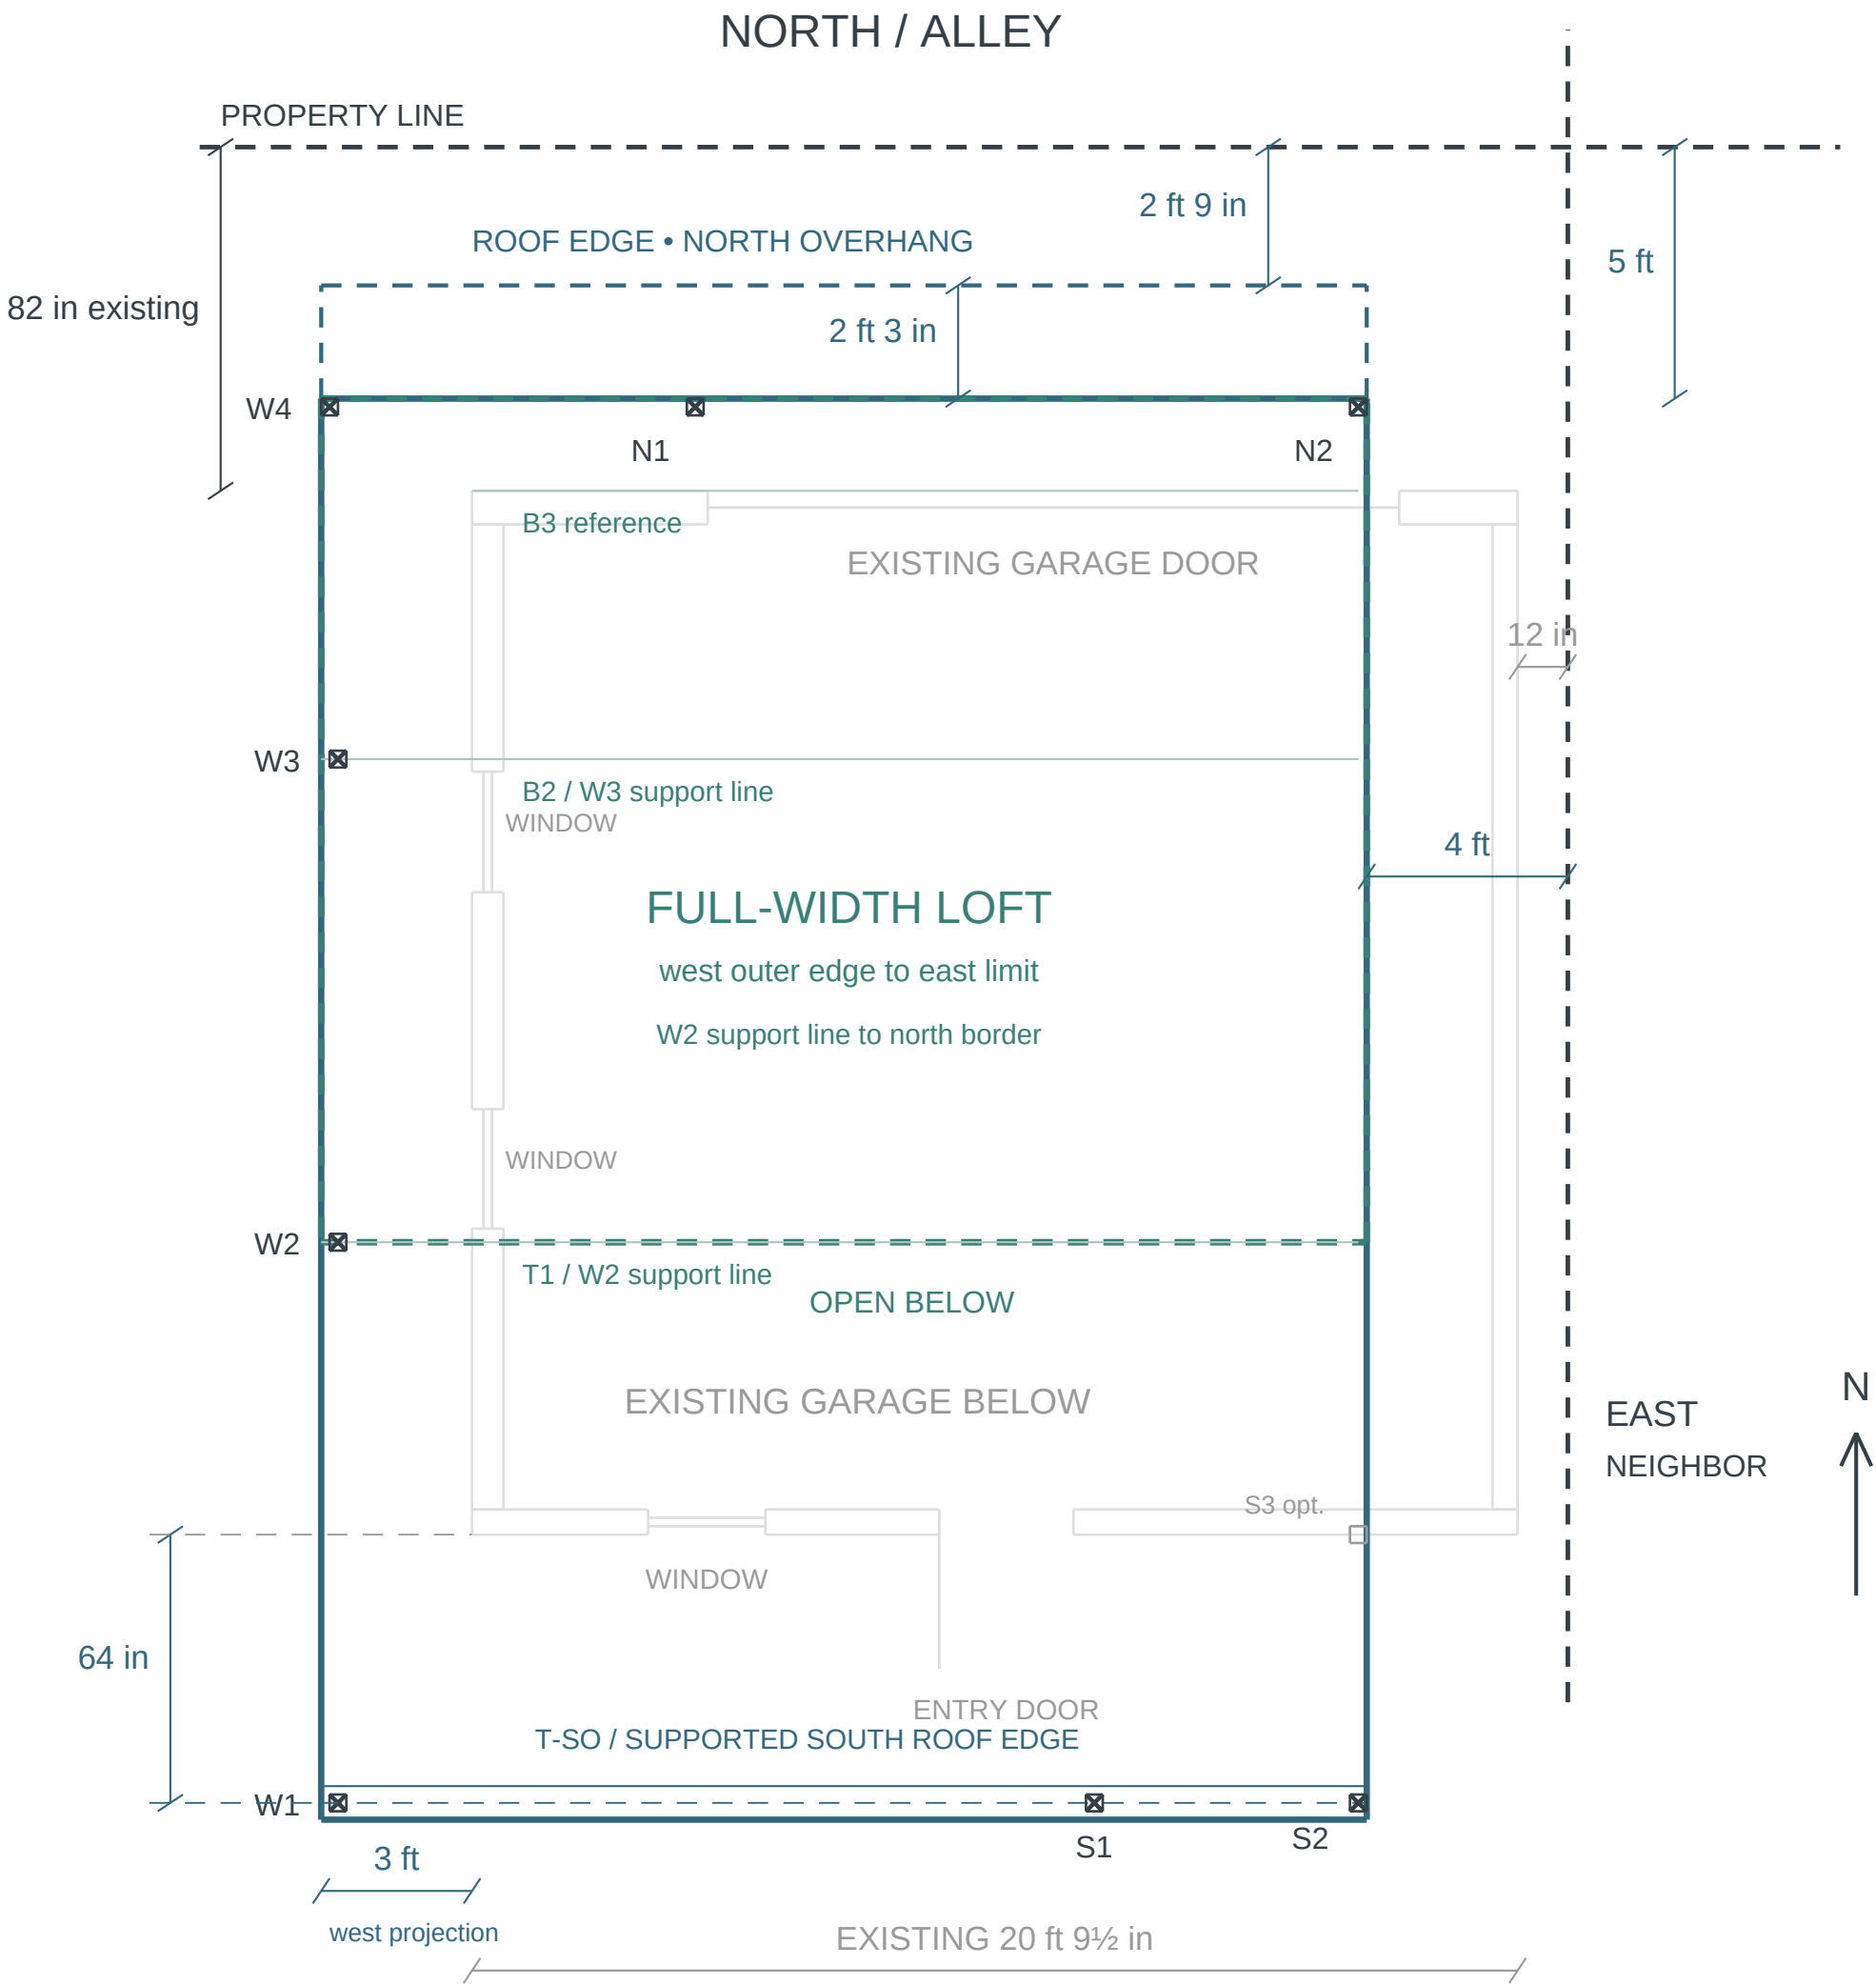

OUTLINES + SUPPORTS

Blue / full upper structure

West and south follow the outer beams.

East outside face: 4 ft from property line.

North outside face: 5 ft from property line.

Dashed blue: 2 ft 3 in north roof overhang.

Teal / loft floor

Expanded to the full available width.

West, east and north edges meet blue outline.

South edge follows W2 at Y = 69 3/4 in.

Supported along the west by W2, W3, W4.

Teal dashes overlay shared blue boundaries.

Columns / revised north row

N1 and N2 moved to the north border.

W4 moved to the northwest corner.

4-in symbols sit inside the outline.

W1, S1, S2 stay 64 in south of wall.

Outer beam locations

West beam centerline: 32 in west of wall.

South beam centered over W1, S1 and S2.

Roof edge at beam outside face (assumed).

COORDINATION NOTES

North column faces flush with 5-ft limit.

Their centers sit 2 in inside the north edge.

S3 remains optional; east limit remains 4 ft.

South beam width: 8 in provisional; edge 68 in.

Sources: labeled framing plan / member register; earlier model for member widths; loft and north supports revised to your instructions.