


STORAGE LOFT / LIFTING STAIR


West-side elevation · looking east · NORTH ← → SOUTH

ST-01 · Draft concept · 15 Sep 2026 · Dimensioned study, not a construction drawing

01 / STAIR RAISED

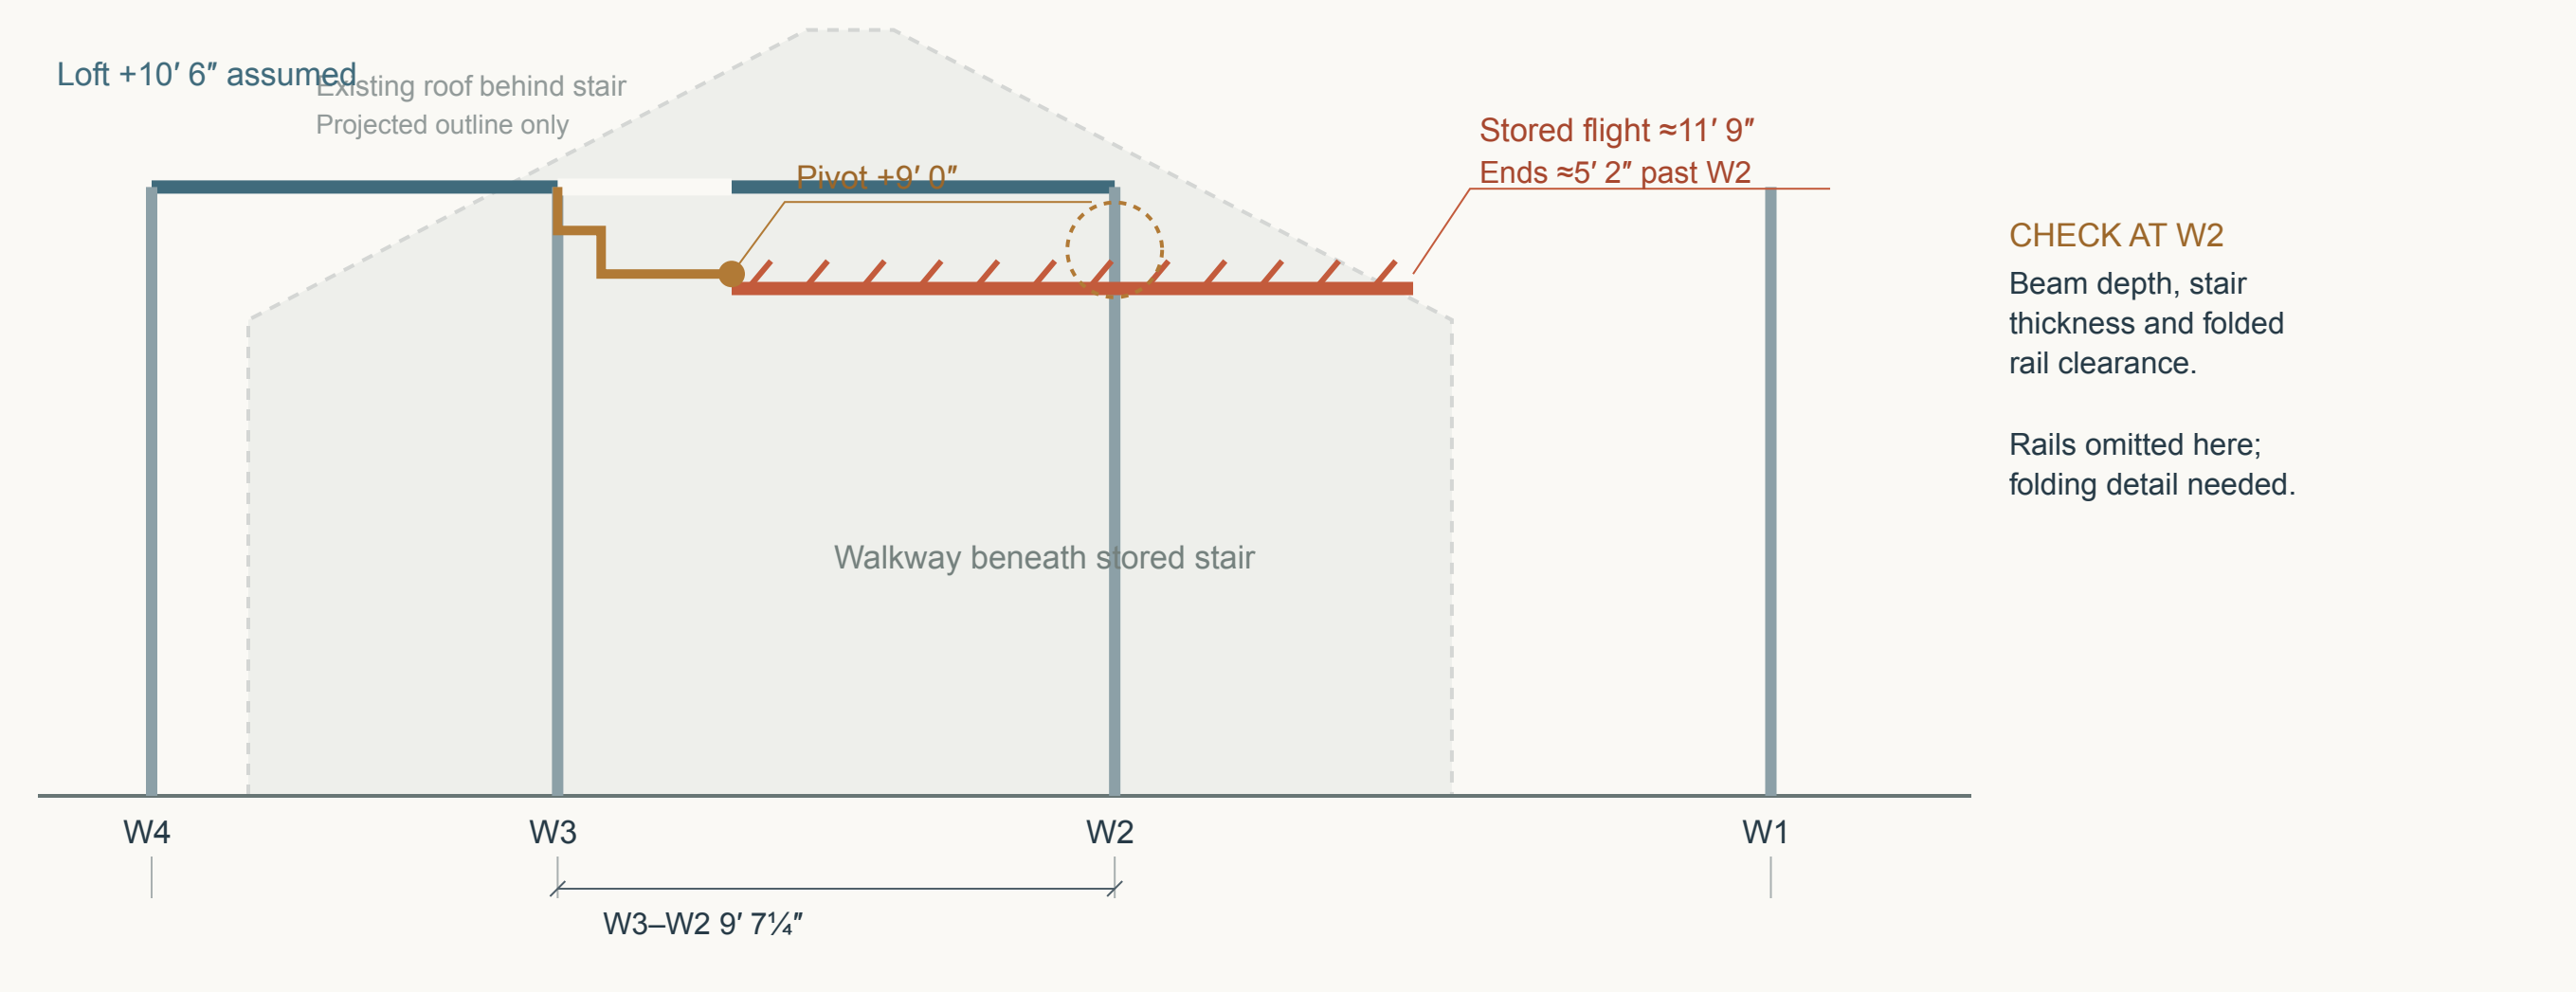

02 / STAIR LOWERED

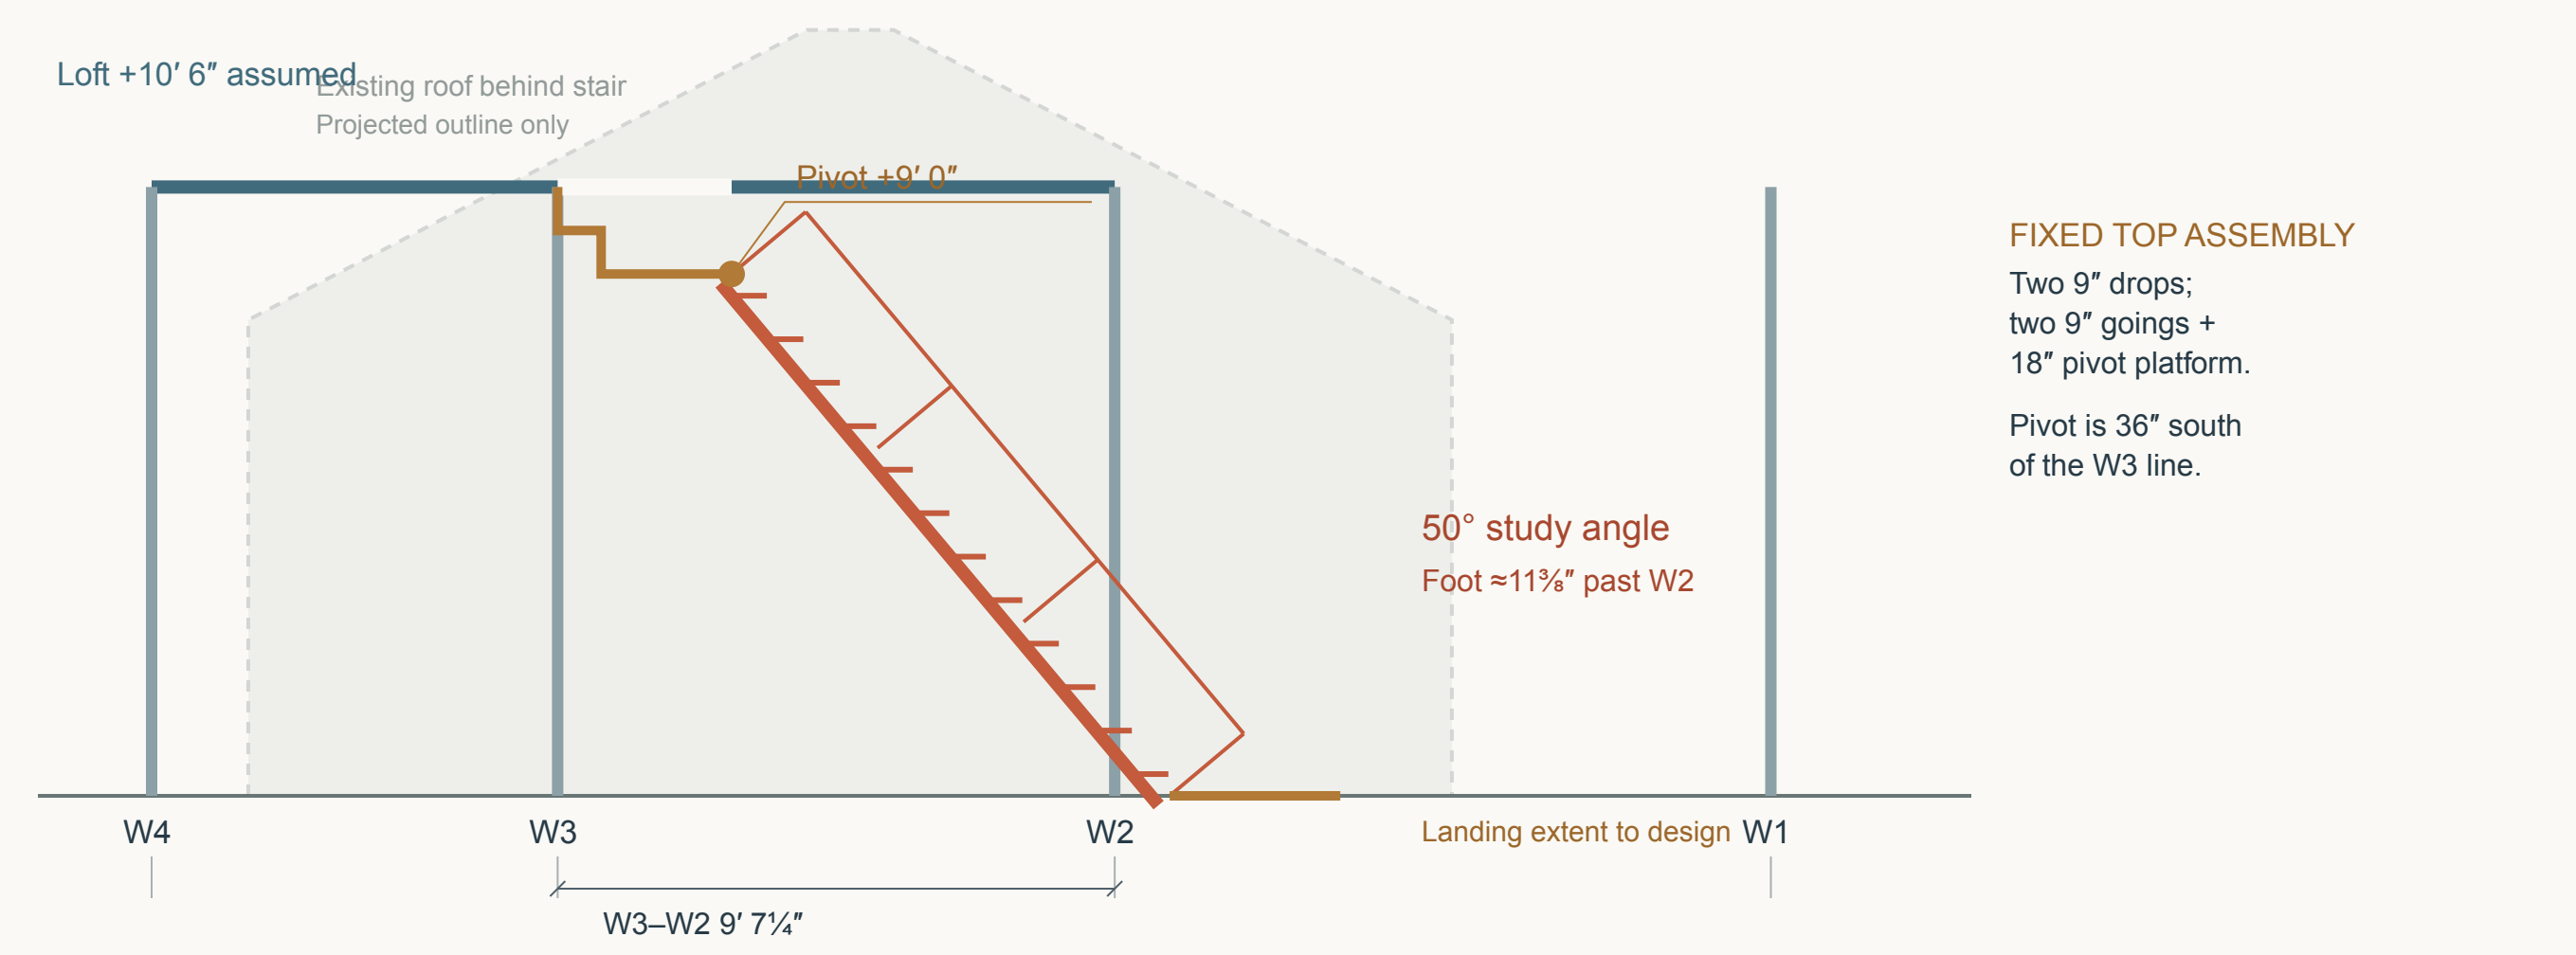

ASSUMPTIONS & LIMITS

Loft +126"; pivot +108"; level outside landing at 0". Heights and 50° pitch are illustrative, not adopted or code-approved.

Plan post locations retained. Fixed assembly, rails, pivot support, beam depths and counterbalance require design.

Retained roof is shown behind the stair in projection; this does not establish beam-to-roof clearance. Upper roof omitted.

Sources: ARCH-006 rev 4 basis.json (plan); model/parameters.json (existing roof). No controlled report drawings changed.