



Flat-cap garage · integrated photovoltaic roof

ELEVATIONS FIRST / Heights from garage ground datum / Concept dimensions, not construction details


01 WEST ELEVATION · looking east

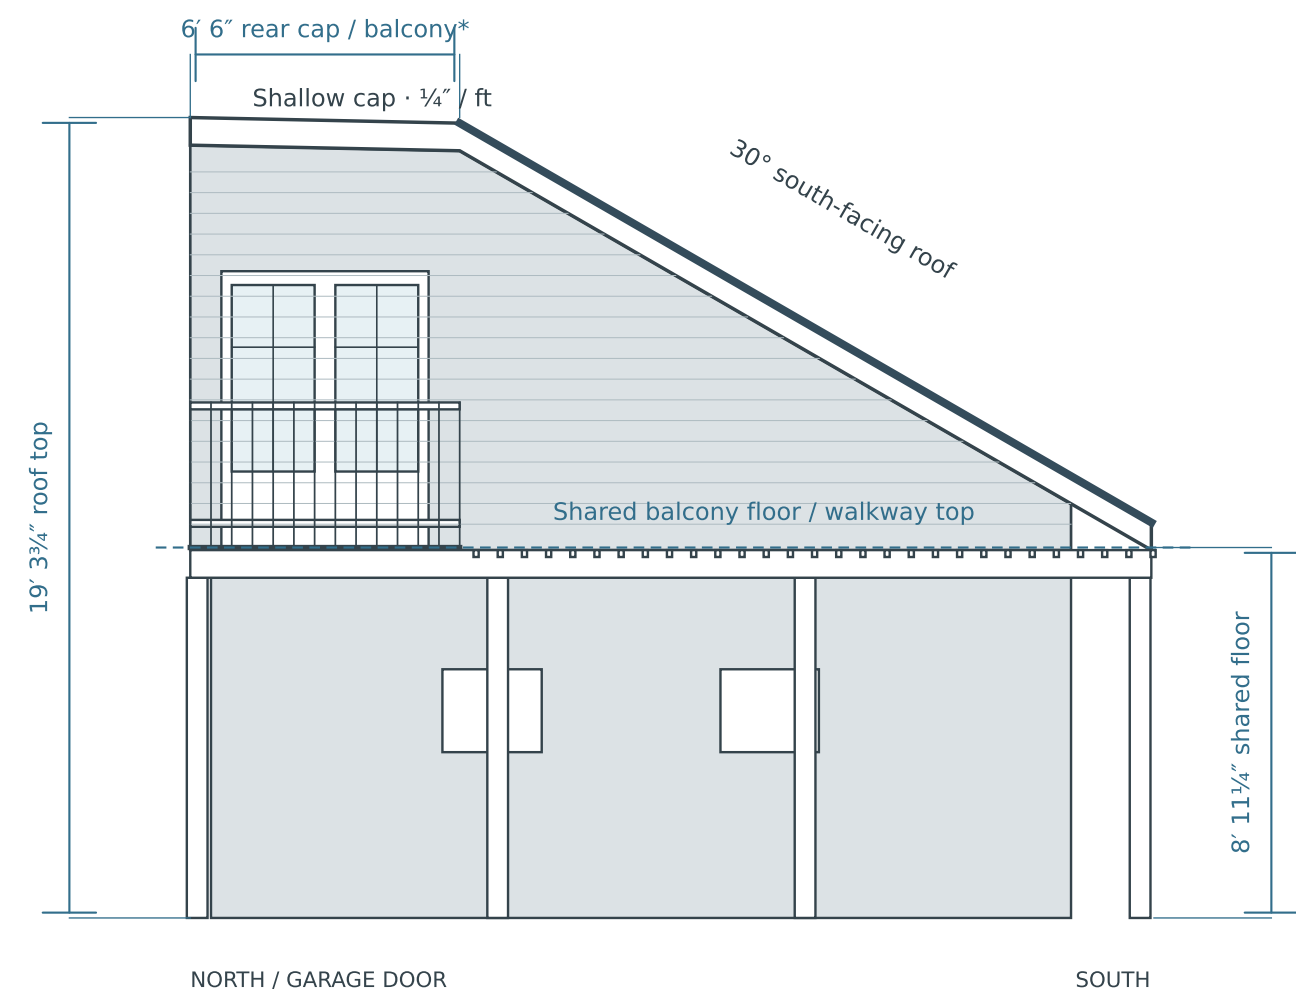

02 SOUTH ELEVATION · looking north

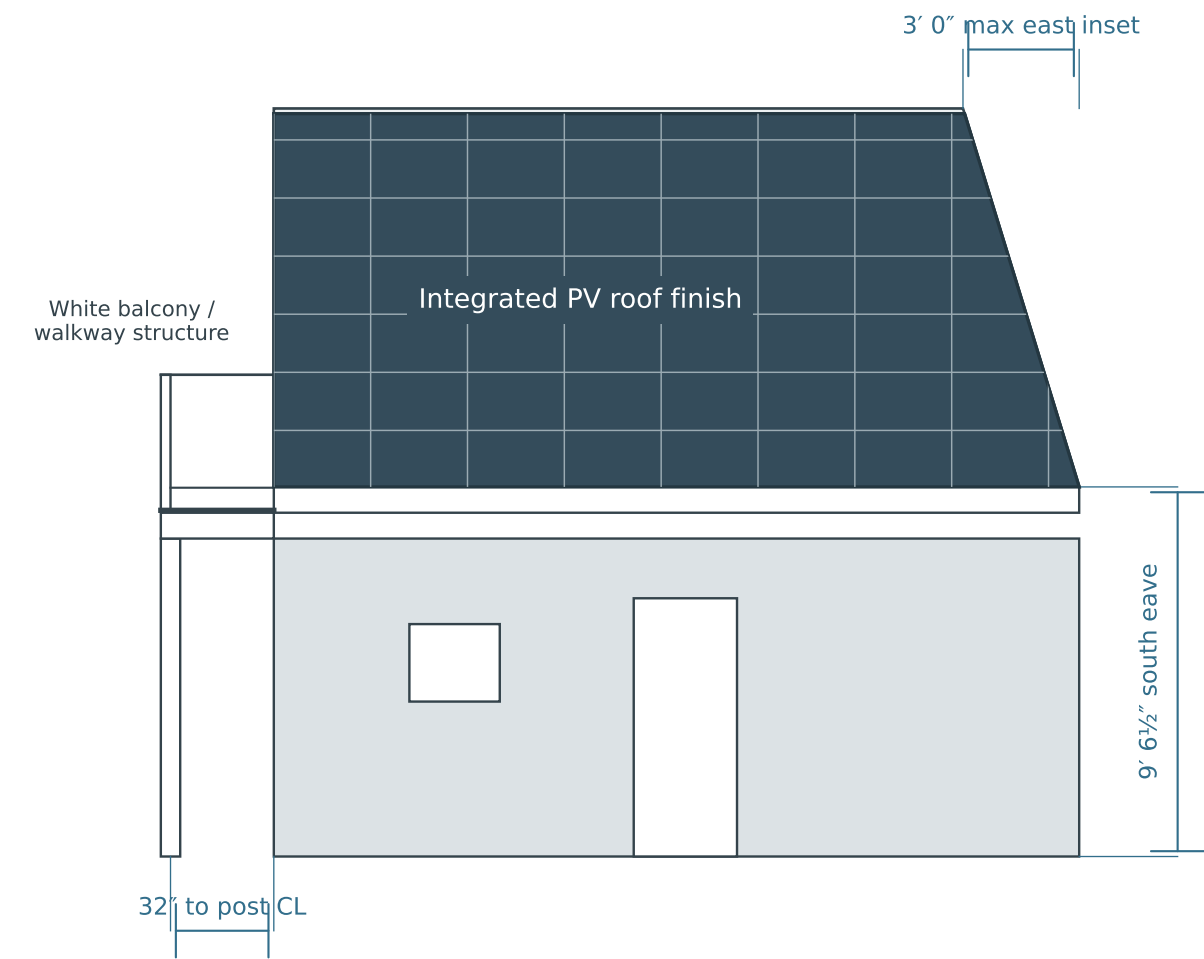

03 WEST WALKWAY / BALCONY SECTION · diagram

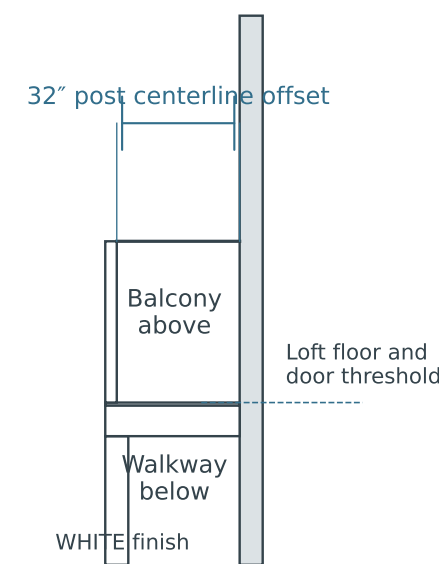


REVISION FOR REVIEW

- Rear flat-cap option retained; full-slope option dropped.
- No lattice rises from the walkway to the main roof.
- One west beam/post row: 32 inches from the existing wall.
- Walkway roof and balcony floor share the loft floor level.
- Balcony, fascia, posts and beam shown white.
- Horizontal members over the remaining walkway; solid walking surface beneath the balcony and French doors.

* Provisional: balcony spans the 6 ft 6 in rear zone;
French doors 5 ft × 6 ft 8 in; railing 42 in high.
Existing assumptions retained: 8 in beam + 3/4 in deck.
Assembly thickness, drainage and connections need design.
No new east/south covered passage inferred in this sheet.

Integrated solar roof · assembly intent

CONCEPT SECTION · exploded for clarity · not to scale

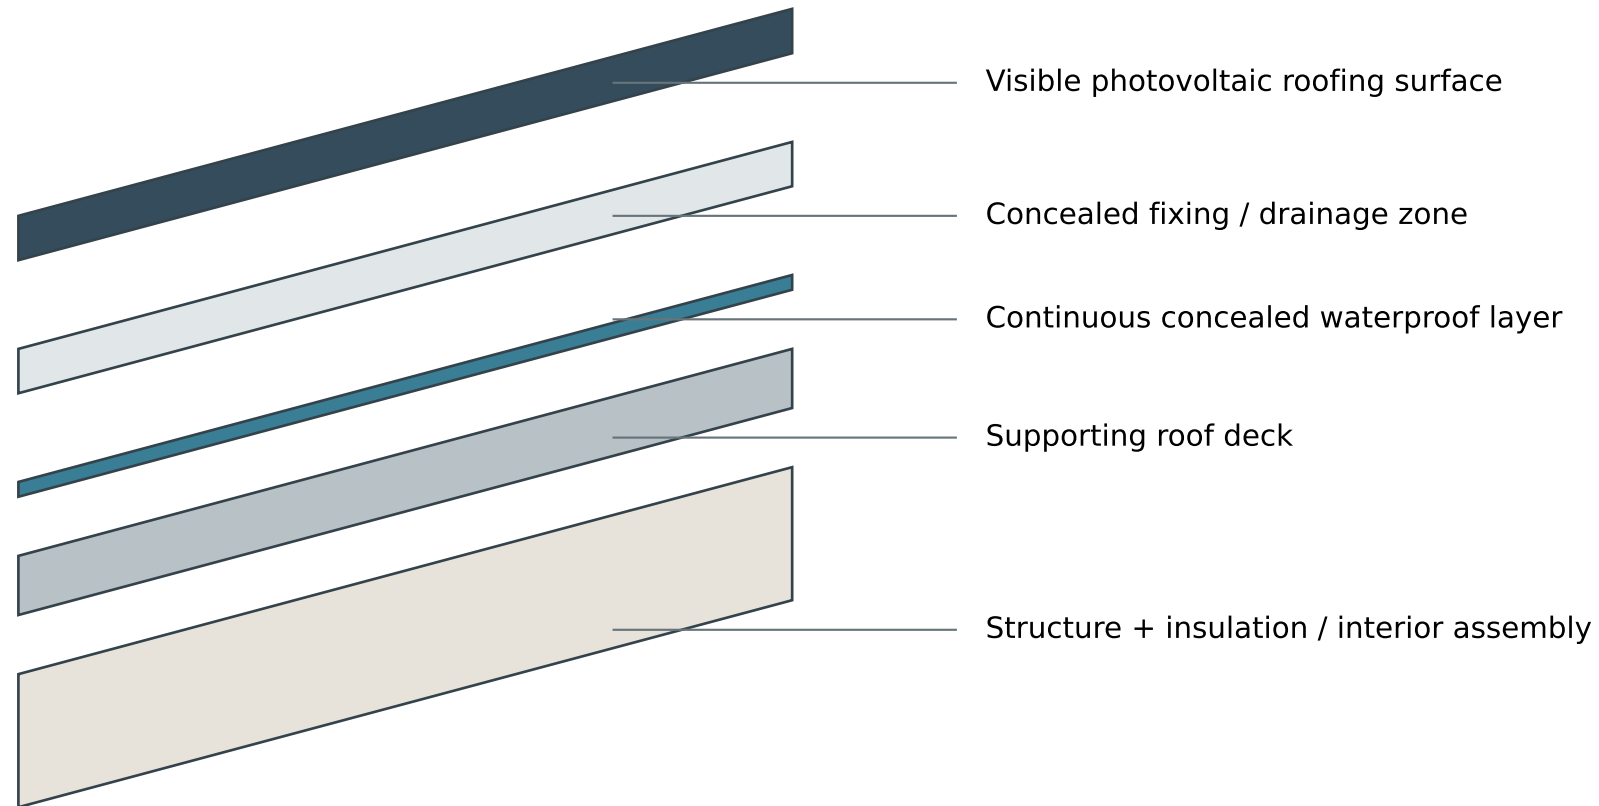

30° roof pitch; no raised rack profile. Layer depths and ventilation depend on the selected system.

Design intent: spend on waterproofing and durability, not the appearance of hidden layers.
PV joints, edge flashings and the transition to the shallow rear cap must form a coordinated roofing system.