


SOUTH ELEVATION · TRUSSES AND FRAMING

Looking north | West left · East right | Roof and wall cladding hidden

Dark: south outer frame at Y-63 and T-S at Y0 in. Pale: framing farther north.

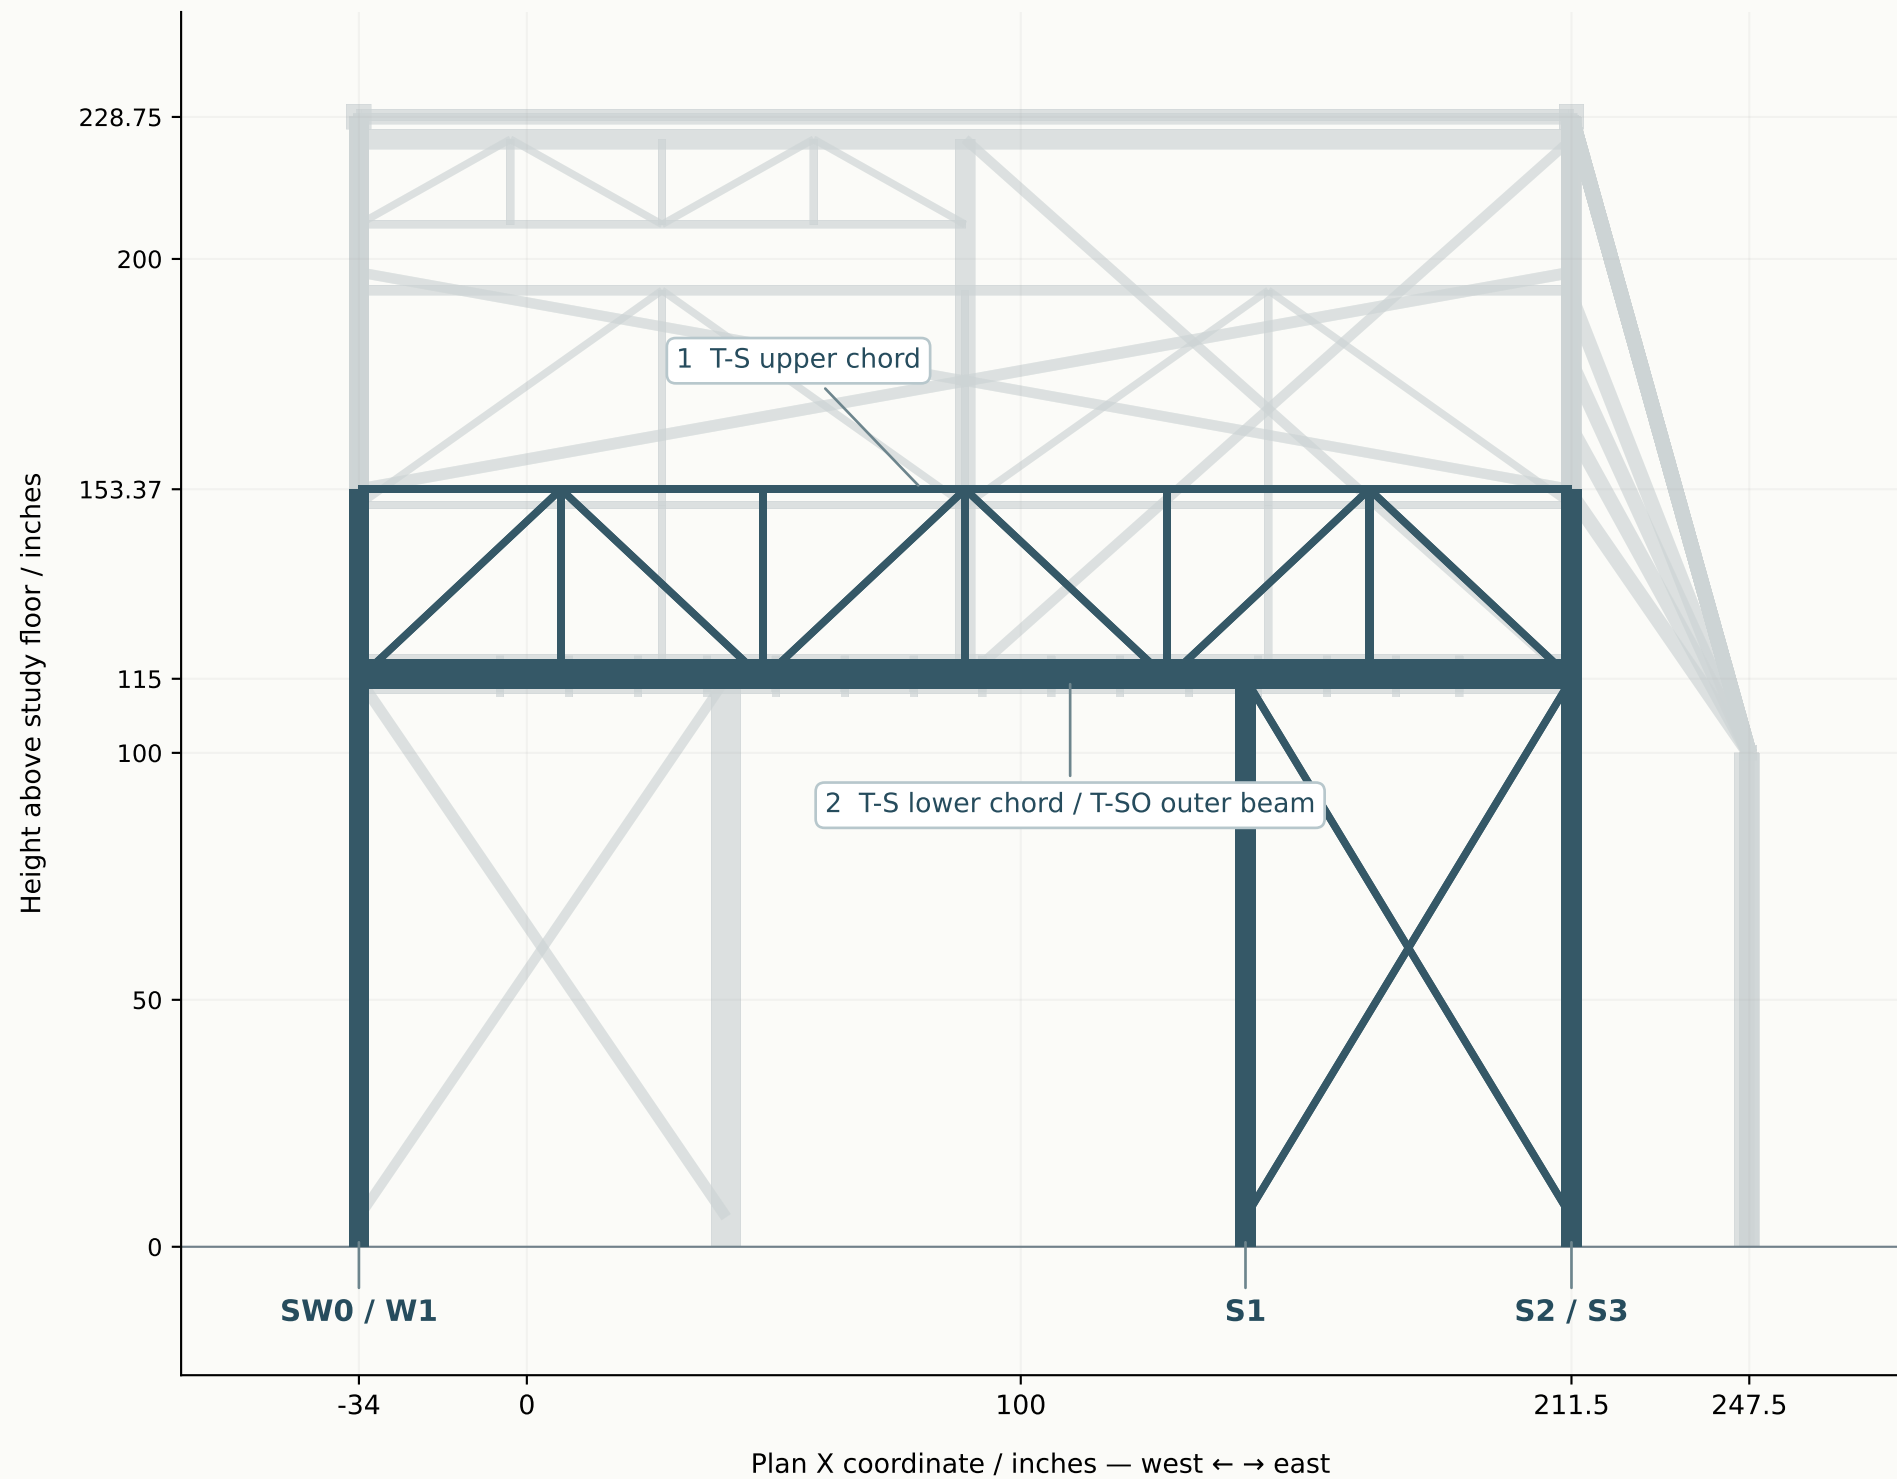

Linked to frame-spec.json → COMPAS joint graph and member model. Includes corrected east supports; S2-S3 braces removed.
Geometric study; joint detailing and structural sizing remain unresolved. Mesh projection with depth ordering; not a fabrication drawing.